

69 Bawtry Road

Sheffield, S9 1UA



Location Plan
Scale: 1:500



REF	DESCRIPTION	DATE	DRAWN
10/10/14	10/10/14	10/10/14	10/10/14
1/1000MAY	July 2014	10/10/14	10/10/14

Mr Van T Pham

PROPOSED 1 STOREY HOUSE
69 BAWTRY ROAD, SHEFFIELD

LOCATION PLAN

DATE	REVISION	REVISION
14/01	UP01	UP01

Proposed New 3 bed Semi-detached House

69 Bawtry Road, Sheffield, S9 1UA



09/12/16 - rev B - ingress and egress and visibility splay revised, following planning officer comment

PH

31/10/16 - rev A - drawing revised, showing ingress and egress and visibility splay, following planning officer comment

PH

REF	DESCRIPTION	DATE	STATUS
1000000	1000000	1000000	1000000
1000000	1000000	1000000	1000000

Mr Van T Pham


PROPOSED 3 BED SEMI DETACHED HOUSE
69 BAWTRY ROAD, SHEFFIELD

PROPOSED SITE PLAN


REF	DESCRIPTION	DATE
1401	1401	1401

69 Bawtry Road

Sheffield, S9 1UA

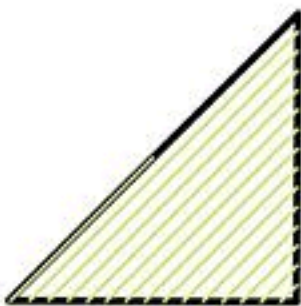

2mX2m Visibility splay

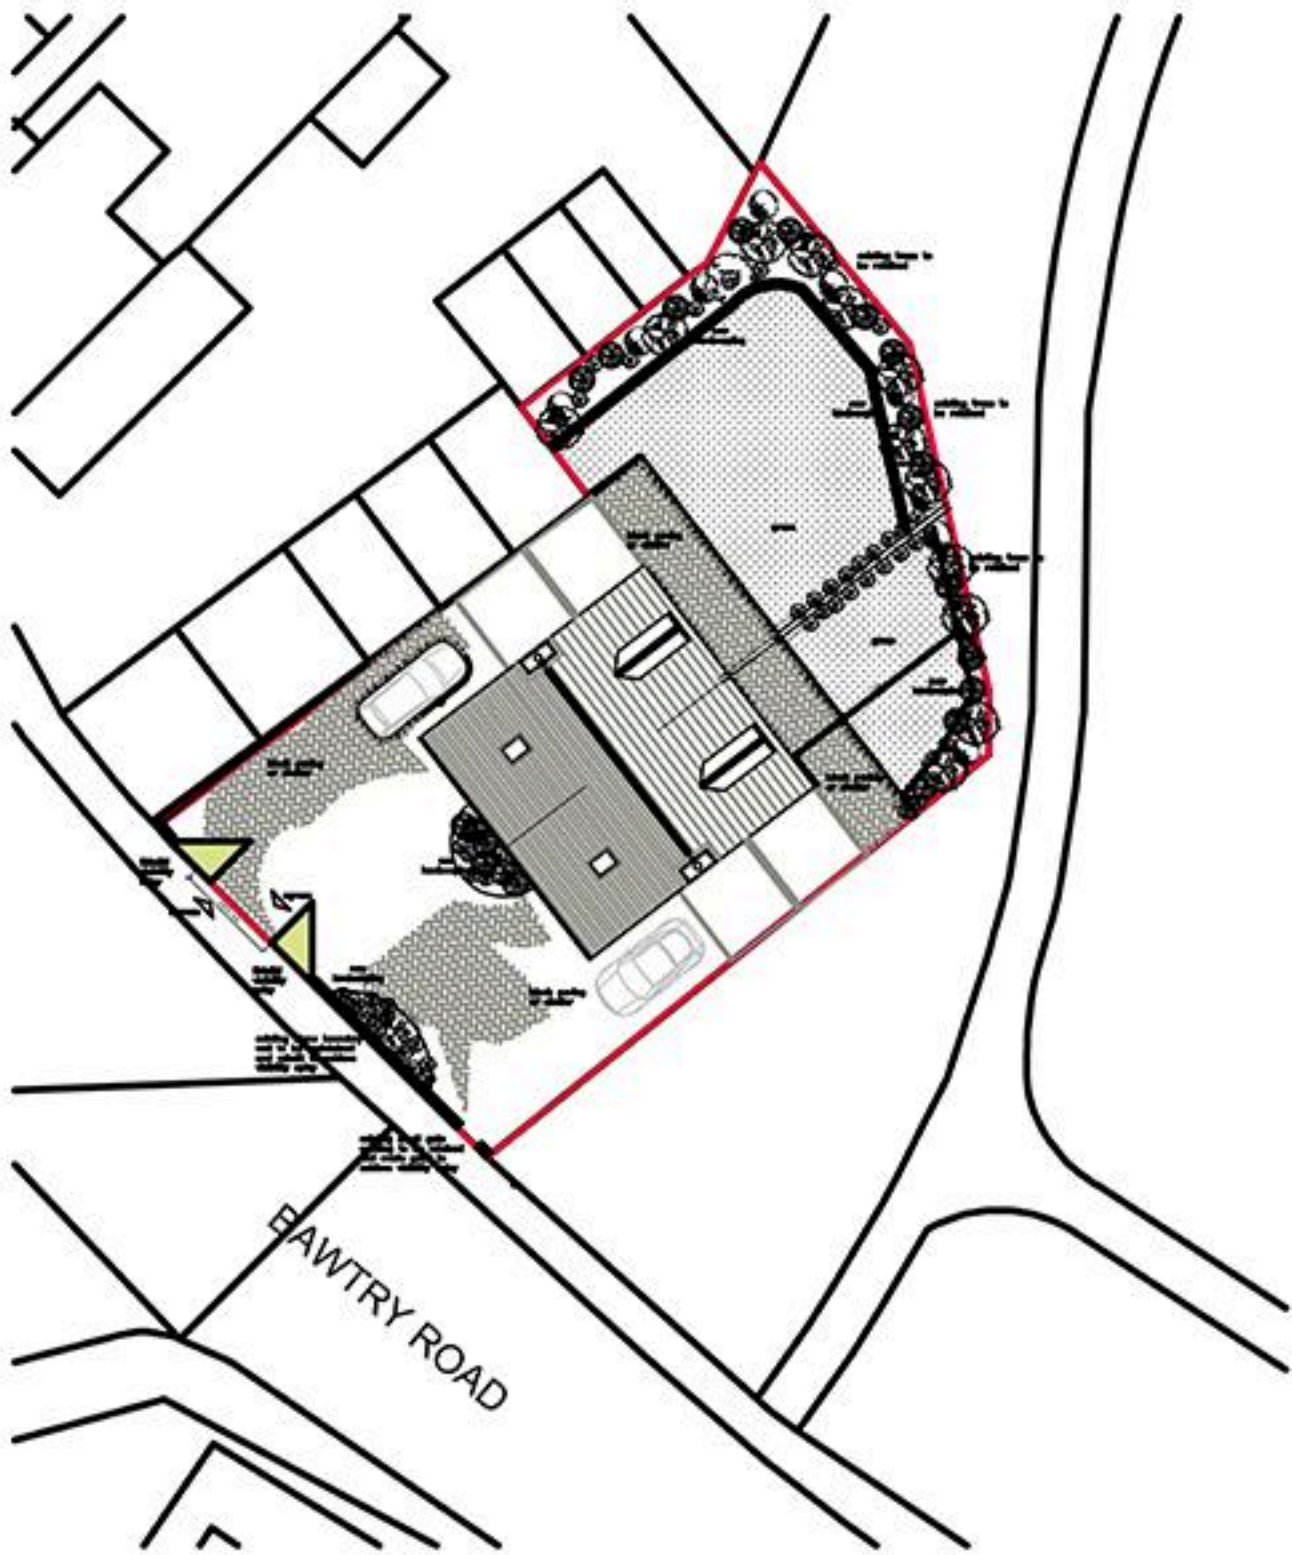

Visibility Splay Plan

Scale: 1:500




REF	DESCRIPTION	DATE	DRAWN
REVISIONS			
SCALE	DATE	DRAWN BY	
1:100, 1:250000	25/04/18	PBN	
CLIENT			

Mr Van T Pham

JOB TITLE		
PROPOSED 1 STOREY HOUSE 69 BAWTRY ROAD, SHEFFIELD		
DRAWING TITLE		
PROPOSED VISIBILITY SPLAY		
JOB NO.	DRAWING NO.	REVISION
14.01	V301	

Proposed New 3 bed Semi-detached House

69 Bawtry Road, Sheffield, S9 1UA

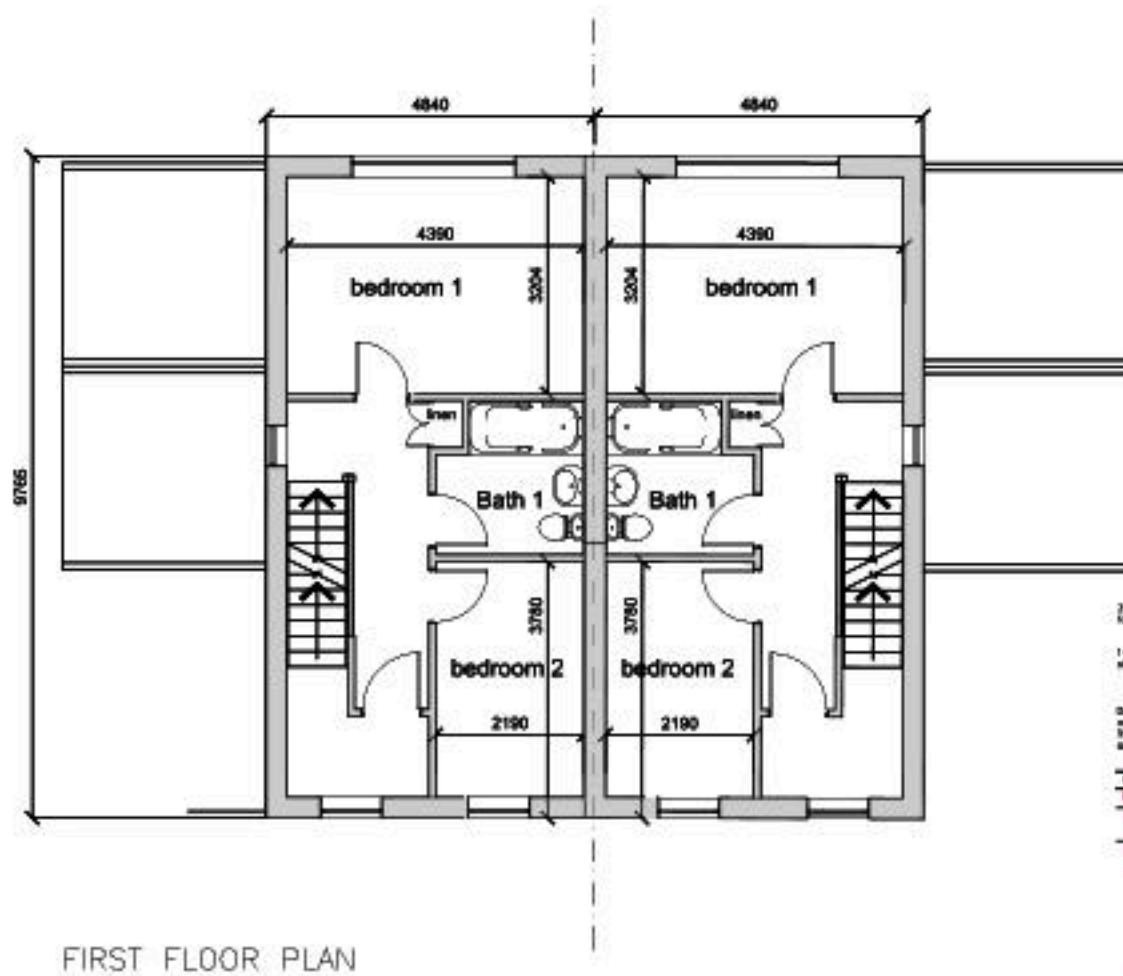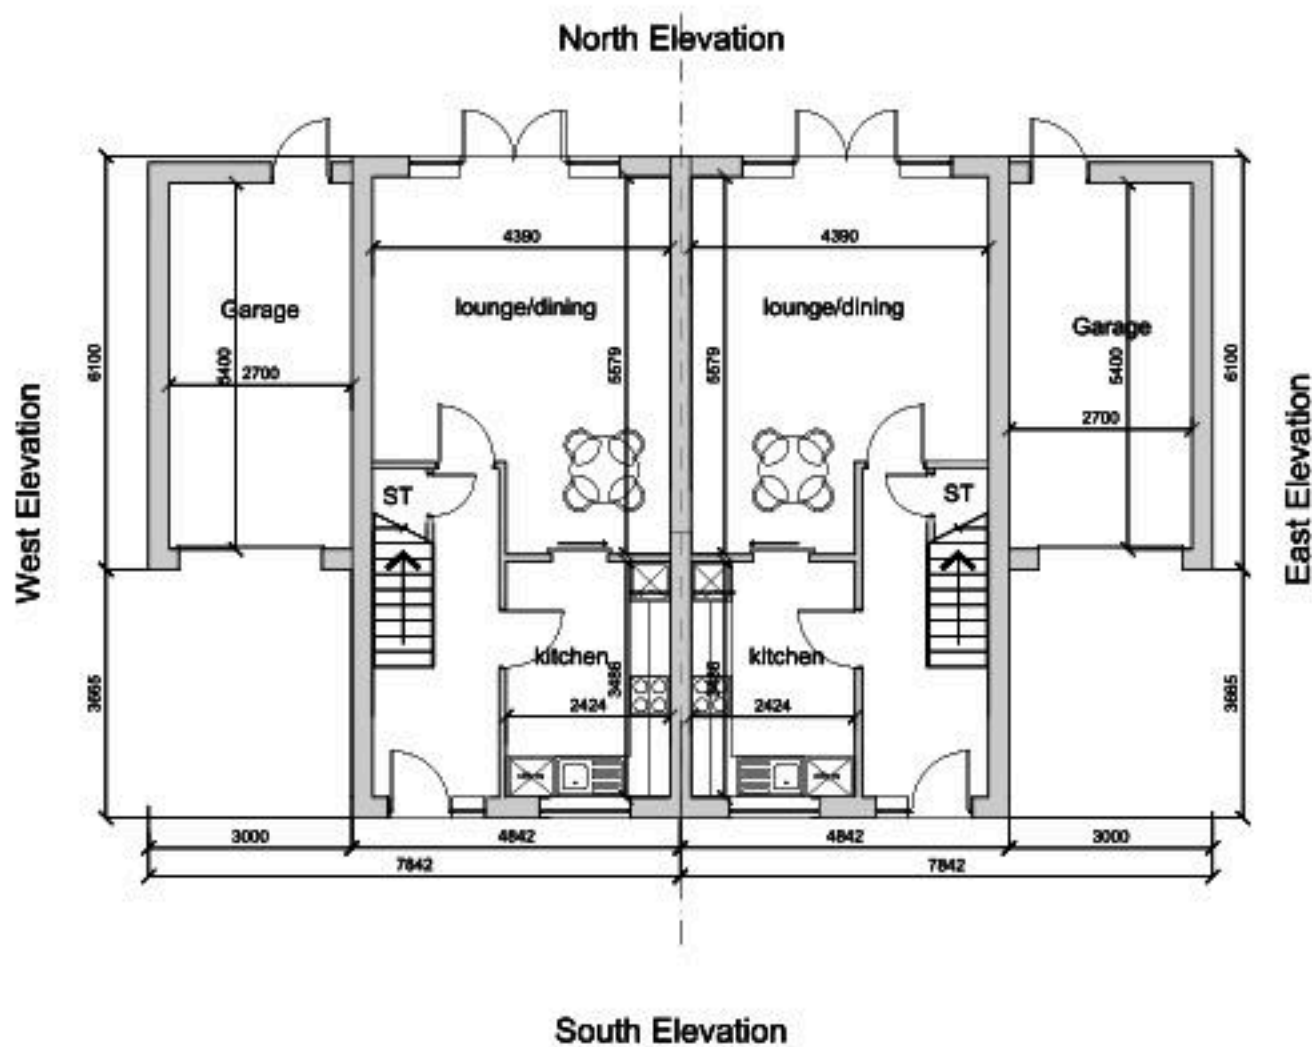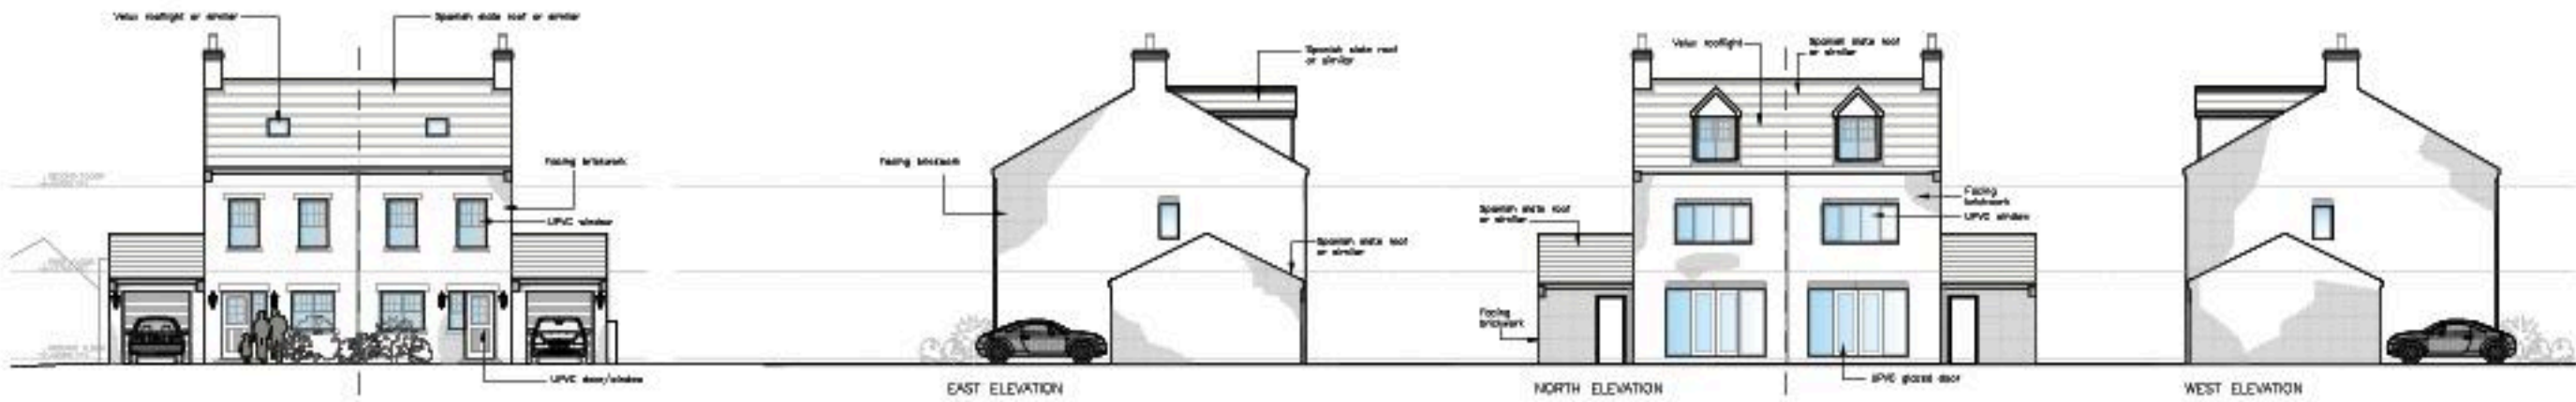

PROPOSED GROUND FLOOR
SCALE:1:50
0 5m

21/11/16 - rev B - showing revised garage moved back following planning refusal comment.
14/10/18 - rev A - showing revised following planning refusal comment.
Do not scale. Allowing all dimensions to be confirmed prior to construction and any discrepancies confirmed to architect.
This drawing is to be used in conjunction with all other architectural and structural drawings.

NO	REVISION	DATE	BY
1	ISSUED FOR PERMIT	28.04.18	PH

Mr Van T Pham


PROPOSED 3 BED SEMI DETACHED HOUSE
69 BAWTRY ROAD, SHEFFIELD S9 1UA

PROPOSED FLOOR PLANS
AND ELEVATIONS


NO	REVISION	DATE	BY
1	ISSUED FOR PERMIT	28.04.18	PH

Proposed New 3 bed Semi-detached House

69 Bawtry Road, Sheffield, S9 1UA

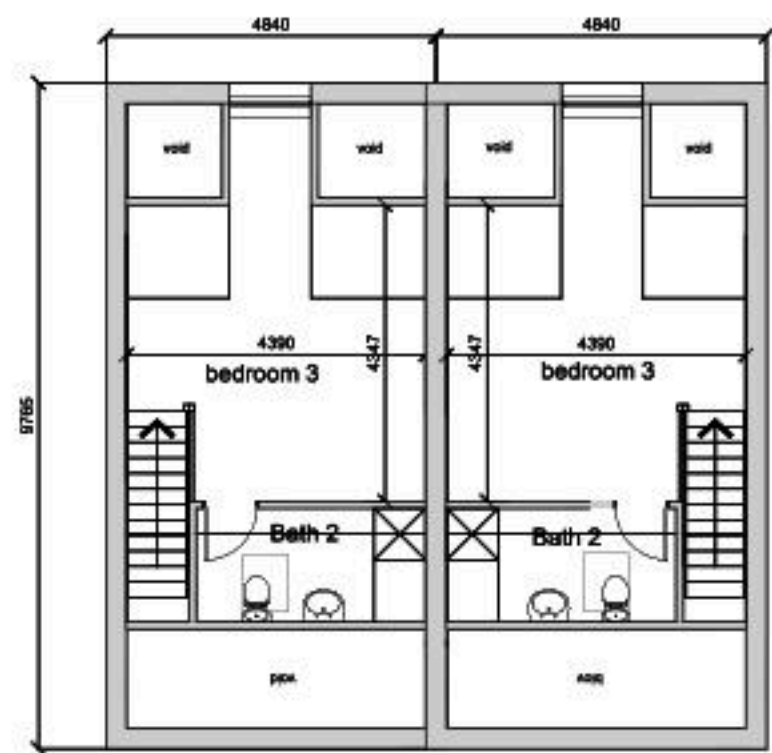

SECOND FLOOR PLAN

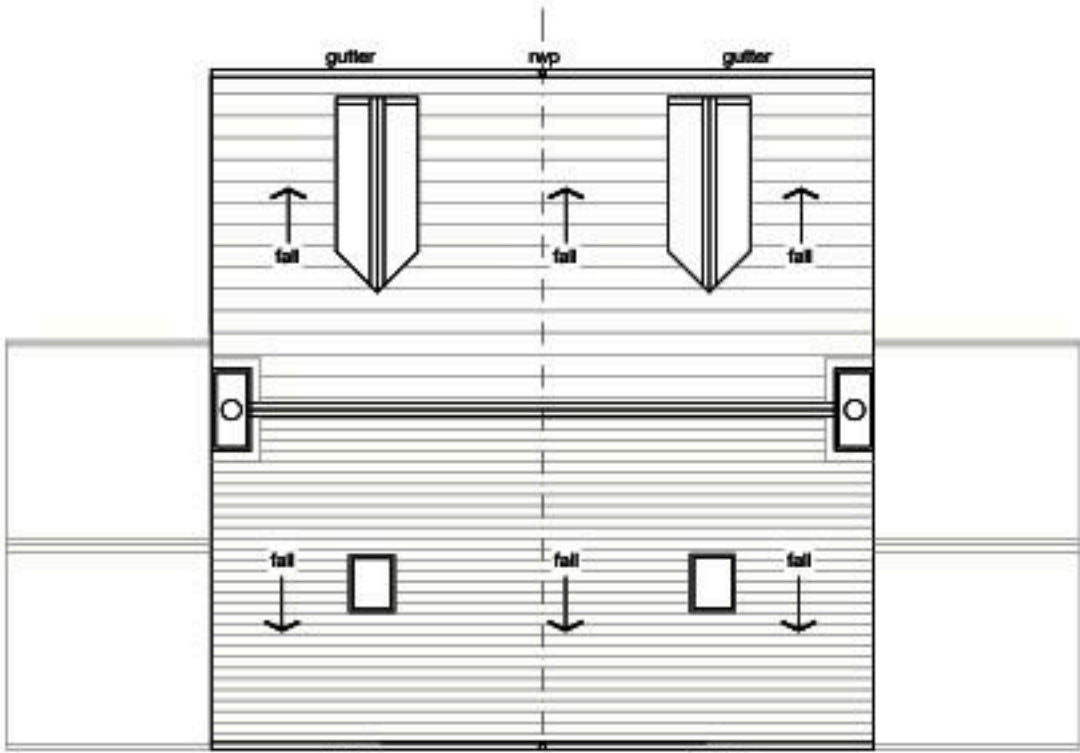

ROOF PLAN

14/11/10 - rev A - drawing revised following planning approval comment

Do not scale. All setting out dimensions to be site confirmed prior to works commencing and any discrepancies corrected to construct. This drawing is to be read in conjunction with all other architectural and structural engineers drawings.

REV		DESCRIPTION	DATE
1	14/11/10	14/11/10	PM

Mr Van T Pham

PROPOSED 3 BED SEMI DETACHED HOUSE
69 BAWTRY ROAD, SHEFFIELD S9 1UA

PROPOSED SECOND FLOOR PLAN
AND ROOF PLAN

SCALE	DATE	BY
1:100	14/11/10	PM

Proposed New 3 bed Semi-detached House

69 Bawtry Road, Sheffield, S9 1UA



PROPOSED STREET ELEVATIONS



14/10/18- rev A - drawing revised following planning officer comment.

Do not scale. All setting out dimensions to be site confirmed prior to works commencing and any discrepancies confirmed to architect. This drawing is to be read in conjunction with all other architectural and structural engineers drawings.

REV	DESCRIPTION	DATE	DRAWN
REVISIONS			
1	1:10000A2	28.09.18	PM
CLIENT			

Mr Van T Pham

PROPOSED 3 BED SEMI DETACHED HOUSE
69 BAWTRY ROAD, SHEFFIELD S9 1UA

PROPOSED BAWTRY STREET ELEVATIONS

JOB NO.	DRAWING NO.	REVISION
14.01	PL04	A