

11 CHORLEY ROAD, SHEFFIELD, S10 3RJ



Proposed Elevations


[illegible]

Great Gilling

11 CHORLEY ROAD, SHEFFIELD, S10 3RJ




Proposed Elevations
Scale: 1:100

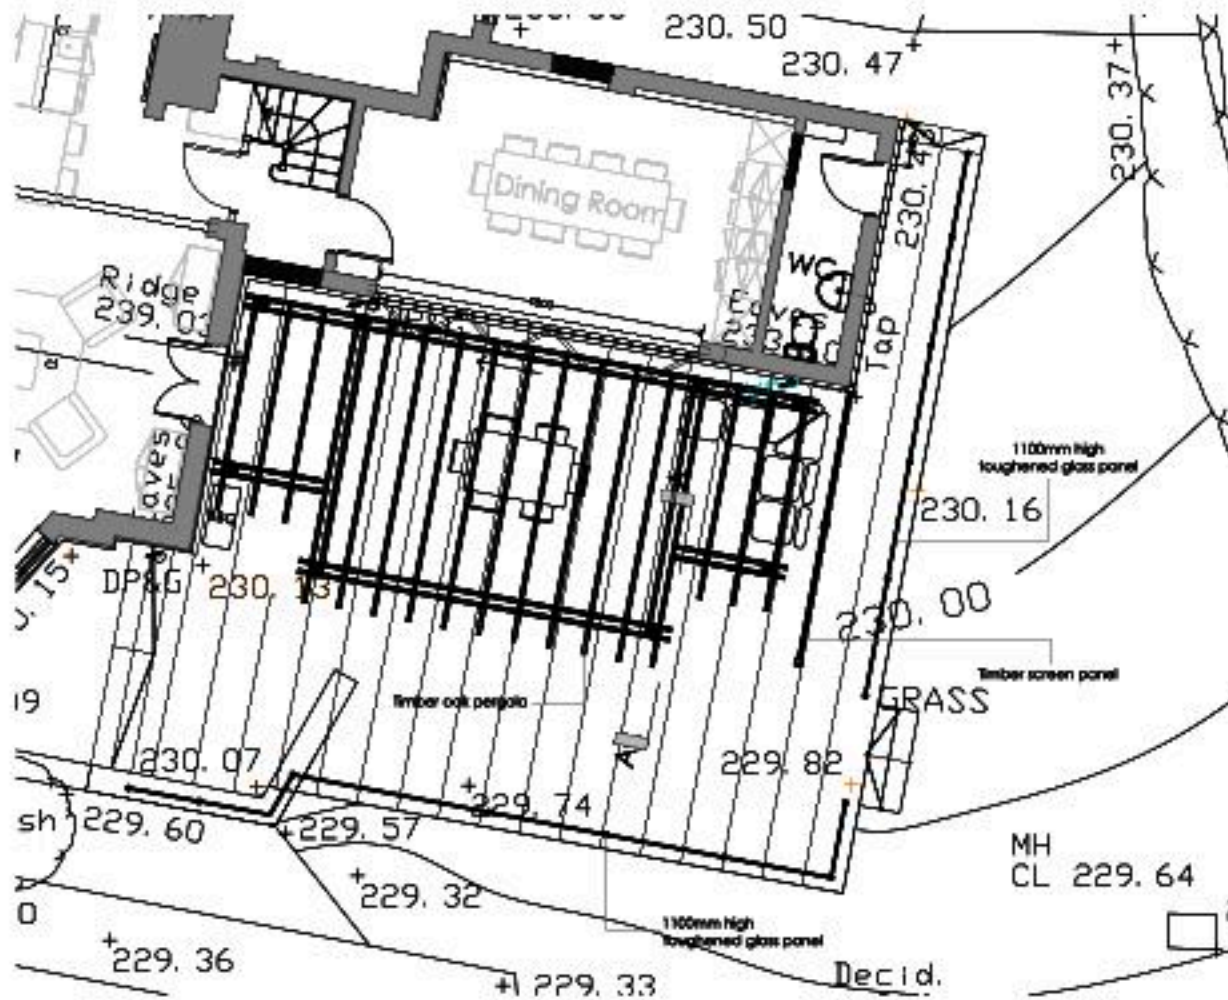

Proposed Plan
Scale: 1:50

Proposed External Works

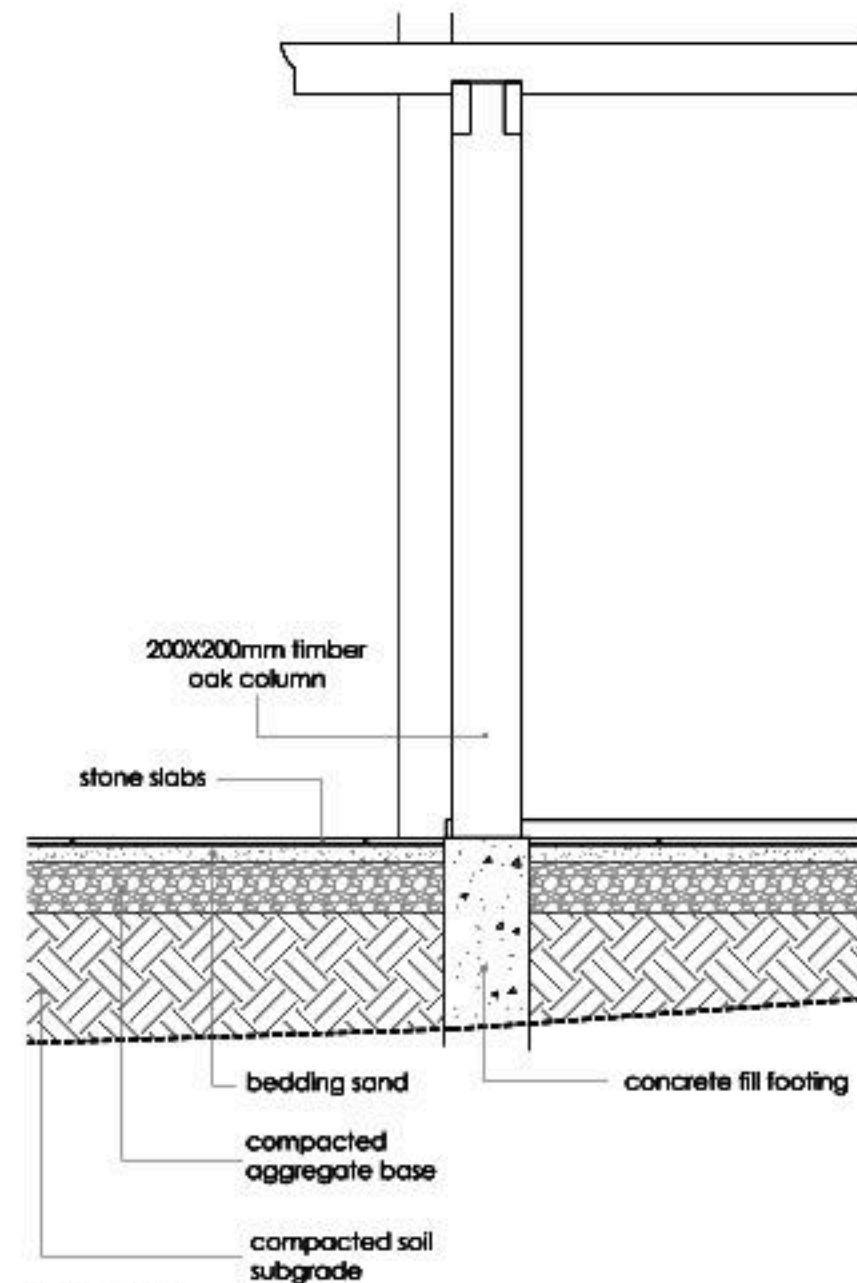


Section A-A
Scale: 1:10


THIS DRAWING IS THE PROPERTY OF CORDONIER & ASSOCIATES LTD. IT IS TO BE USED ONLY FOR THE PROJECT AND SITE SPECIFICALLY IDENTIFIED HEREON. IT IS NOT TO BE REPRODUCED, COPIED, OR TRANSMITTED IN ANY FORM OR BY ANY MEANS, WITHOUT THE WRITTEN PERMISSION OF CORDONIER & ASSOCIATES LTD.			
CORDONIER & ASSOCIATES LTD. 10 LANG LANE SHEFFIELD S11 7TX Tel: +44 (0)114 262 1000 Fax: +44 (0)114 262 0000 www.cordonier.com			
DRAWING STATUS			
DATE	BY	APP'D	DATE
1/1/20	1/1/20	1/1/20	1/1/20
PREPARED	✓	APP'D	DATE
DESIGNED	✓	APP'D	DATE
CONSTRUCTED	✓	APP'D	DATE
REVISIONS			
NO	DATE	DESCRIPTION	BY
A	1/1/20	Drawing updated	PN PM
B	1/1/20	Drawing updated	PN PM
C	1/1/20	Drawing updated	PN PM
D	1/1/20	Drawing updated	PN PM
NOTES			
MR & MRS HUDSON			
CORDONIER Chartered Architects			
PROJECT NO: GREAT GILLING 11 CHORLEY ROAD, S10 3RJ			
DRAWN BY: PROPOSED PERGOLA & ELEVATIONS			
1/1/20	PNM	PM	D

Great Gilling

11 CHORLEY ROAD, SHEFFIELD, S10 3RJ

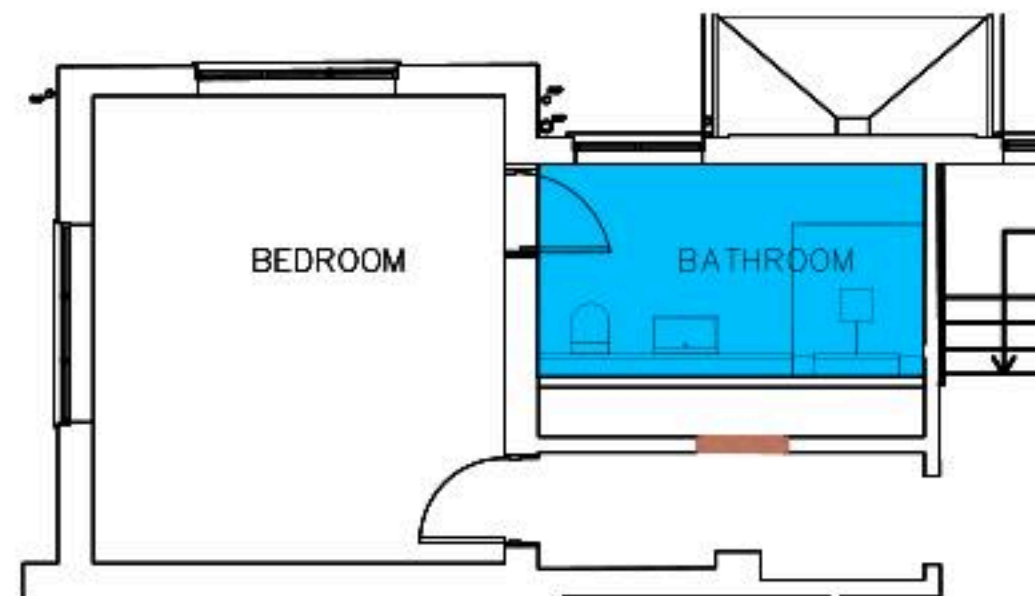

First Floor Bathroom

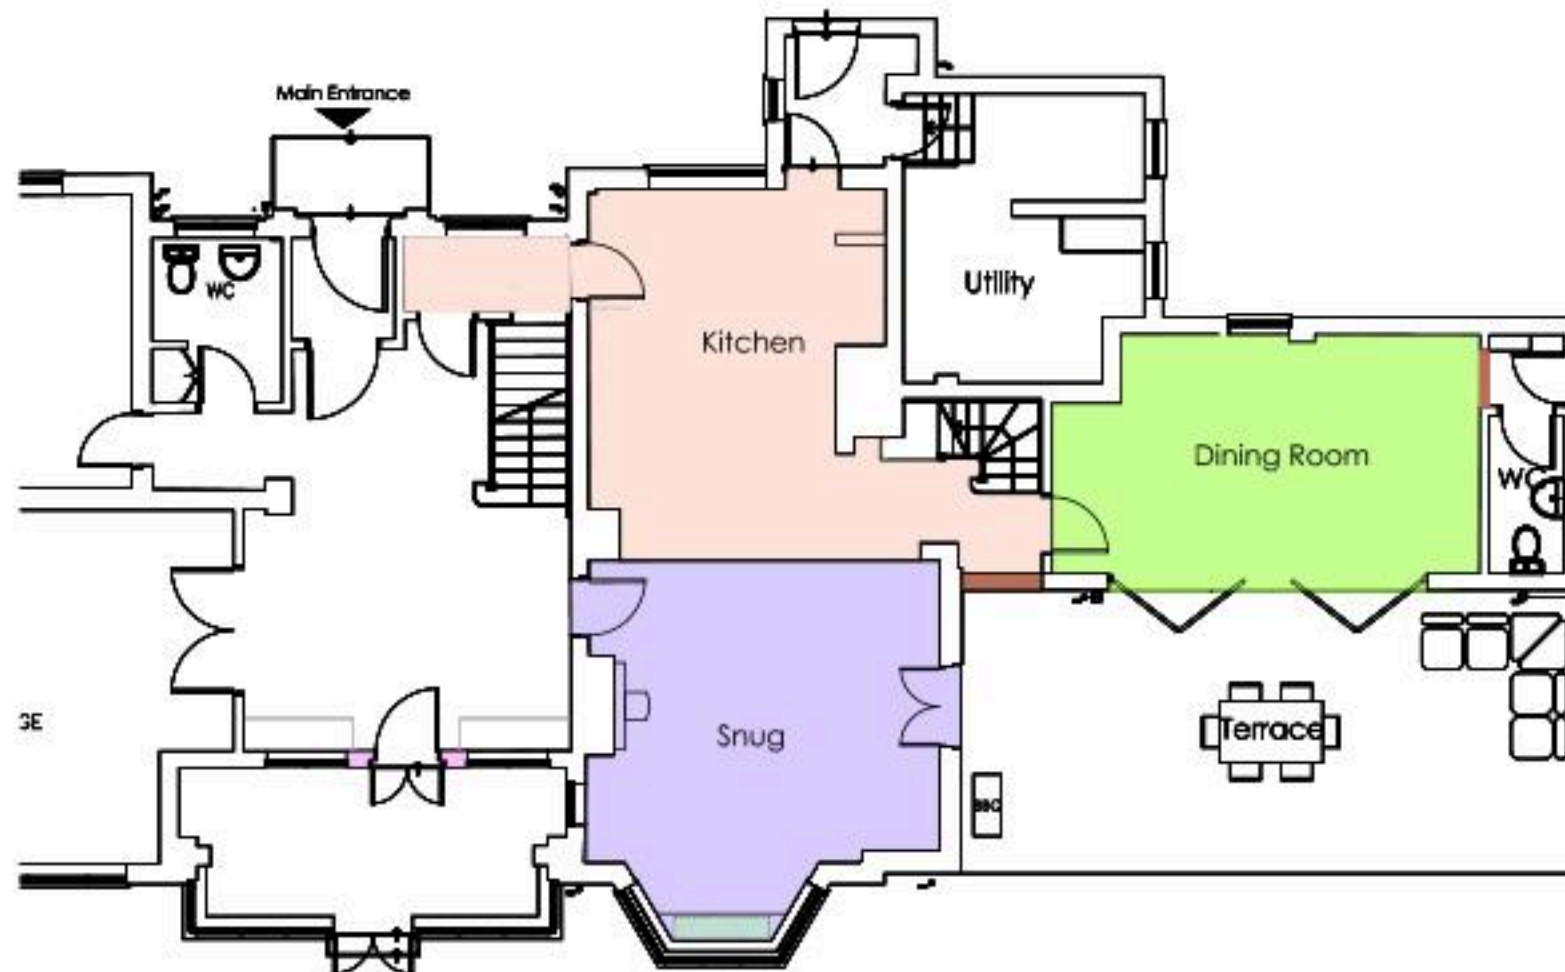

Ground Floor

Key

- Underfloor heating Zone 1
- Underfloor heating Zone 2
- Underfloor heating Zone 3
- Underfloor heating bathroom Zone 4

Proposed Underfloor Heating

THIS DOCUMENT, TOGETHER WITH THE BASIC DESIGN STATEMENT, IS A PRELIMINARY DESIGN AND NOT A CONTRACT DOCUMENT. IT IS THE PROPERTY OF CORDONIER ARCHITECTS AND SHOULD NOT BE REPRODUCED OR USED FOR ANY OTHER PROJECT WITHOUT THE WRITTEN PERMISSION OF CORDONIER ARCHITECTS.

DATE: 14/03/2012
 DRAWN BY: JH
 CHECKED BY: JH
 APPROVED BY: JH
 PROJECT NO: 11/03/2012
 CLIENT: MR & MRS HUDSON
 PROJECT: GREAT GILLING
 ADDRESS: 11 CHORLEY ROAD, S10 3RJ

REVISIONS

NO	DATE	BY	REASON
A	14/03/2012	JH	PN

NOTES

BASED ON DRAWING A1/01, A1/02 AND A1/03 DATED NOV 2012 FROM TATLOW STANIER ARCHITECTS

MR & MRS HUDSON

CORDONIER
 Chartered Architects
 18 Longside
 Sheffield
 S10 2TC
 Tel: +44 (0)114 262 1888
 Fax: +44 (0)114 262 0950
 www.cordonier.com


GREAT GILLING
 11 CHORLEY ROAD, S10 3RJ

PROPOSED UNDERFLOOR HEATING


14/03/2012

Great Gilling

11 CHORLEY ROAD, SHEFFIELD, S10 3RJ

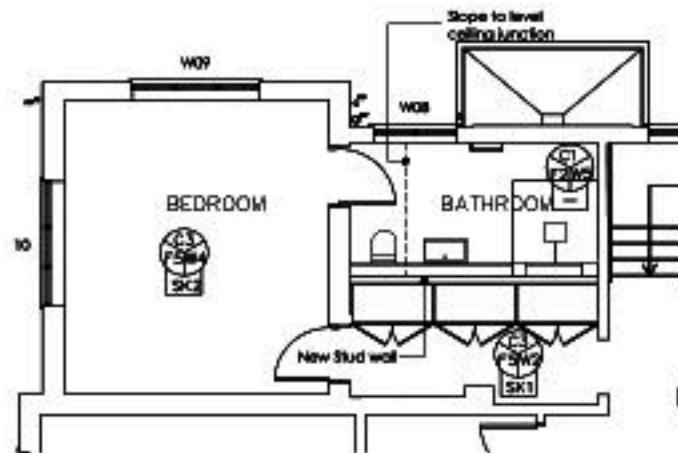

First Floor Plan

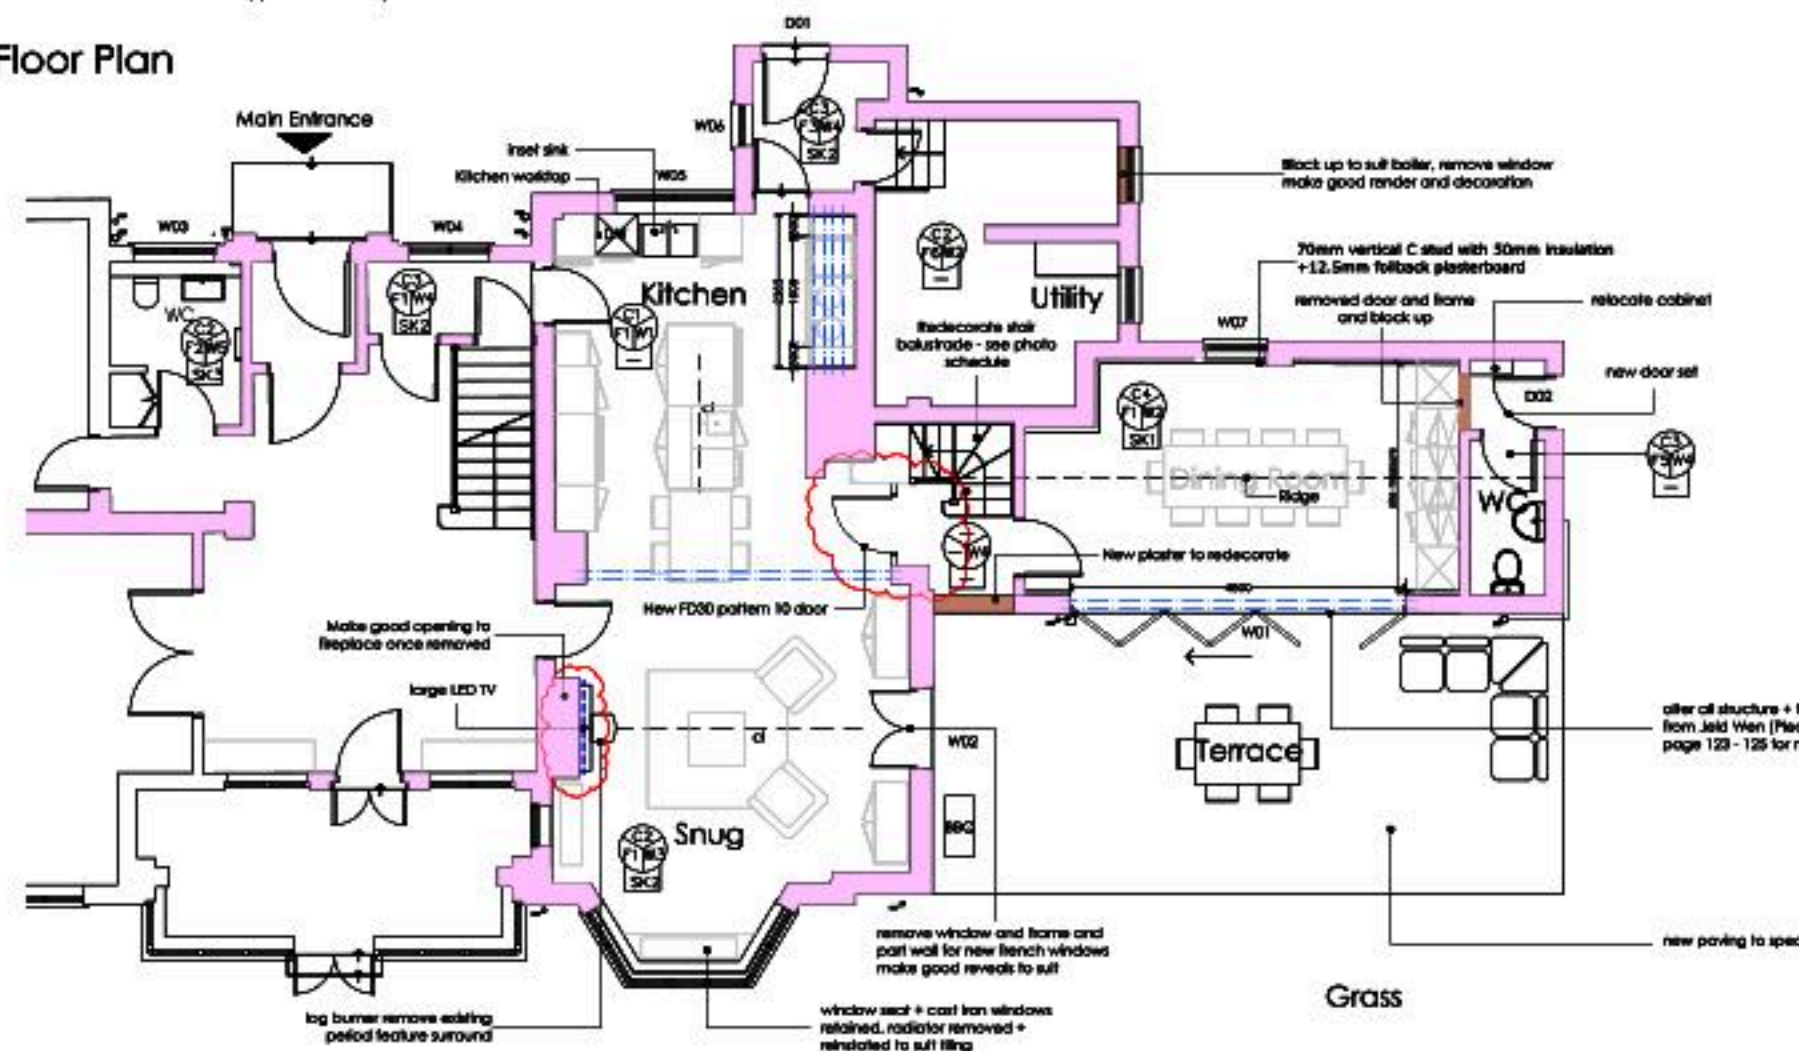

Ground Floor Plan

Proposed General Arrangement & Finishes

Finishes Key

Ceilings

- C1 Overboard
- C2 MF ceiling
- C3 Redecorate to spec
- C4 Slope ceiling redecorate

Walls

- W1 Dot and dab + paint
- W2 Studwork wall + paint
- W3 Uni-bond + skir + paint (Strip all wall paper)
- W4 Redecorate
- W5 See H2O spec
- W6 Make good reveal, threads to all replacement window openings.

Floors

- F1 800x800mm floor tiles
- F2 Floor tiles (see H2O spec)
- F3 Color Melling - to sample approval
- F4 Painted
- F5 Flooring by others
- F6 Make good existing asphalt

Skirting Board

- SK1 Softwood skirtings painted
- SK2 Retain
- SK3 Tiled skirting

DRAWING STATUS			
DATE	14.08.14	DATE	14.08.14
DESIGNER	PN	APPROVED	PN
PREPARED	PN	APPROVED	PN
CONTRACTOR	PN	APPROVED	PN

NOTES

BASED ON DRAWING A1/01, A1/02 AND A1/03 DATED NOV 2013 FROM SATLOW STANICE ARCHITECTS

W6: To be read in conjunction with photo schedule + room data schedule

MR & MRS HUDSON

CORDONIER
Chartered Architects
18 Longline
Sheffield
S11 7TG
Tel +44 (0)114 262 1000
Fax +44 (0)114 262 1001
www.cordonier.com


GREAT GILLING
11 CHORLEY ROAD, S10 3RJ

PROPOSED GENERAL ARRANGEMENT AND FINISHES


14.08	14.08	A
-------	-------	---

Great Gilling

11 CHORLEY ROAD, SHEFFIELD, S10 3RJ

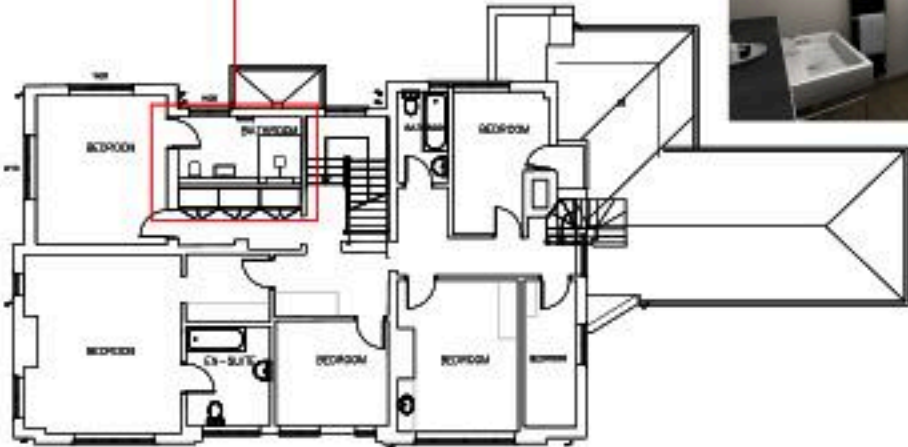

First Floor Plan

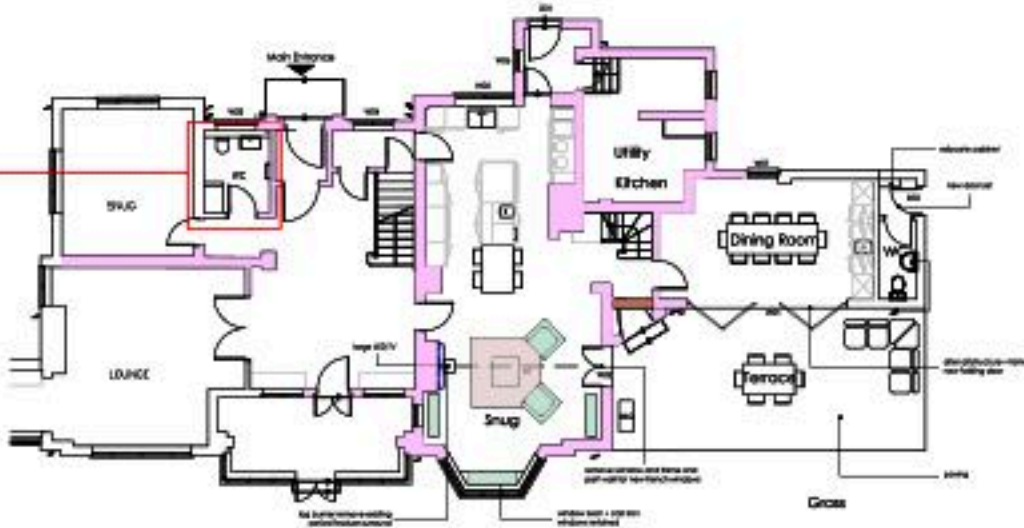

Ground Floor Plan



Please see H2O specification for more details

Please see H2O specification for more details

Proposed Bathroom Finishes

ALL DRAWINGS AND SPECIFICATIONS ARE THE PROPERTY OF CORDONIER ARCHITECTS AND SHALL REMAIN THE PROPERTY OF CORDONIER ARCHITECTS. NO PART OF THIS DRAWING OR SPECIFICATION IS TO BE REPRODUCED OR TRANSMITTED IN ANY FORM OR BY ANY MEANS, ELECTRONIC OR MECHANICAL, INCLUDING PHOTOCOPYING, RECORDING, OR BY ANY INFORMATION STORAGE AND RETRIEVAL SYSTEM, WITHOUT THE WRITTEN PERMISSION OF CORDONIER ARCHITECTS.

THIS DRAWING IS THE PROPERTY OF CORDONIER ARCHITECTS.

DRAWING STATUS			
NO.	DATE	BY	APPROVED BY
1	11/03/14	AT	PN
2			
3			
4			
5			
6			
7			
8			
9			
10			

BASED ON DRAWING A1/01, A1/02 AND A1/03 DATED NOV 2012 FROM TAYLOR STANCO ARCHITECTS

NB: To be read in conjunction with H2O spec

MR & MRS HUDSON

CORDONIER
 Chartered Architects
 18 Long Lane
 Sheffield
 S11 1TQ
 Tel: +44 (0)114 262 1555
 Fax: +44 (0)114 262 1555
 www.cordonier.co.uk

PROJECT TITLE
 GREAT GILLING
 11 CHORLEY ROAD, S10 3RJ

DRAWING TITLE
 PROPOSED BATHROOM FINISHES

NO.	DATE	BY	APPROVED BY
14.02	04/02	X	