


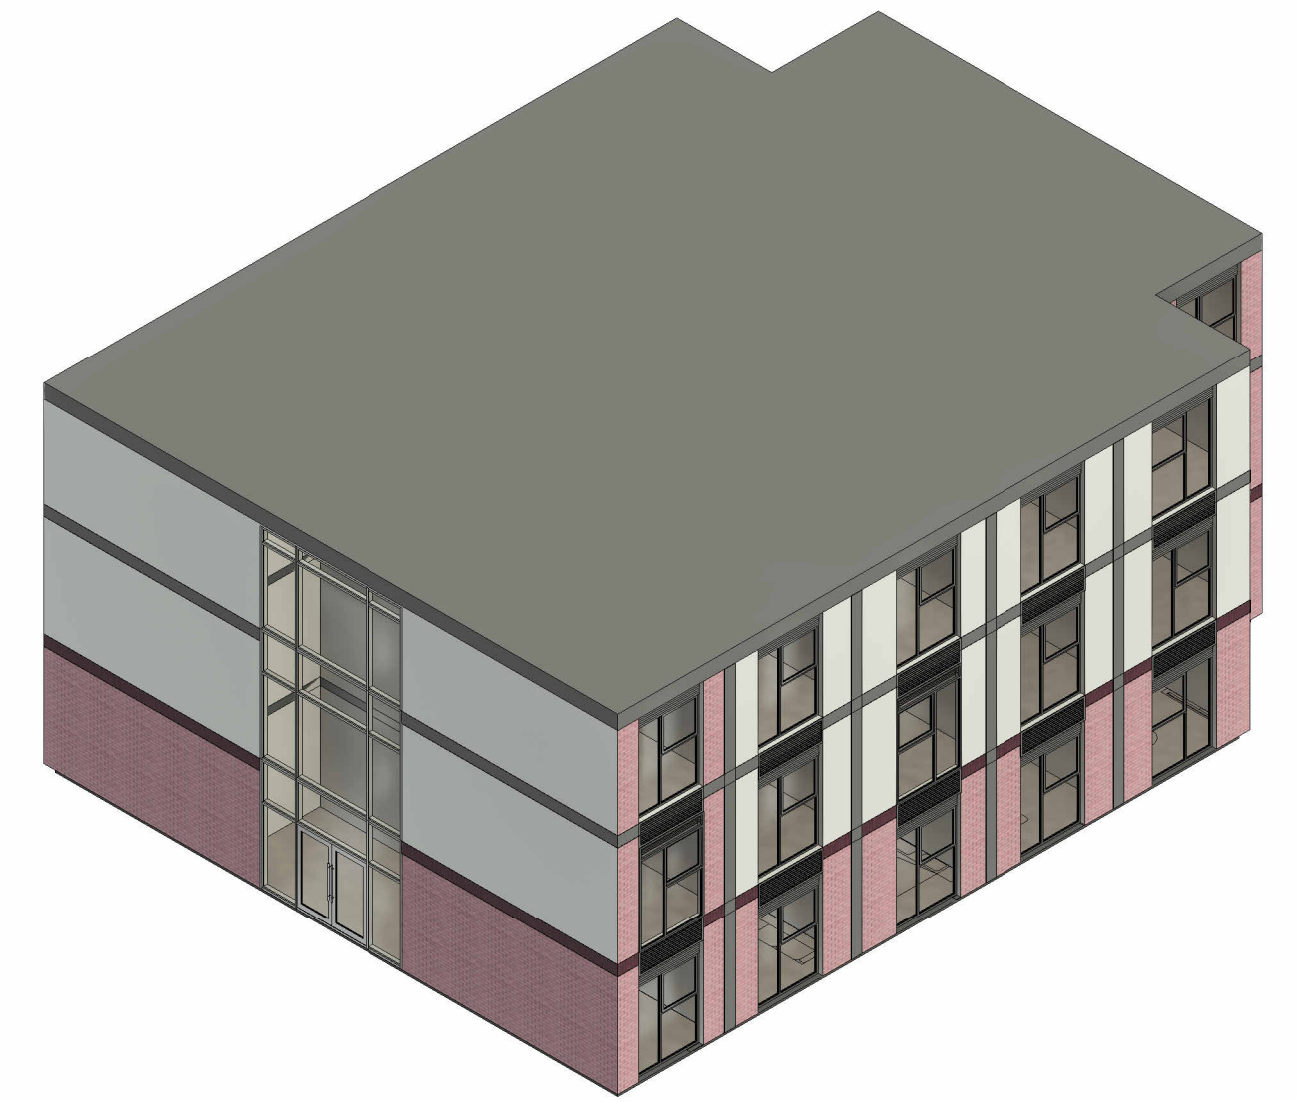
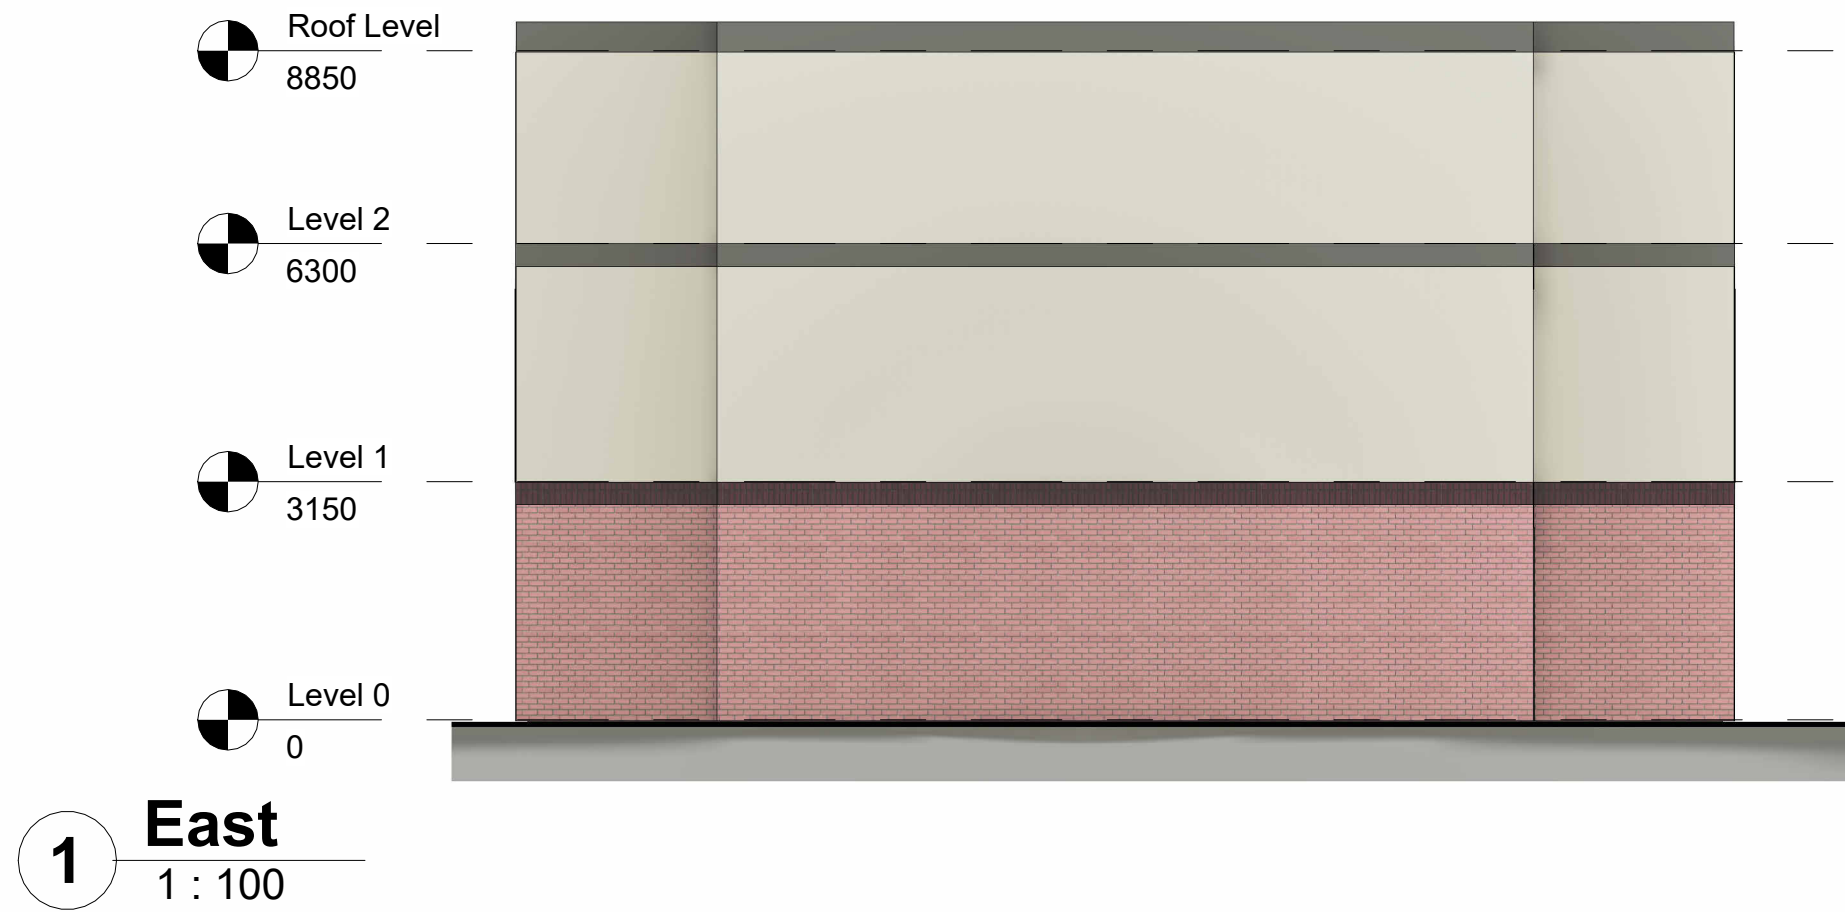


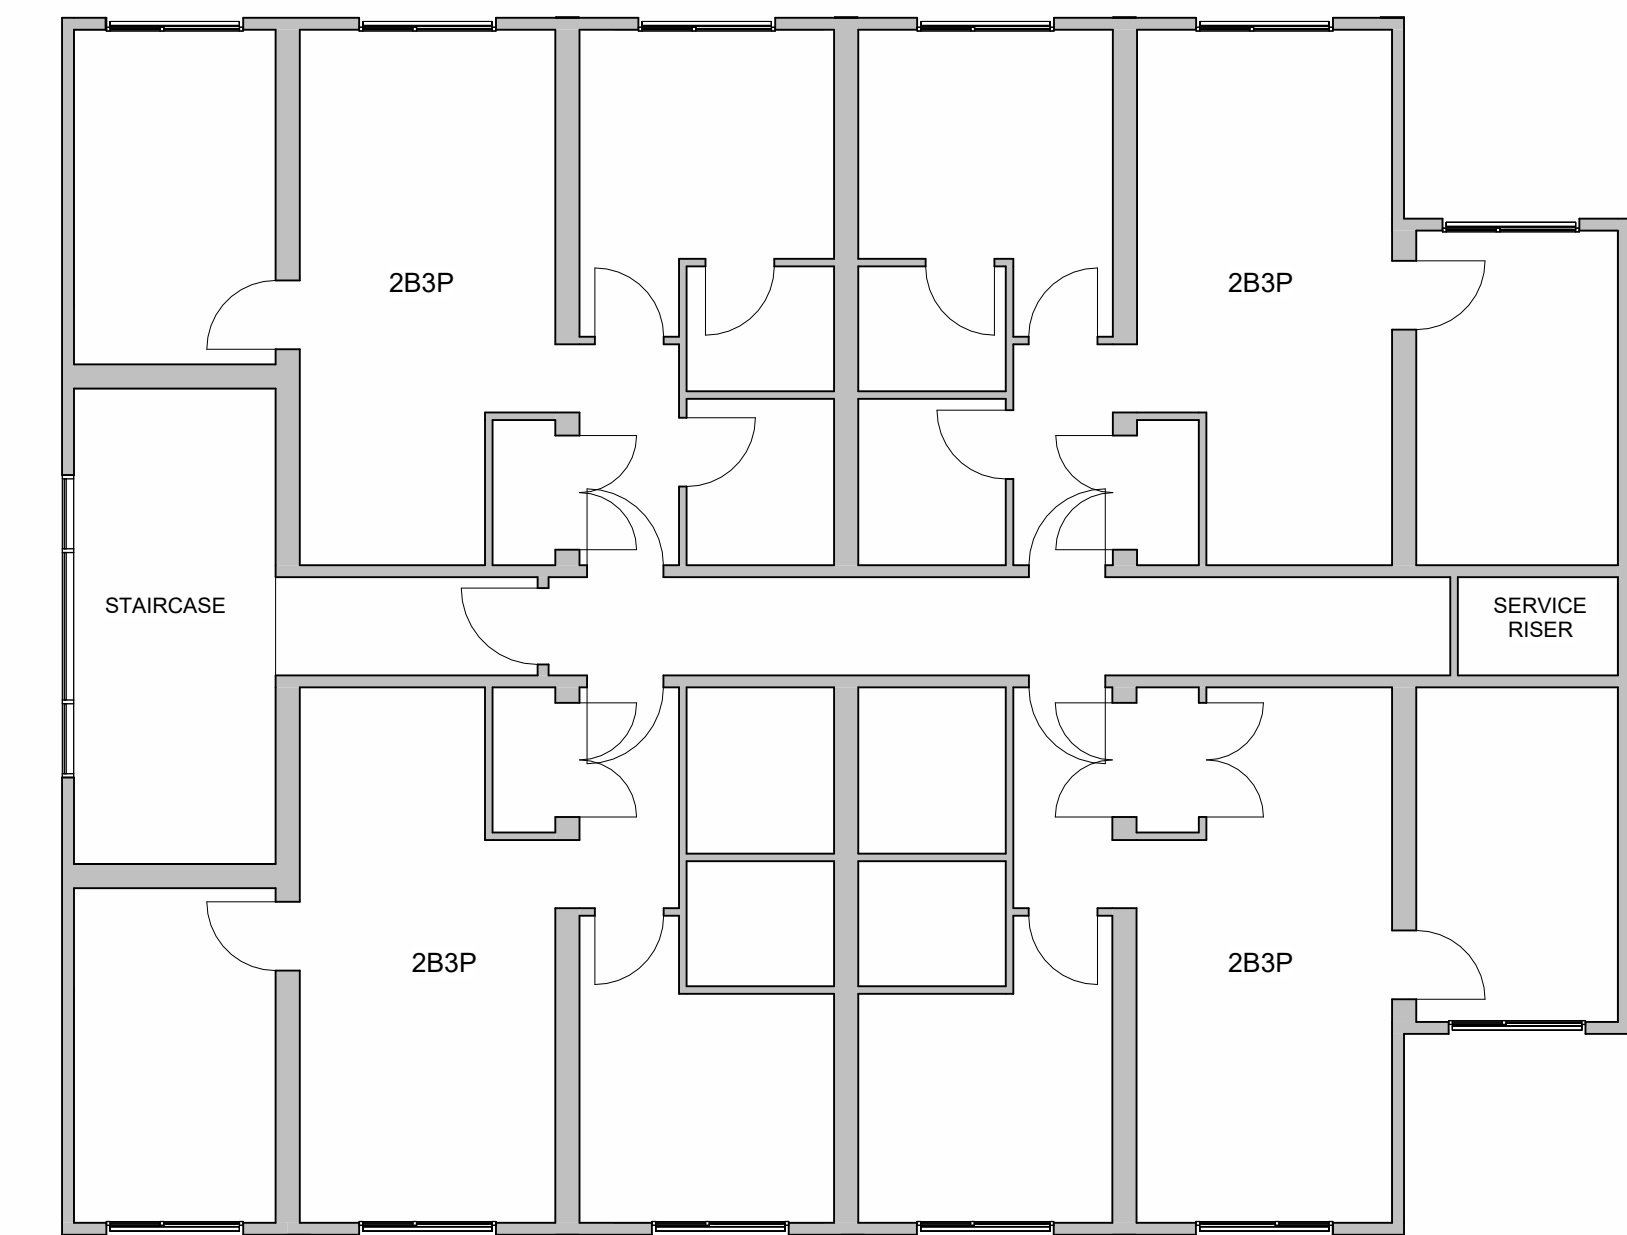

8 ISOMETRIC VIEW

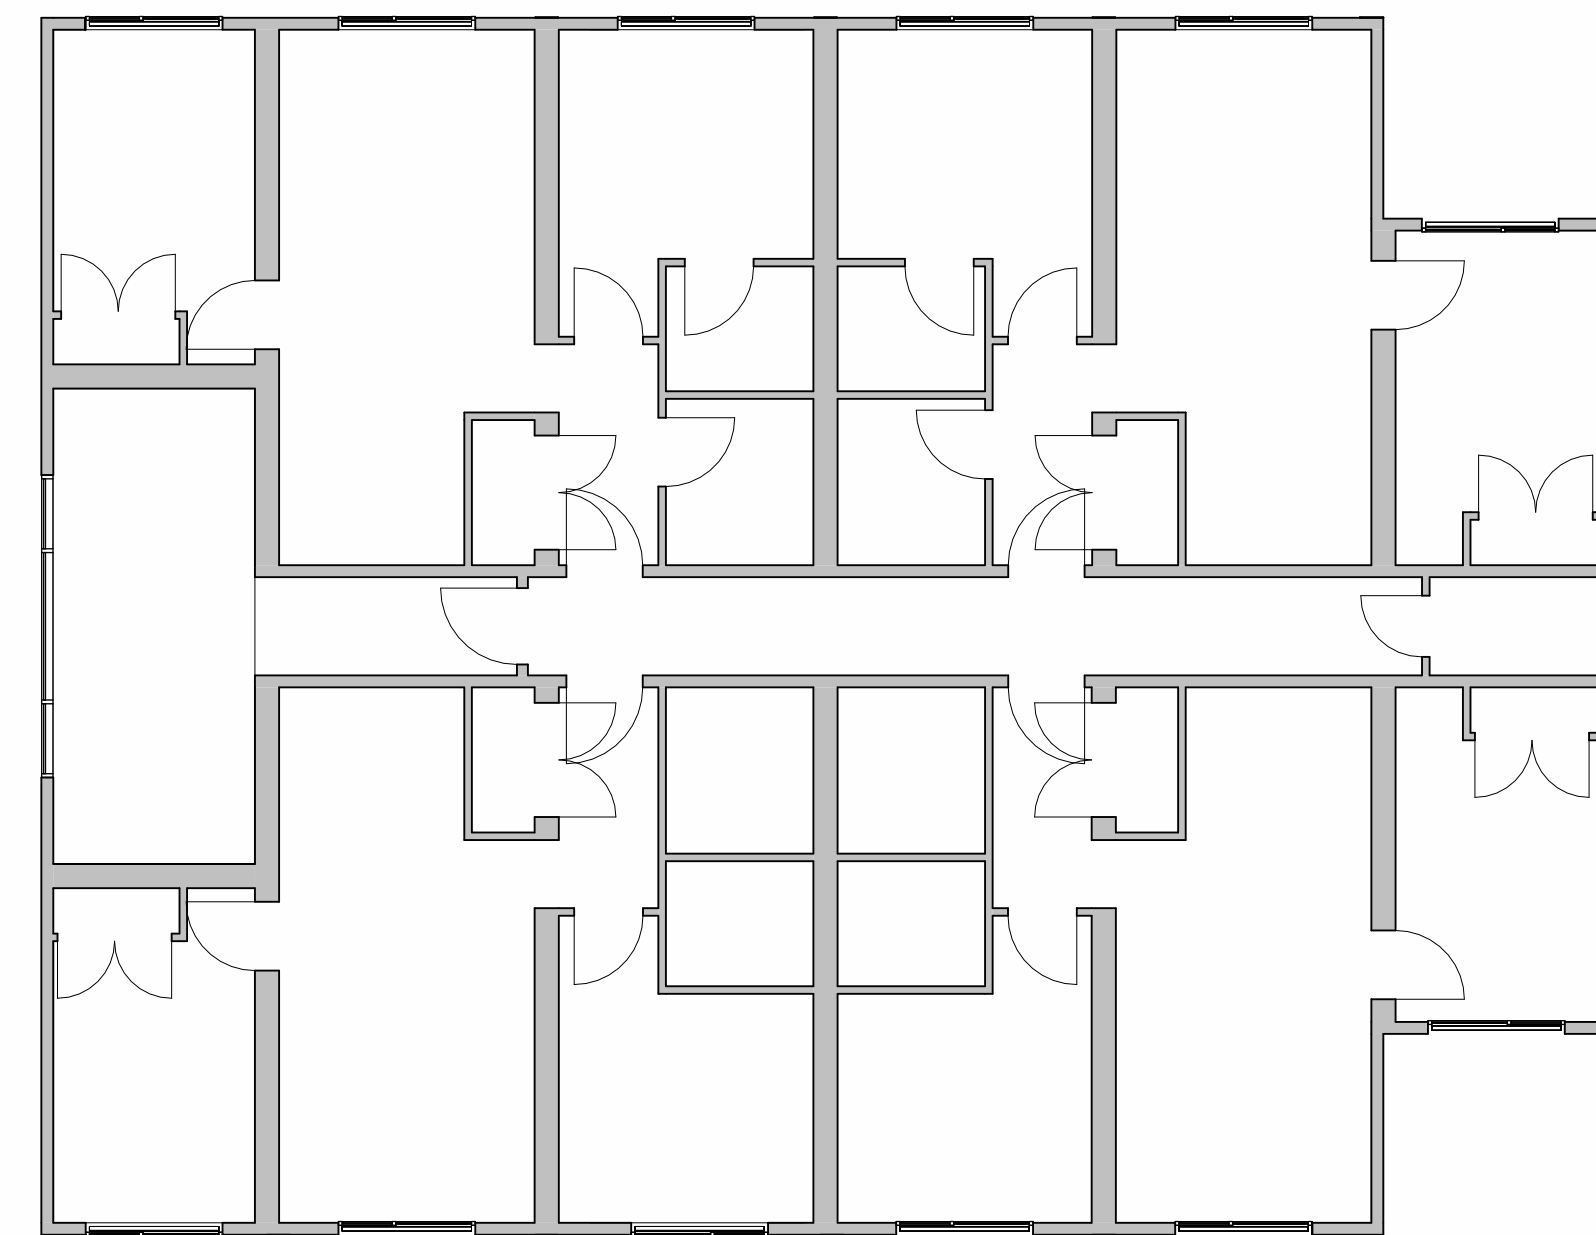

9 RENDER 1:1

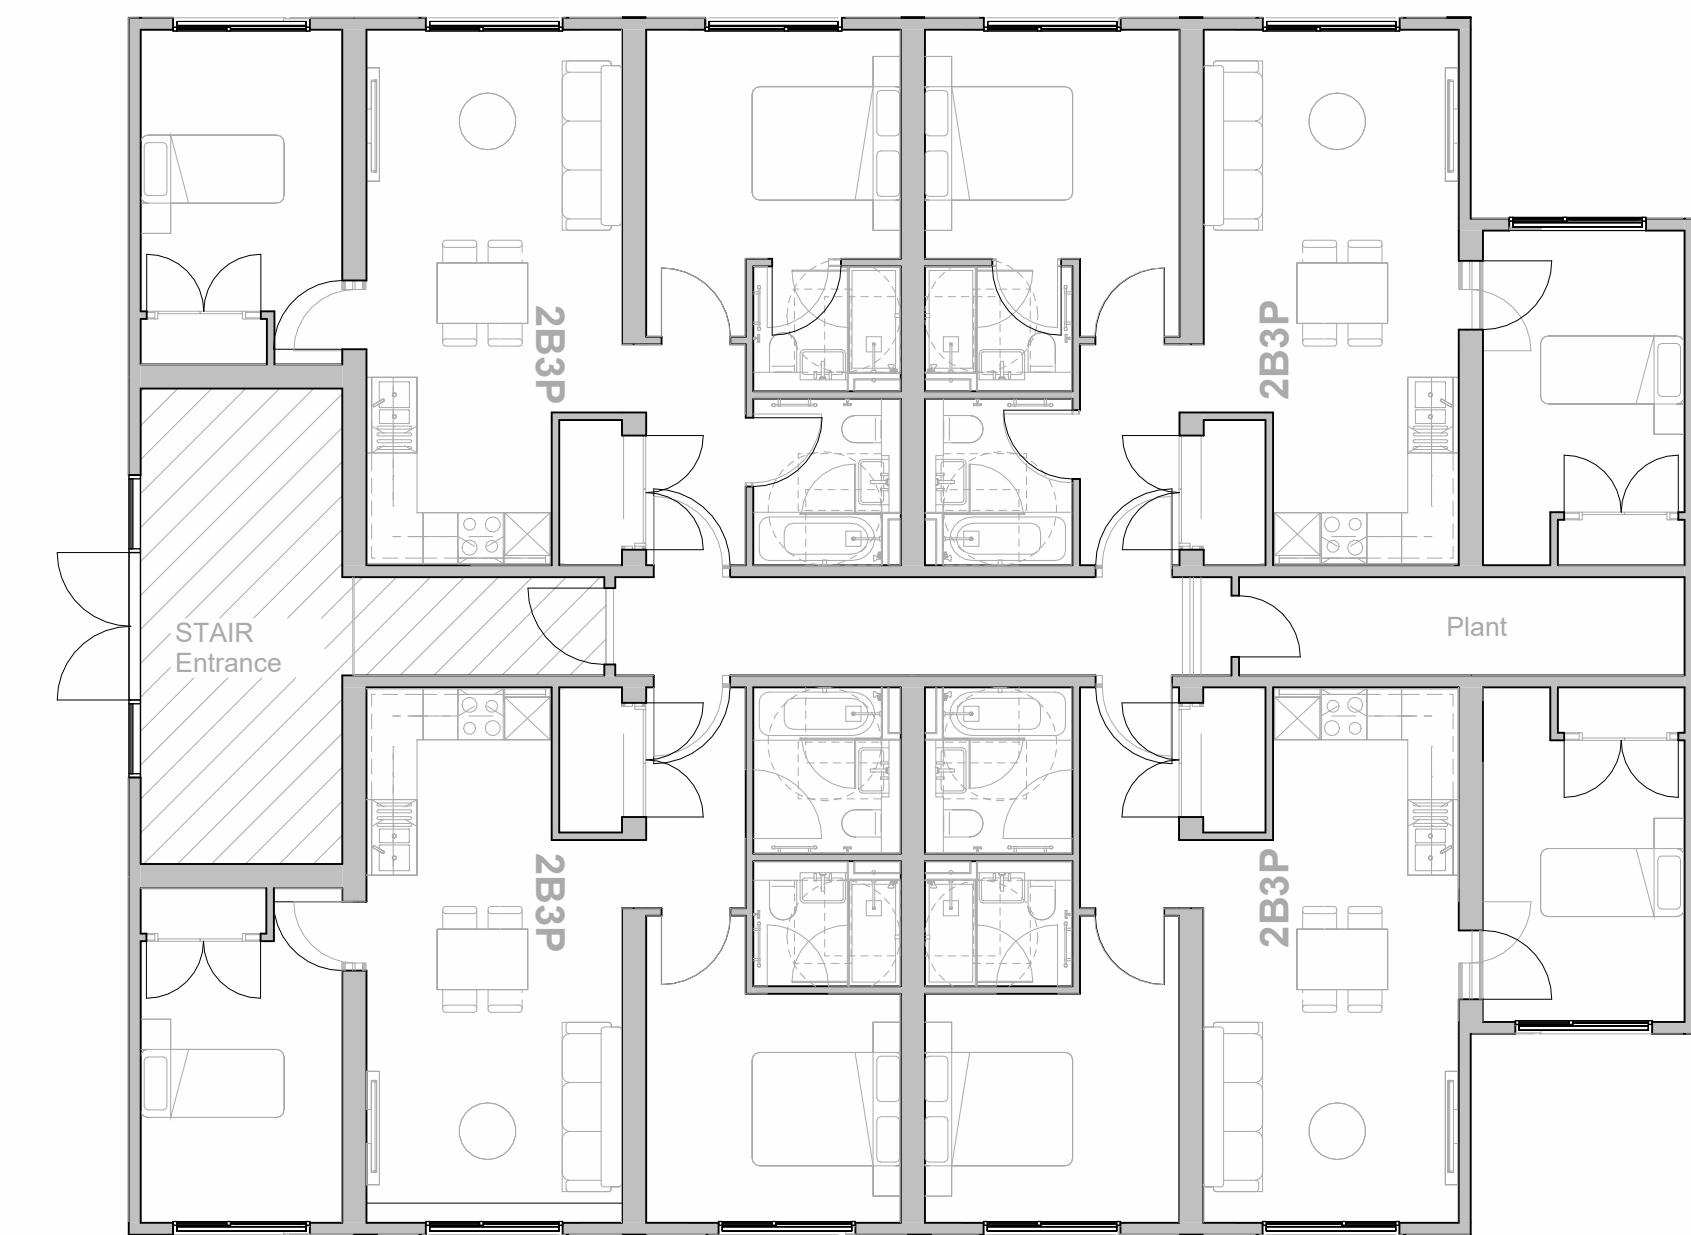

Rev	Date	Description	By	Chk
-----	------	-------------	----	-----



NEWARK

Carlton Works, Ossington Road, Newark, NG23 6NT
Tel: 01636 821 645 www.jrlgroup.co.uk

CLIENT

PROJECT

Project Name
Enter address here

TITLE

Unnamed

CREATION

DATE

01/23/20

JRL CALENDAR NO.

01/23/20

PROJECT NO

01/23/20

REVISION

01/23/20

01/23/20


01/23/20

01/23/20

01/23/20


01/23/20

01/23/20

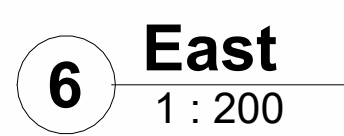


OPTION 1


DO NOT SCALE OFF DISBURSING. USE DISBURSED DISBURSING.

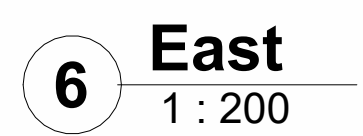

Rev	Date	Description	By	Check
OPTION 2				
				
NEWARK				
Carlton Works, Ossington Road, Newark, NG23 6NT Tel: 01636 821 645 www.jrlgroup.co.uk				
CLIENT _____ _____				
PROJECT _____ Project Name Enter address here				
TITLE _____ Unnamed				
CREATION DATE 12/1/03	SCALE As indicated	DR PN	CH SC	STATUS S
JRL CALSWOOD.MXD				
PROJECT NO: 0030GINATORZONELEVELTYPE: ROLNUMBER				
CIRCLE NO.				REVISION
DISCLAIMER: ALL RIGHTS RESERVED. THIS DRAWING MUST BE READ IN CONNECTION WITH ALL OTHER RELEVANT DRAWINGS AND INFORMATION. ANY DISCREPANCIES MUST BE REPORTED TO JRL CALSWOOD IMMEDIATELY. THIS DRAWING IS INFORMATION MUST NOT BE USED FOR CONSTRUCTION UNLESS EXPRESSLY INDICATED. DO NOT SCALE OFF DRAWINGS. USE DISPLAYED DIMENSIONS.				

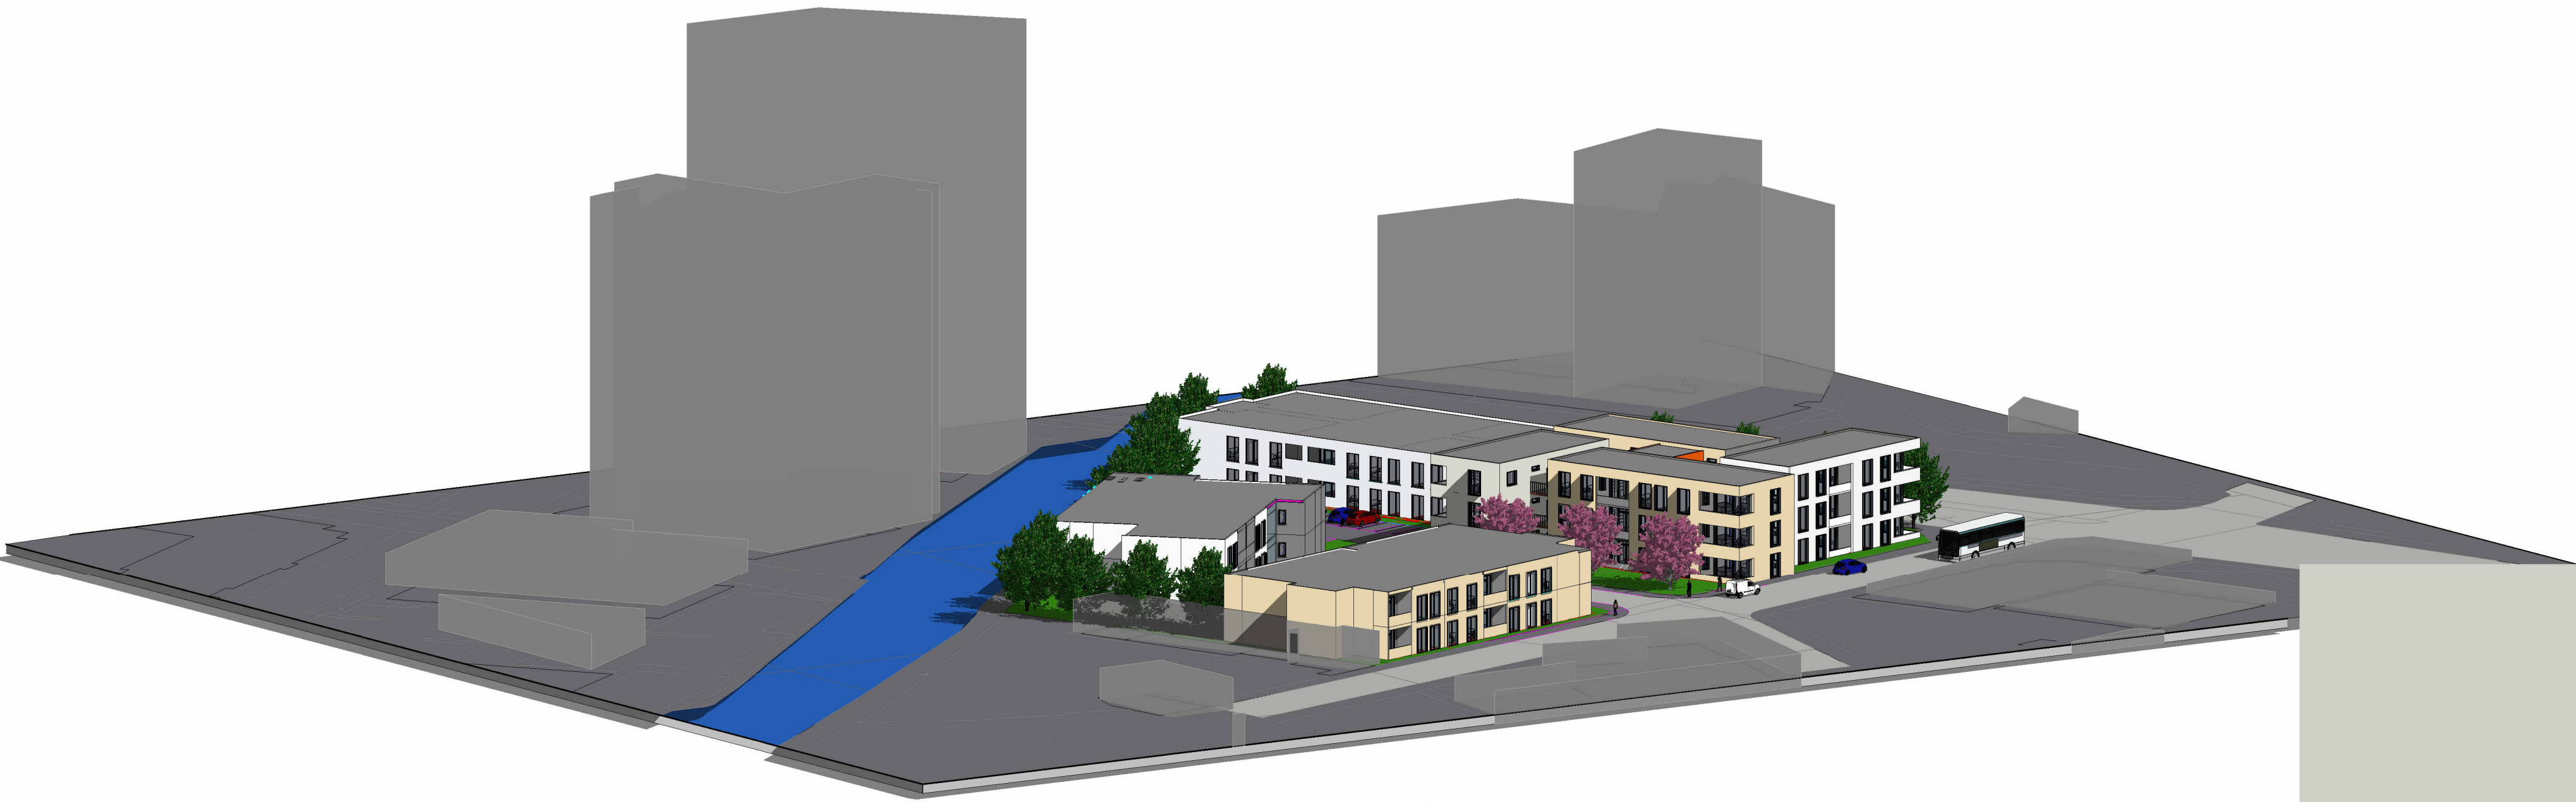

VIEW 3

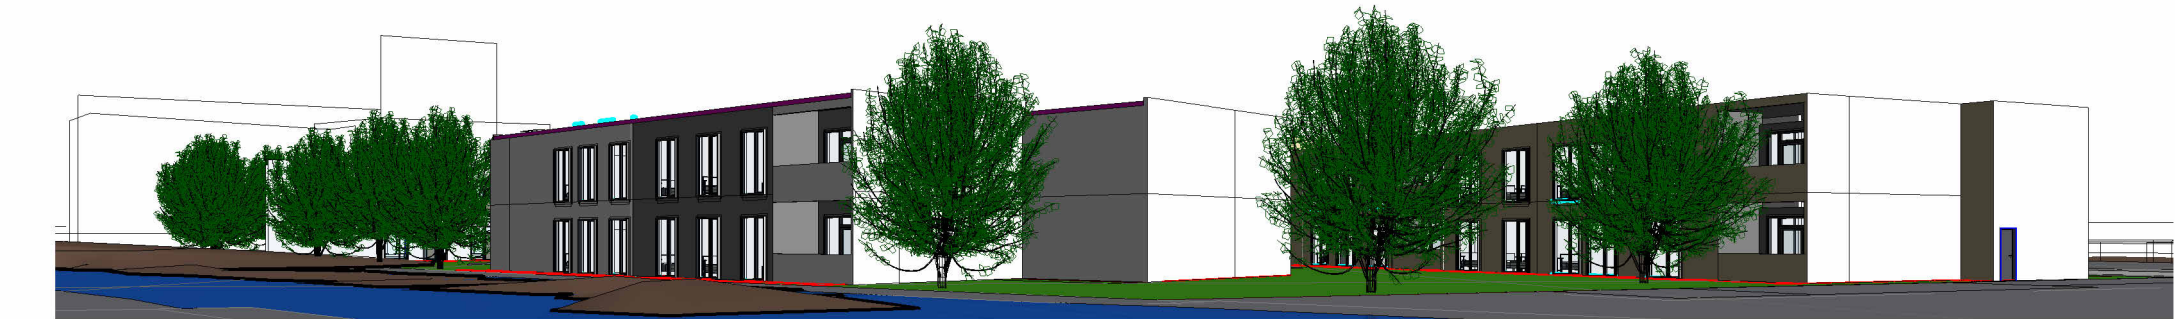

VIEW 4




VIEW 2

E1		
BEDROOMS	N0.	LEVEL
3B	6	GF/1F
2B	6	GF/1F

E2		
3B	6	GF/1F
2B	4	GF/1F

E3		
3B	8	GF/1F
2B	4	GF/1F

H1		
BEDROOMS	N0.	LEVEL
3B	6	GF/1F/2F
2B	12	GF/1F/2F
1B	6	GF/1F/2F

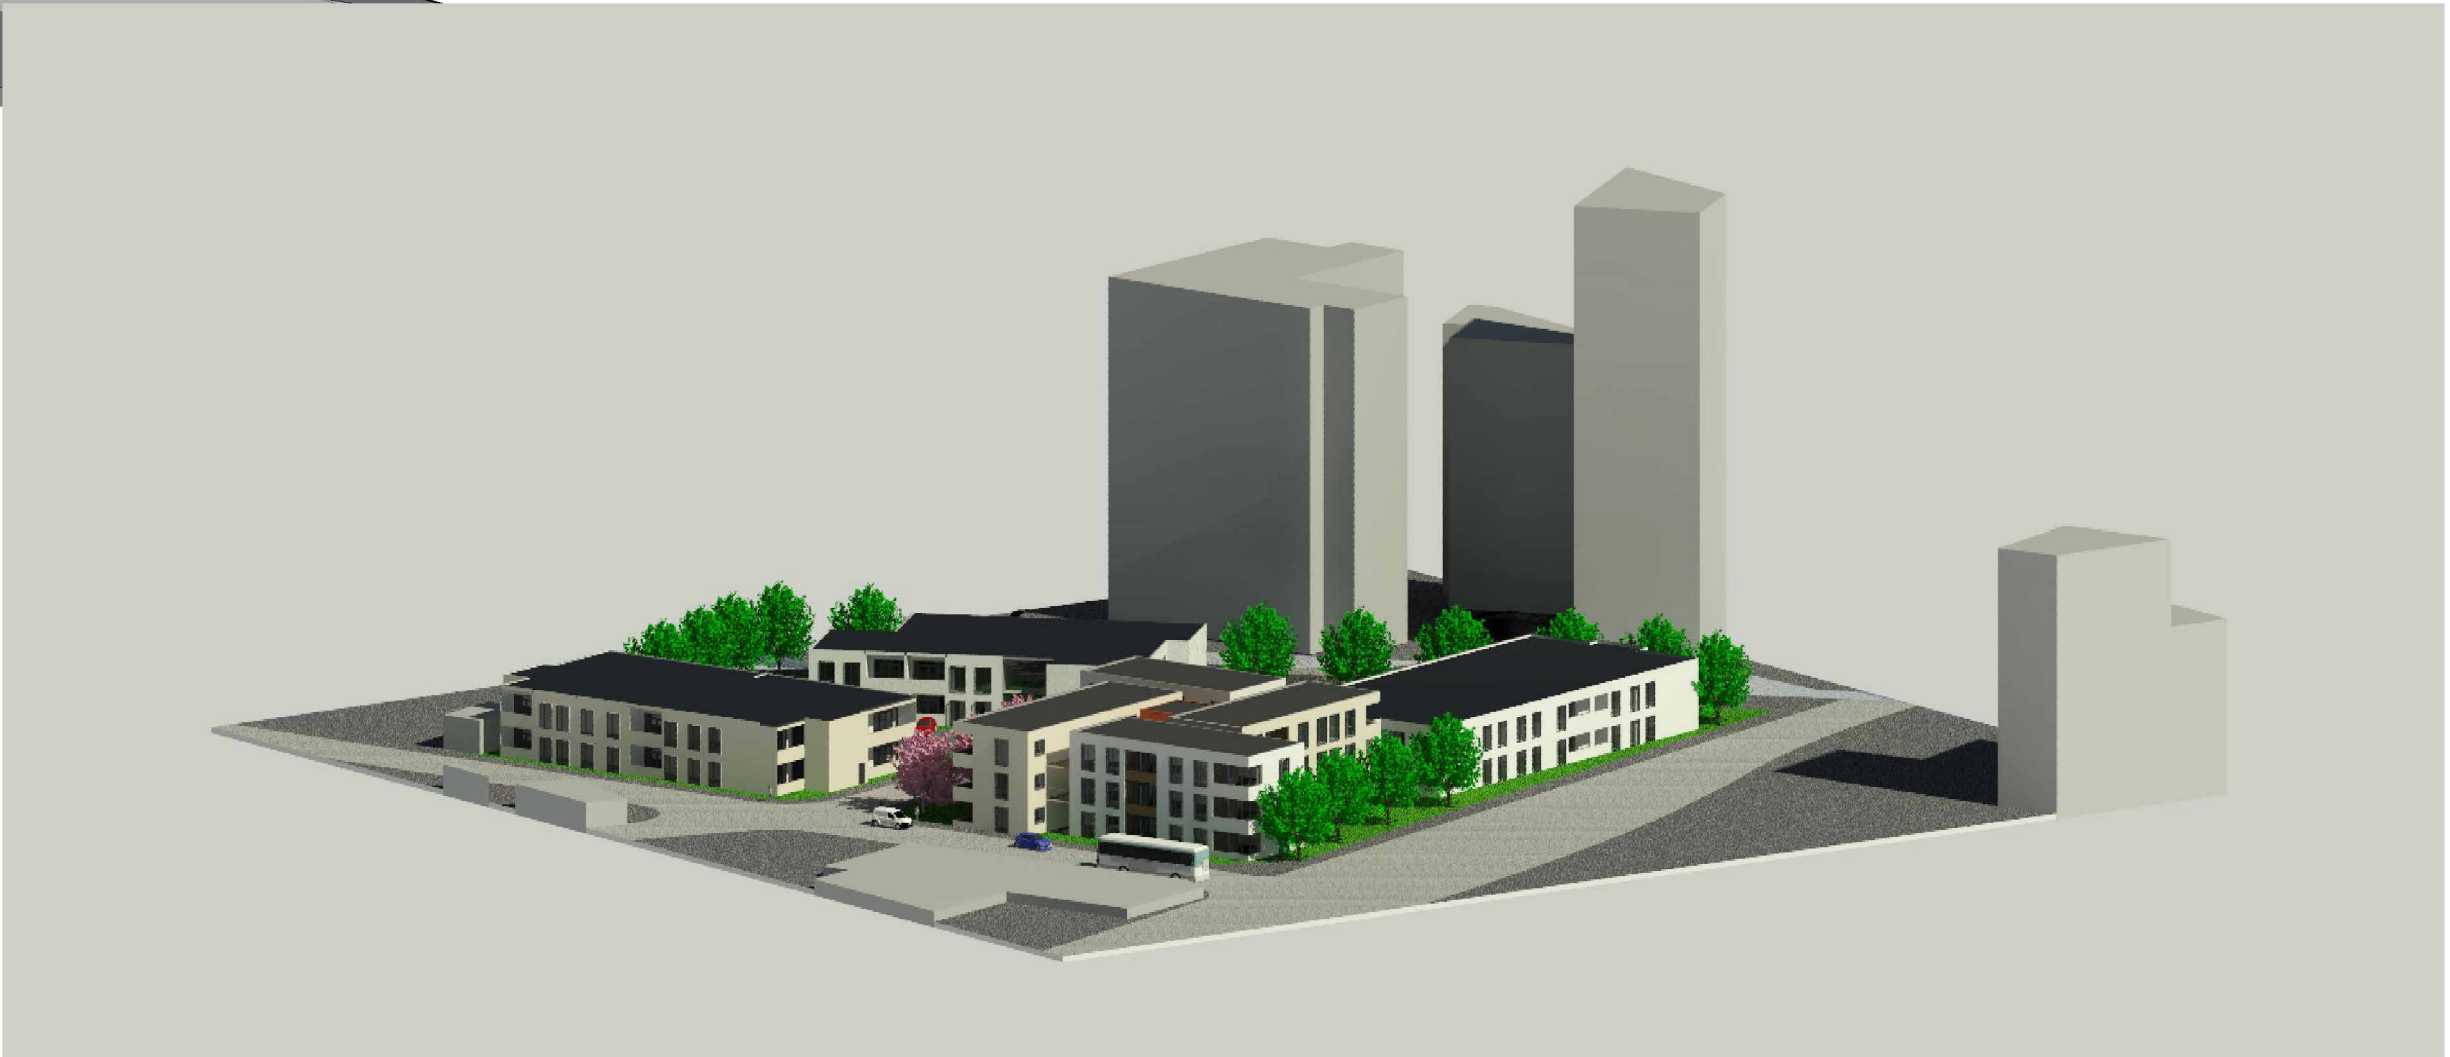

VIEW 1



SITE PLAN
1 : 500

Rev

Date

Description

By

Chk

DRAFT

JRL

MODULAR

LIMITED

NEWARK

Carlton Works, Ossington Road, Newark, NG23 6NT
Tel: 01636 821 645 www.jrlgroup.co.uk

CLIENT

PROJECT

BREWERY STREET RESIDENTIAL BLOCK

TITLE

Unnamed

CREATION

DATE

01/23/2017

SCALE @ A1

As Indicated

OR

Author

CH

Checker

STATUS

JRL CALENDAR NO.

PROJECT NO

ORIGINATOR

ZONE

LEVEL

TYPE

POLE

NUMBER

CHGK NO.

REVISION


© COPYRIGHT - ALL RIGHTS RESERVED.

THIS DRAWING MUST BE READ IN CONNECTION WITH ALL OTHER RELEVANT DRAWINGS AND INFORMATION.


ANY DISCREPANCIES MUST BE REPORTED TO JRL CALENDAR IMMEDIATELY.

THIS DRAWING IS FOR INFORMATION ONLY AND MUST NOT BE USED FOR CONSTRUCTION UNLESS EXPRESSLY DRAWN FOR CONSTRUCTION.

DO NOT SCALE OFF DRAWINGS. USE DISPLAYED DIMENSIONS.

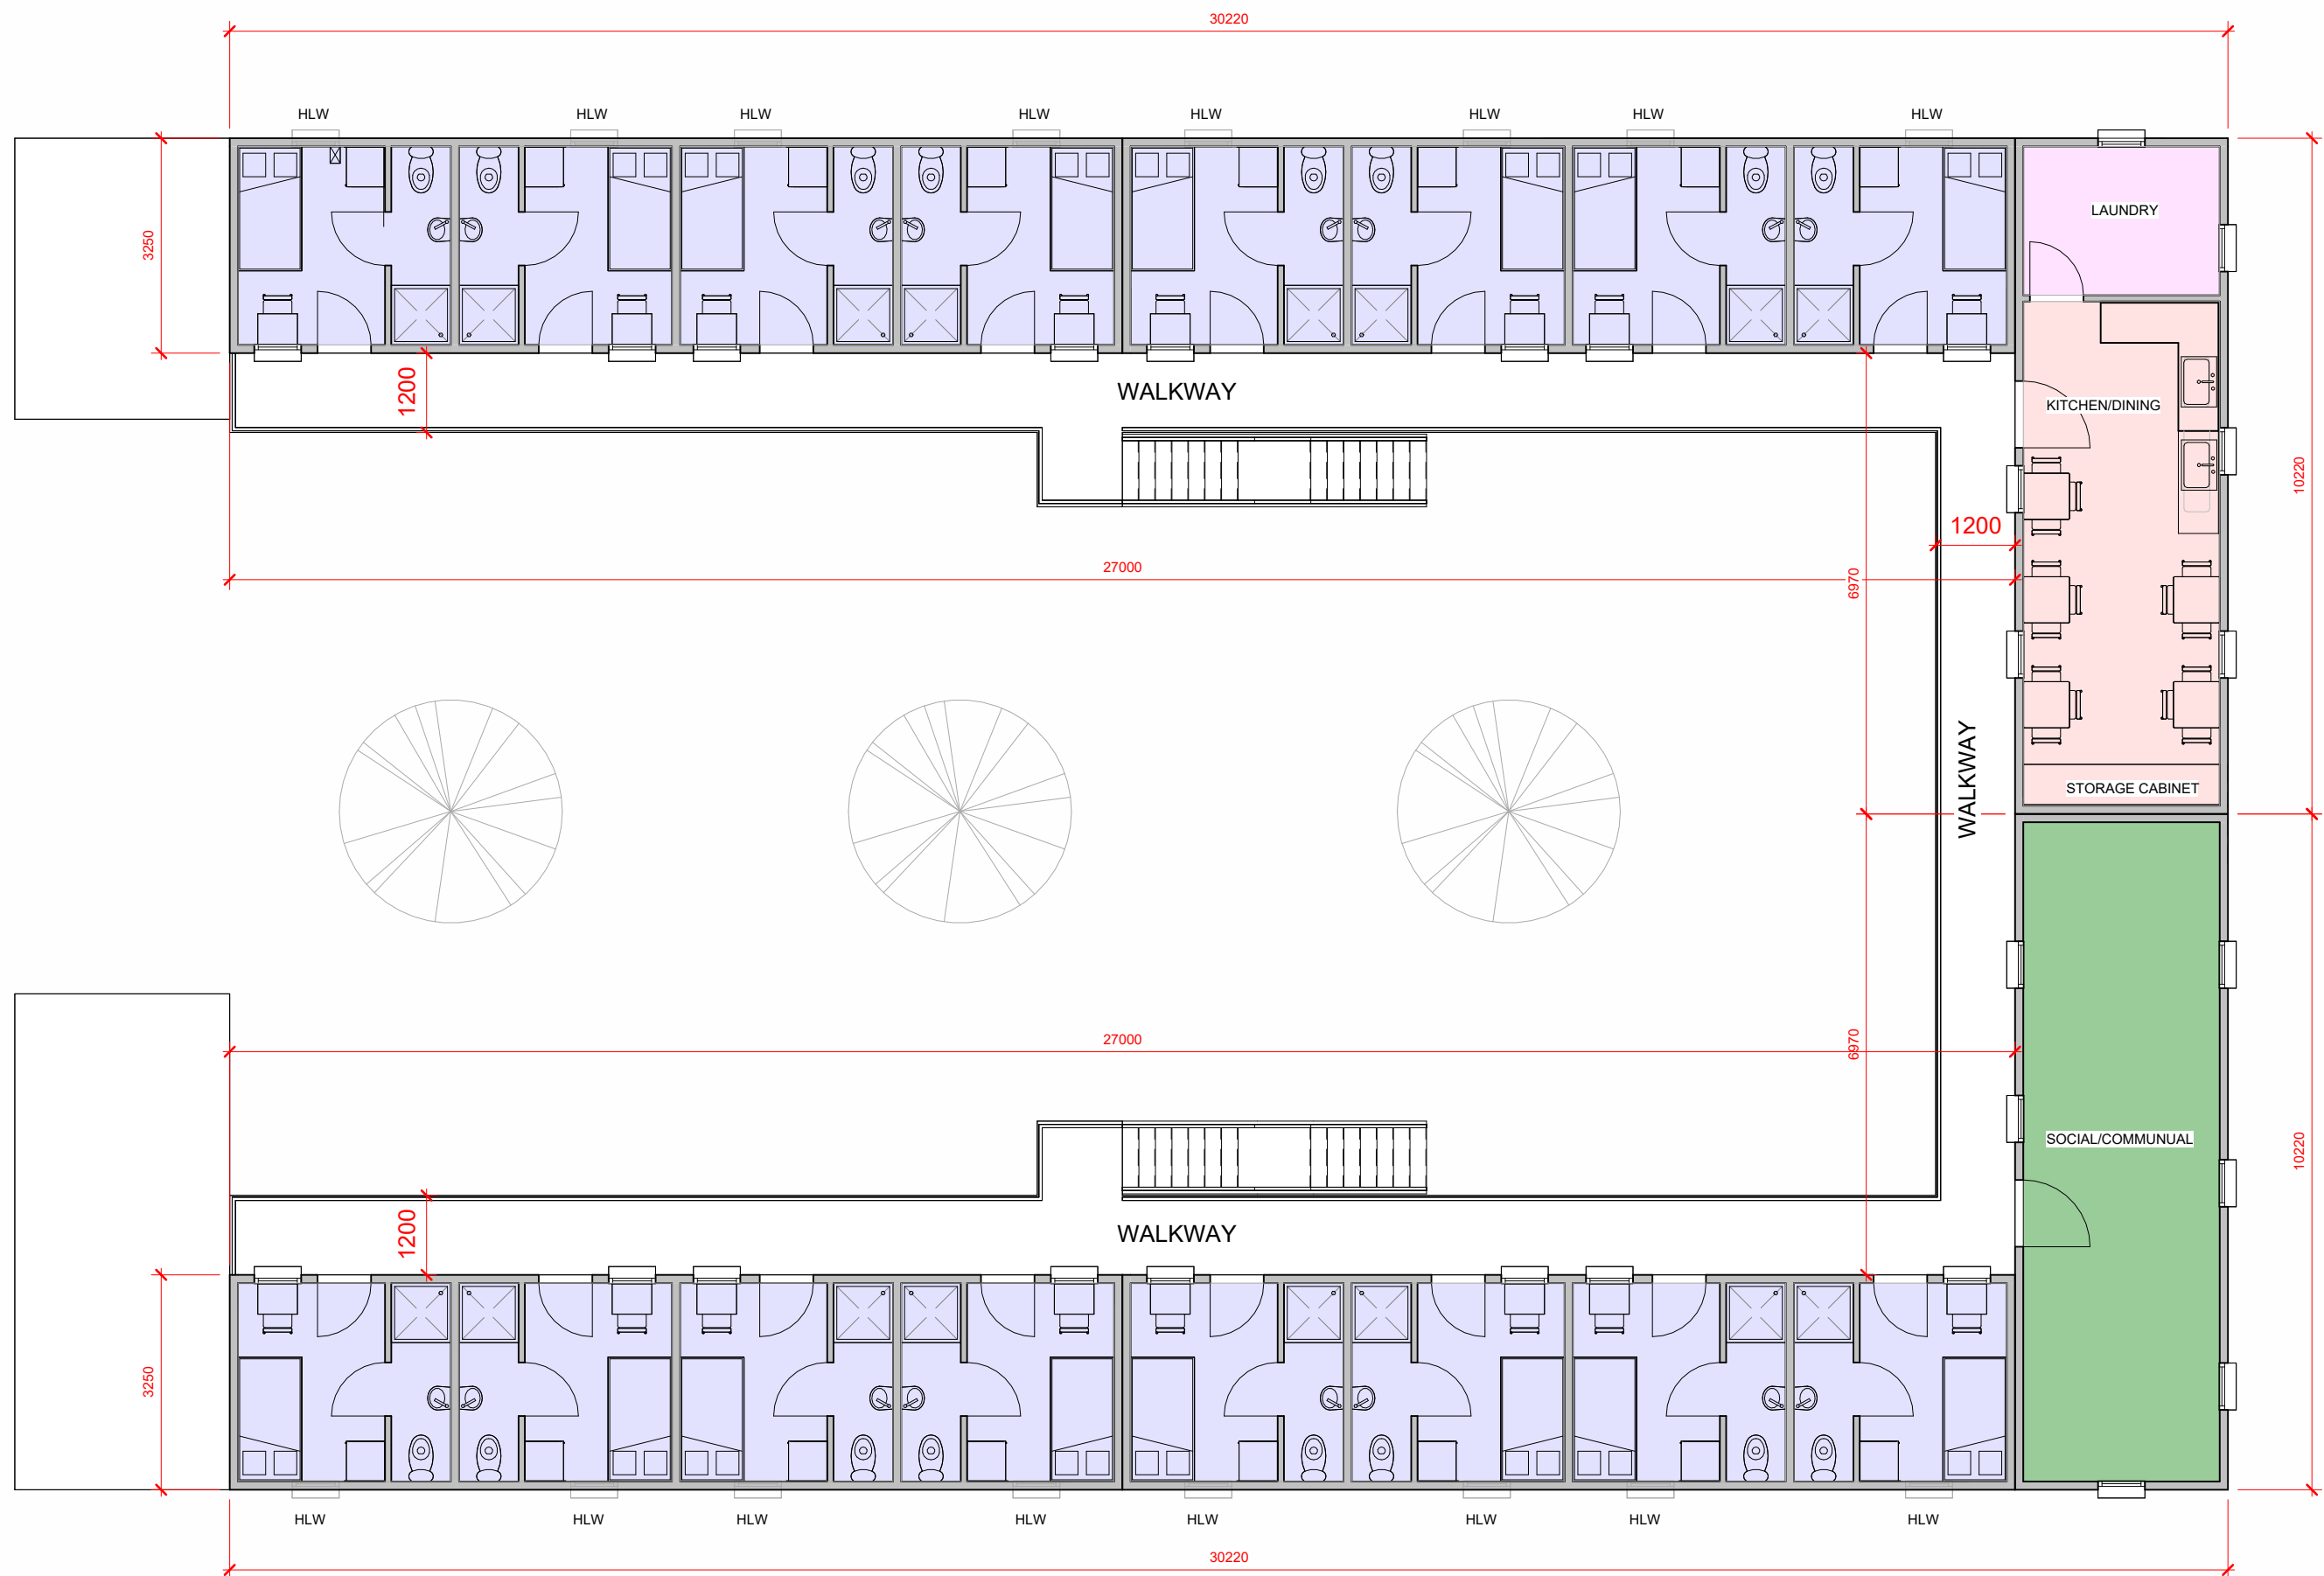

FIRST FLOOR PLAN
1 : 100

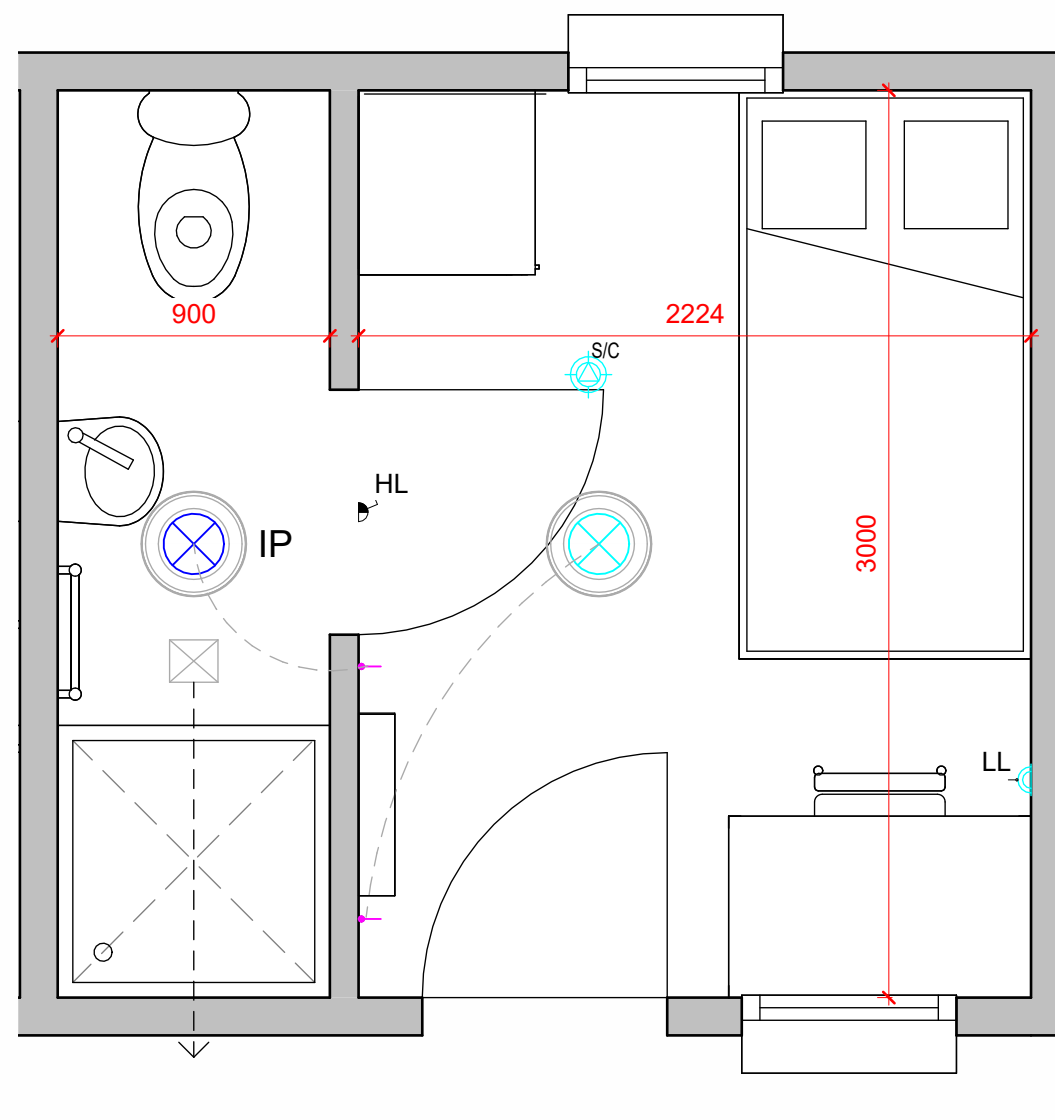


TYPICAL BEDROOM LAYOUT
1 : 25

- EXTRACT FAN
- IP65 LIGHT
- STANDARD LIGHT
- LIGHT SWITCH
- TWIN SWITCH SOCKETS
- SPUR
- SMOKE AND CARBOR MONOXIDE DETECTOR
- ELECTRIC RADIATOR
- TOWEL RAIL
- LL LOW LEVEL
- HL HIGH LEVEL
- SINGLE ROOM
- ACCESSIBLE ROOM
- DOUBLE ROOM (FAMILY)
- KITCHEN / DINING
- LAUNDRY
- SOCIAL / COMMUNAL
- CONSULTING
- WC/SHOWER/LOBBY
- SECURITY
- PLANT ROOM



TYPICAL BEDROOM LAYOUT

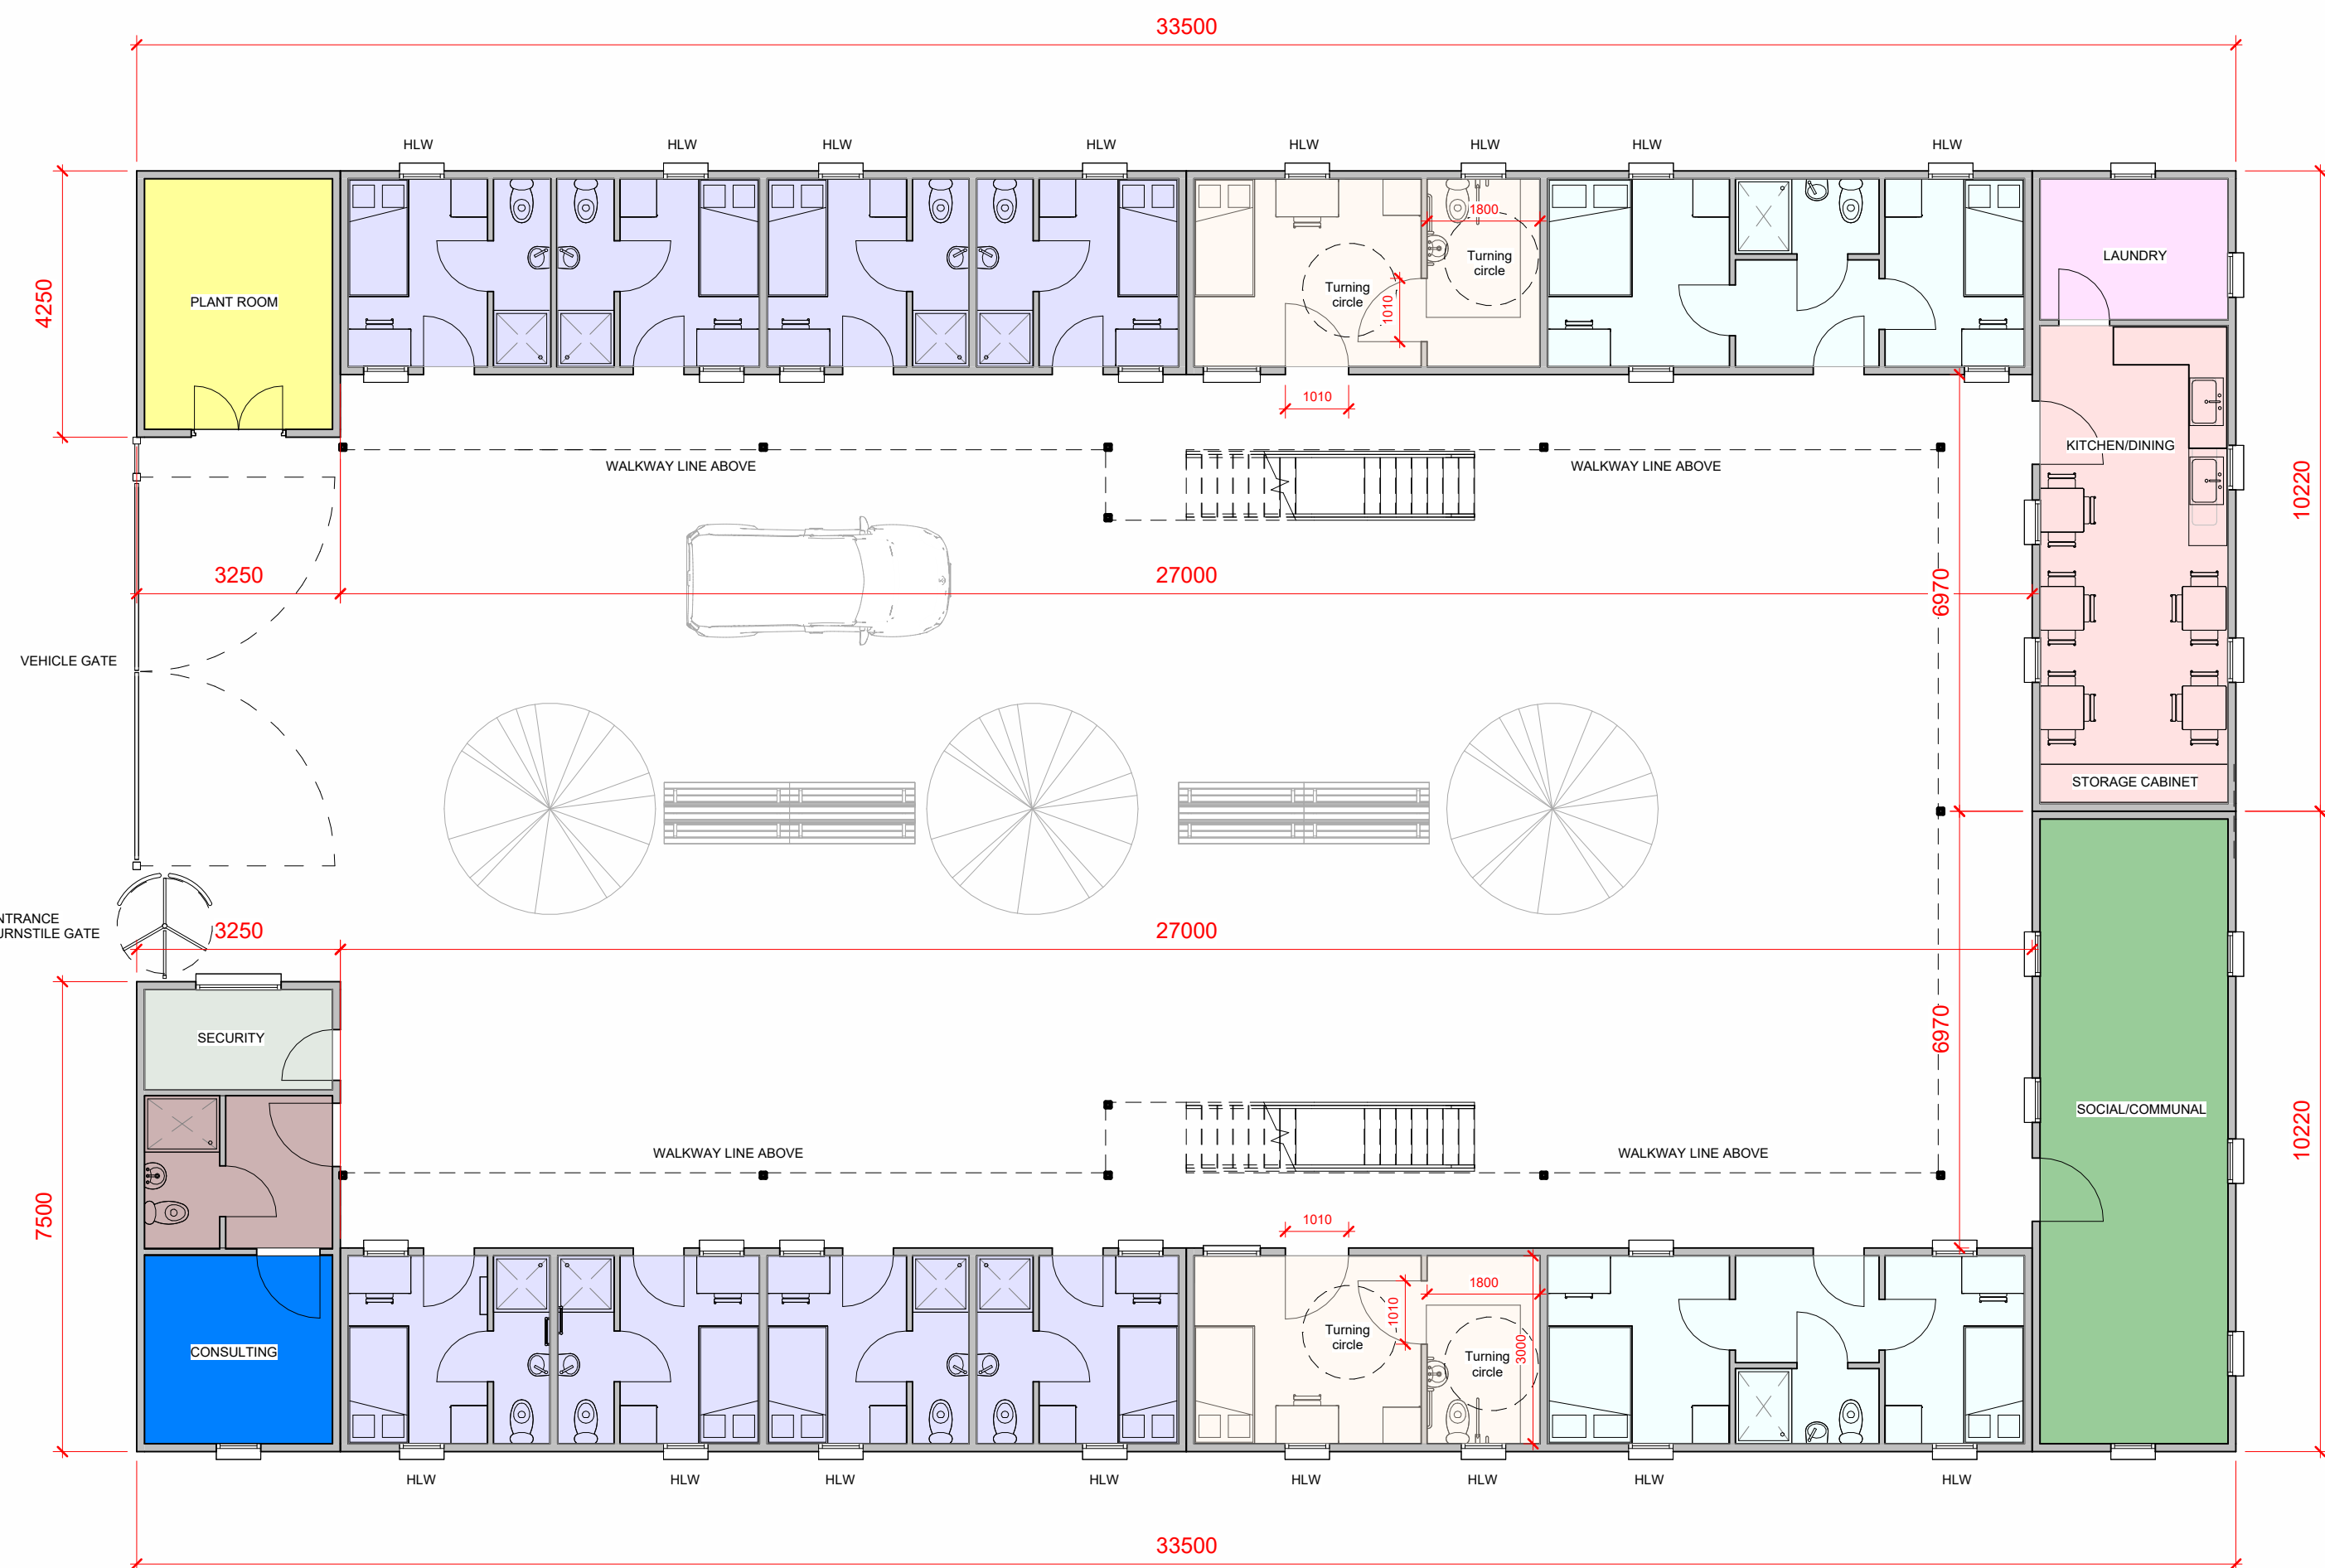

GROUND FLOOR PLAN
1 : 100




ISOMETRIC VIEW

Safety, Health & Environmental Information
The following hazards/residual risk associated with the work detailed on this drawing have not been eliminated during design. These are highlighted in addition to risks that a competent contractor undertaking this work should be aware of and including within their safe systems of work.


CONSTRUCTION
There is no residual risks that a competent contractor would not otherwise be aware of by looking at the drawing.

Notes: All dimensions are in millimeters (mm) otherwise noted.
This drawing and any information or descriptive matter set herein are the confidential and copyright property of JRL Caledonian Modular Ltd. and must not be disclosed, loaned, copied or used for manufacturing, tendering or any other purpose without the prior consent in writing from JRL Caledonian Modular Ltd.

Rev	Date	Description	By	Chk
CONCEPT				
JRL MODULAR LIMITED				
NEWARK				
Carlton Works, Ossington Road, Newark, NG23 6NT				
Tel: 01636 821 645 www.jrlgroup.co.uk				
CLIENT				
PROJECT				
Project Name				
Enter address here				
TITLE				
Unnamed				
CREATION	DATE	SCALE @ A1	OR	STATUS
01/23/2023	As Indicated	Author	CH	Checker
JRL CALEDONIAN NO.				
PROJECT NO/DIGITIZER/ZONE/LEVEL/TYPE/ROLE/NUMBER				
CHG. NO.				
REVISION				
© COPYRIGHT. ALL RIGHTS RESERVED.				
THIS DRAWING MUST BE USED IN CONNECTION WITH ALL OTHER RELEVANT DRAWINGS AND INFORMATION.				
ANY DISCREPANCIES MUST BE REPORTED TO JRL CALEDONIAN IMMEDIATELY.				
FOR CONSTRUCTION.				
DO NOT SCALE OFF DRAWINGS. USE DISPLAYED DIMENSIONS.				

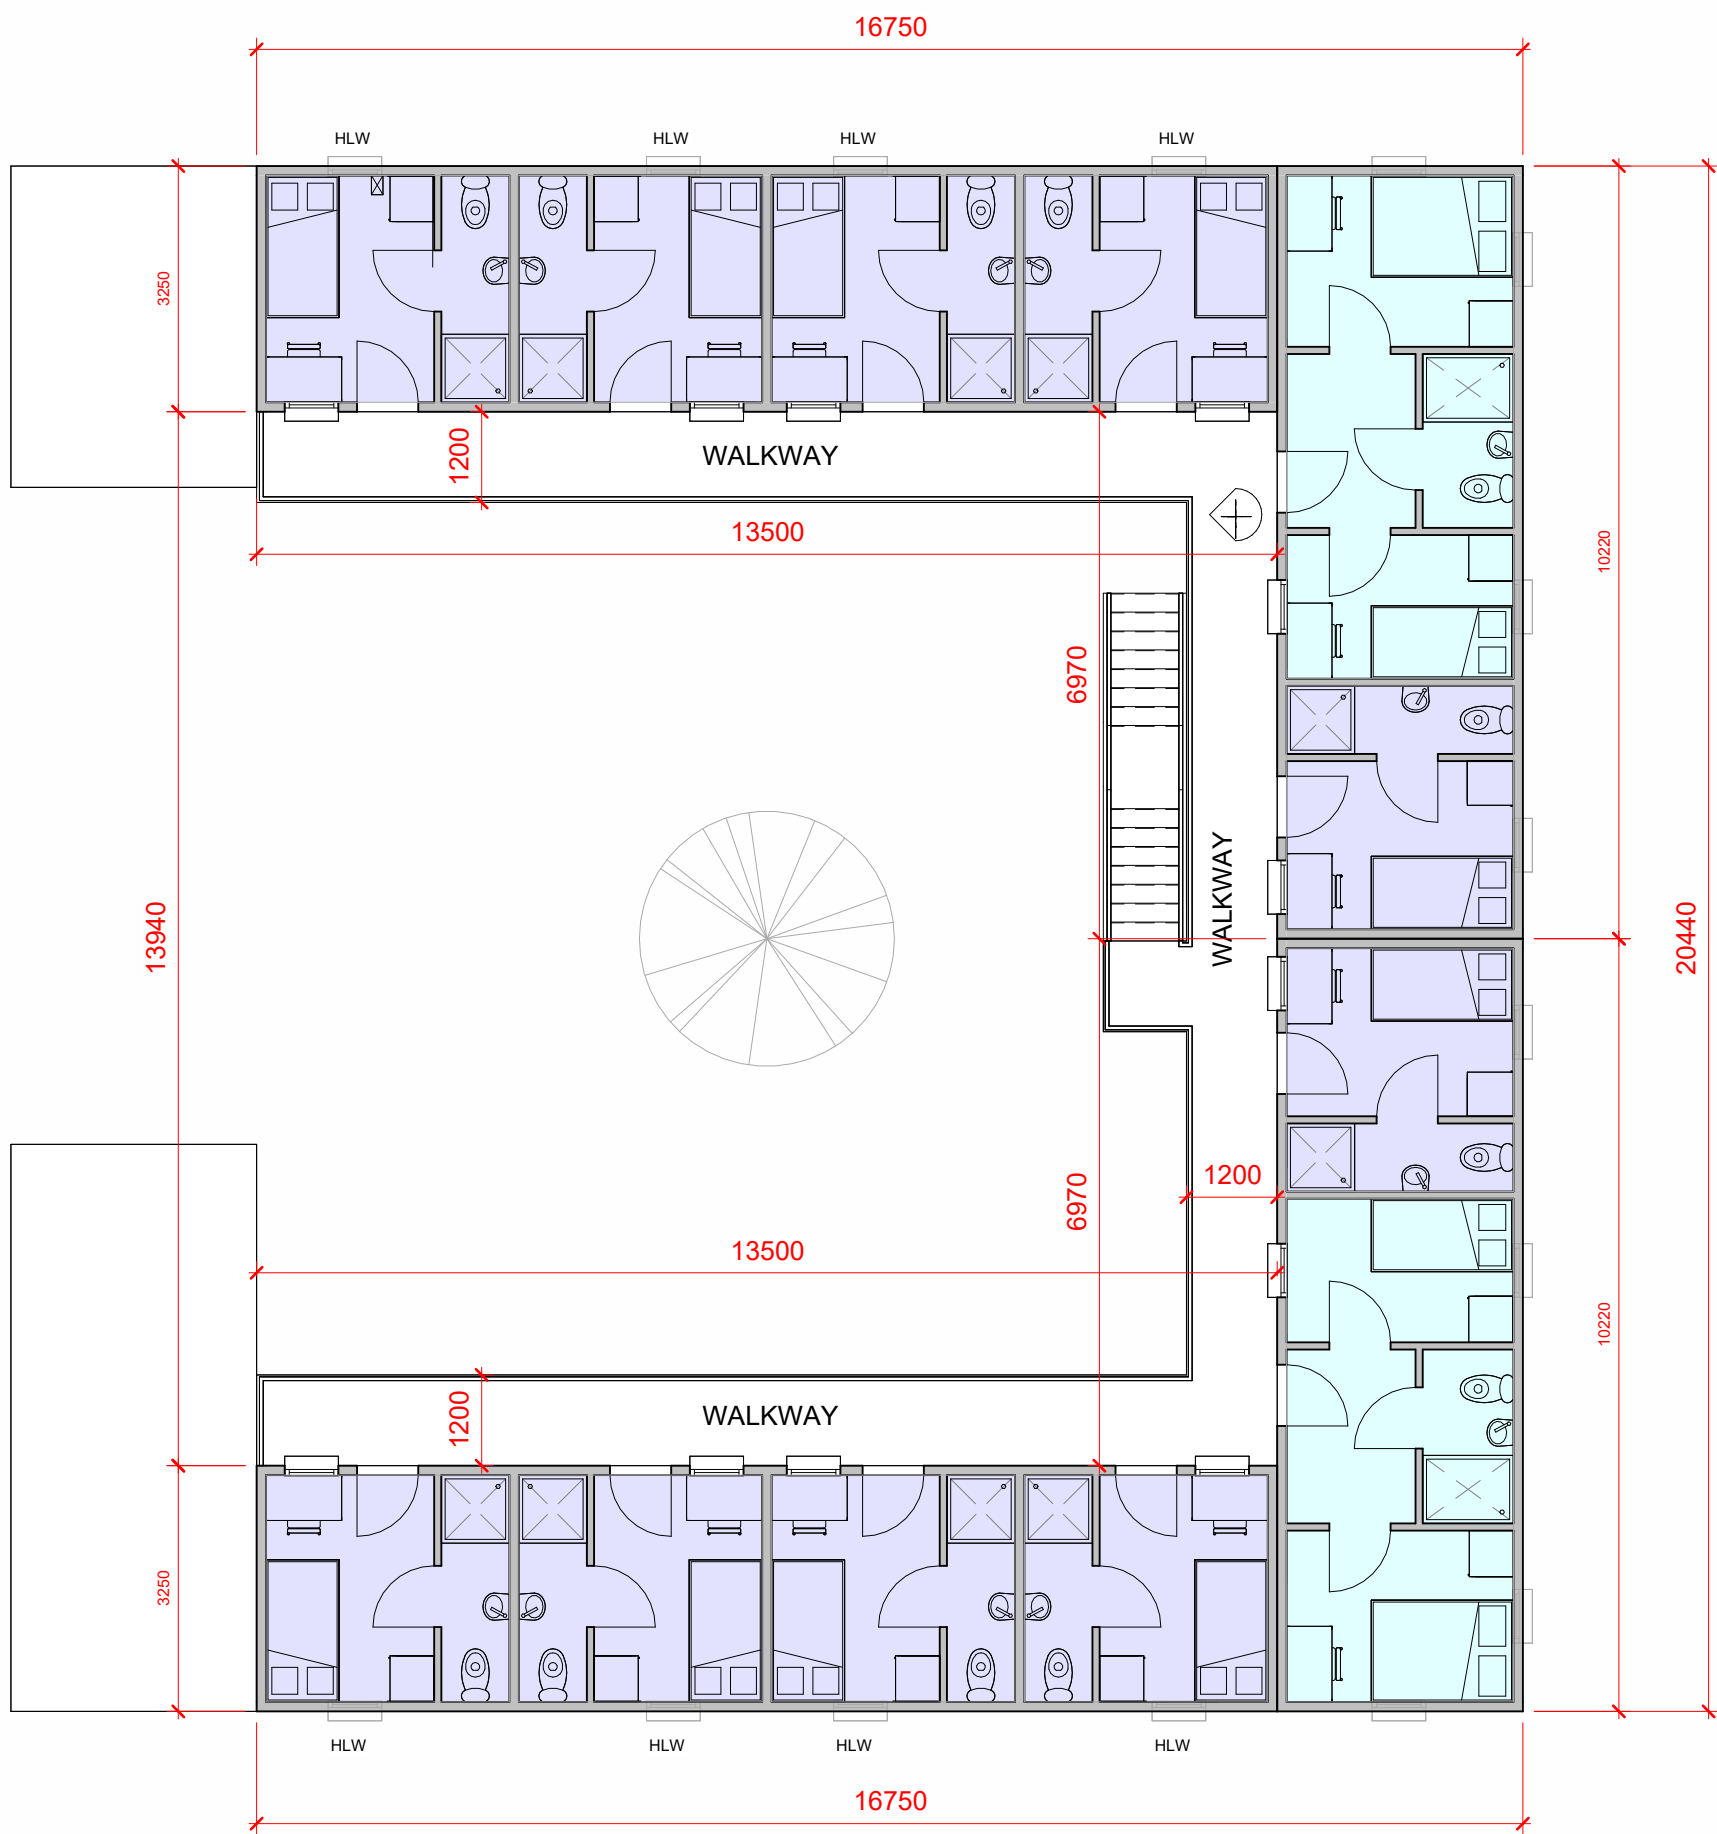

FIRST FLOOR PLAN
1 : 100

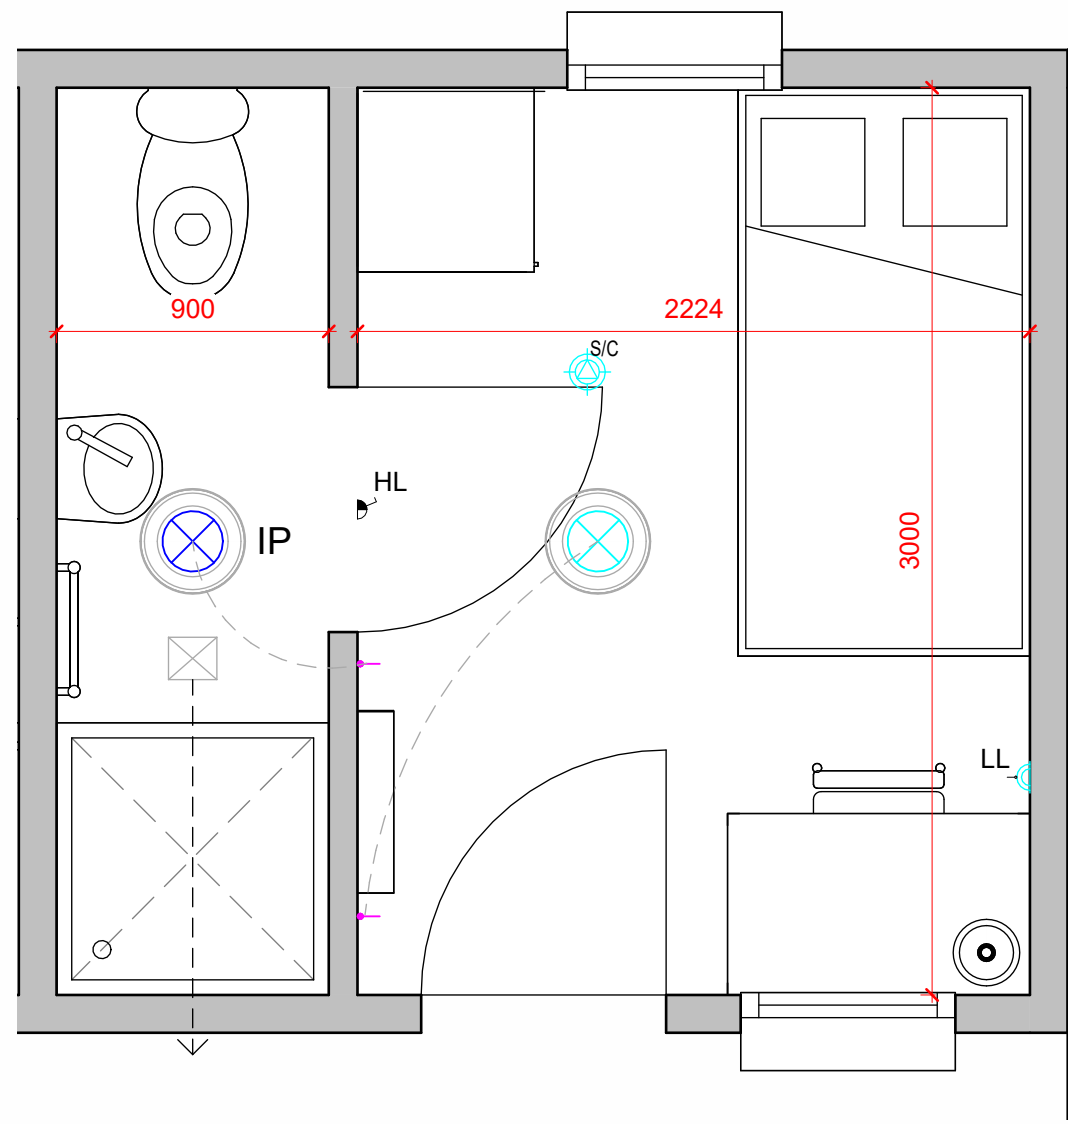

TYPICAL BEDROOM LAYOUT
1 : 25



ELEVATION C
1 : 100




ELEVATION B
1 : 100



ELEVATION A
1 : 100



FRONT ELEVATION
1 : 100

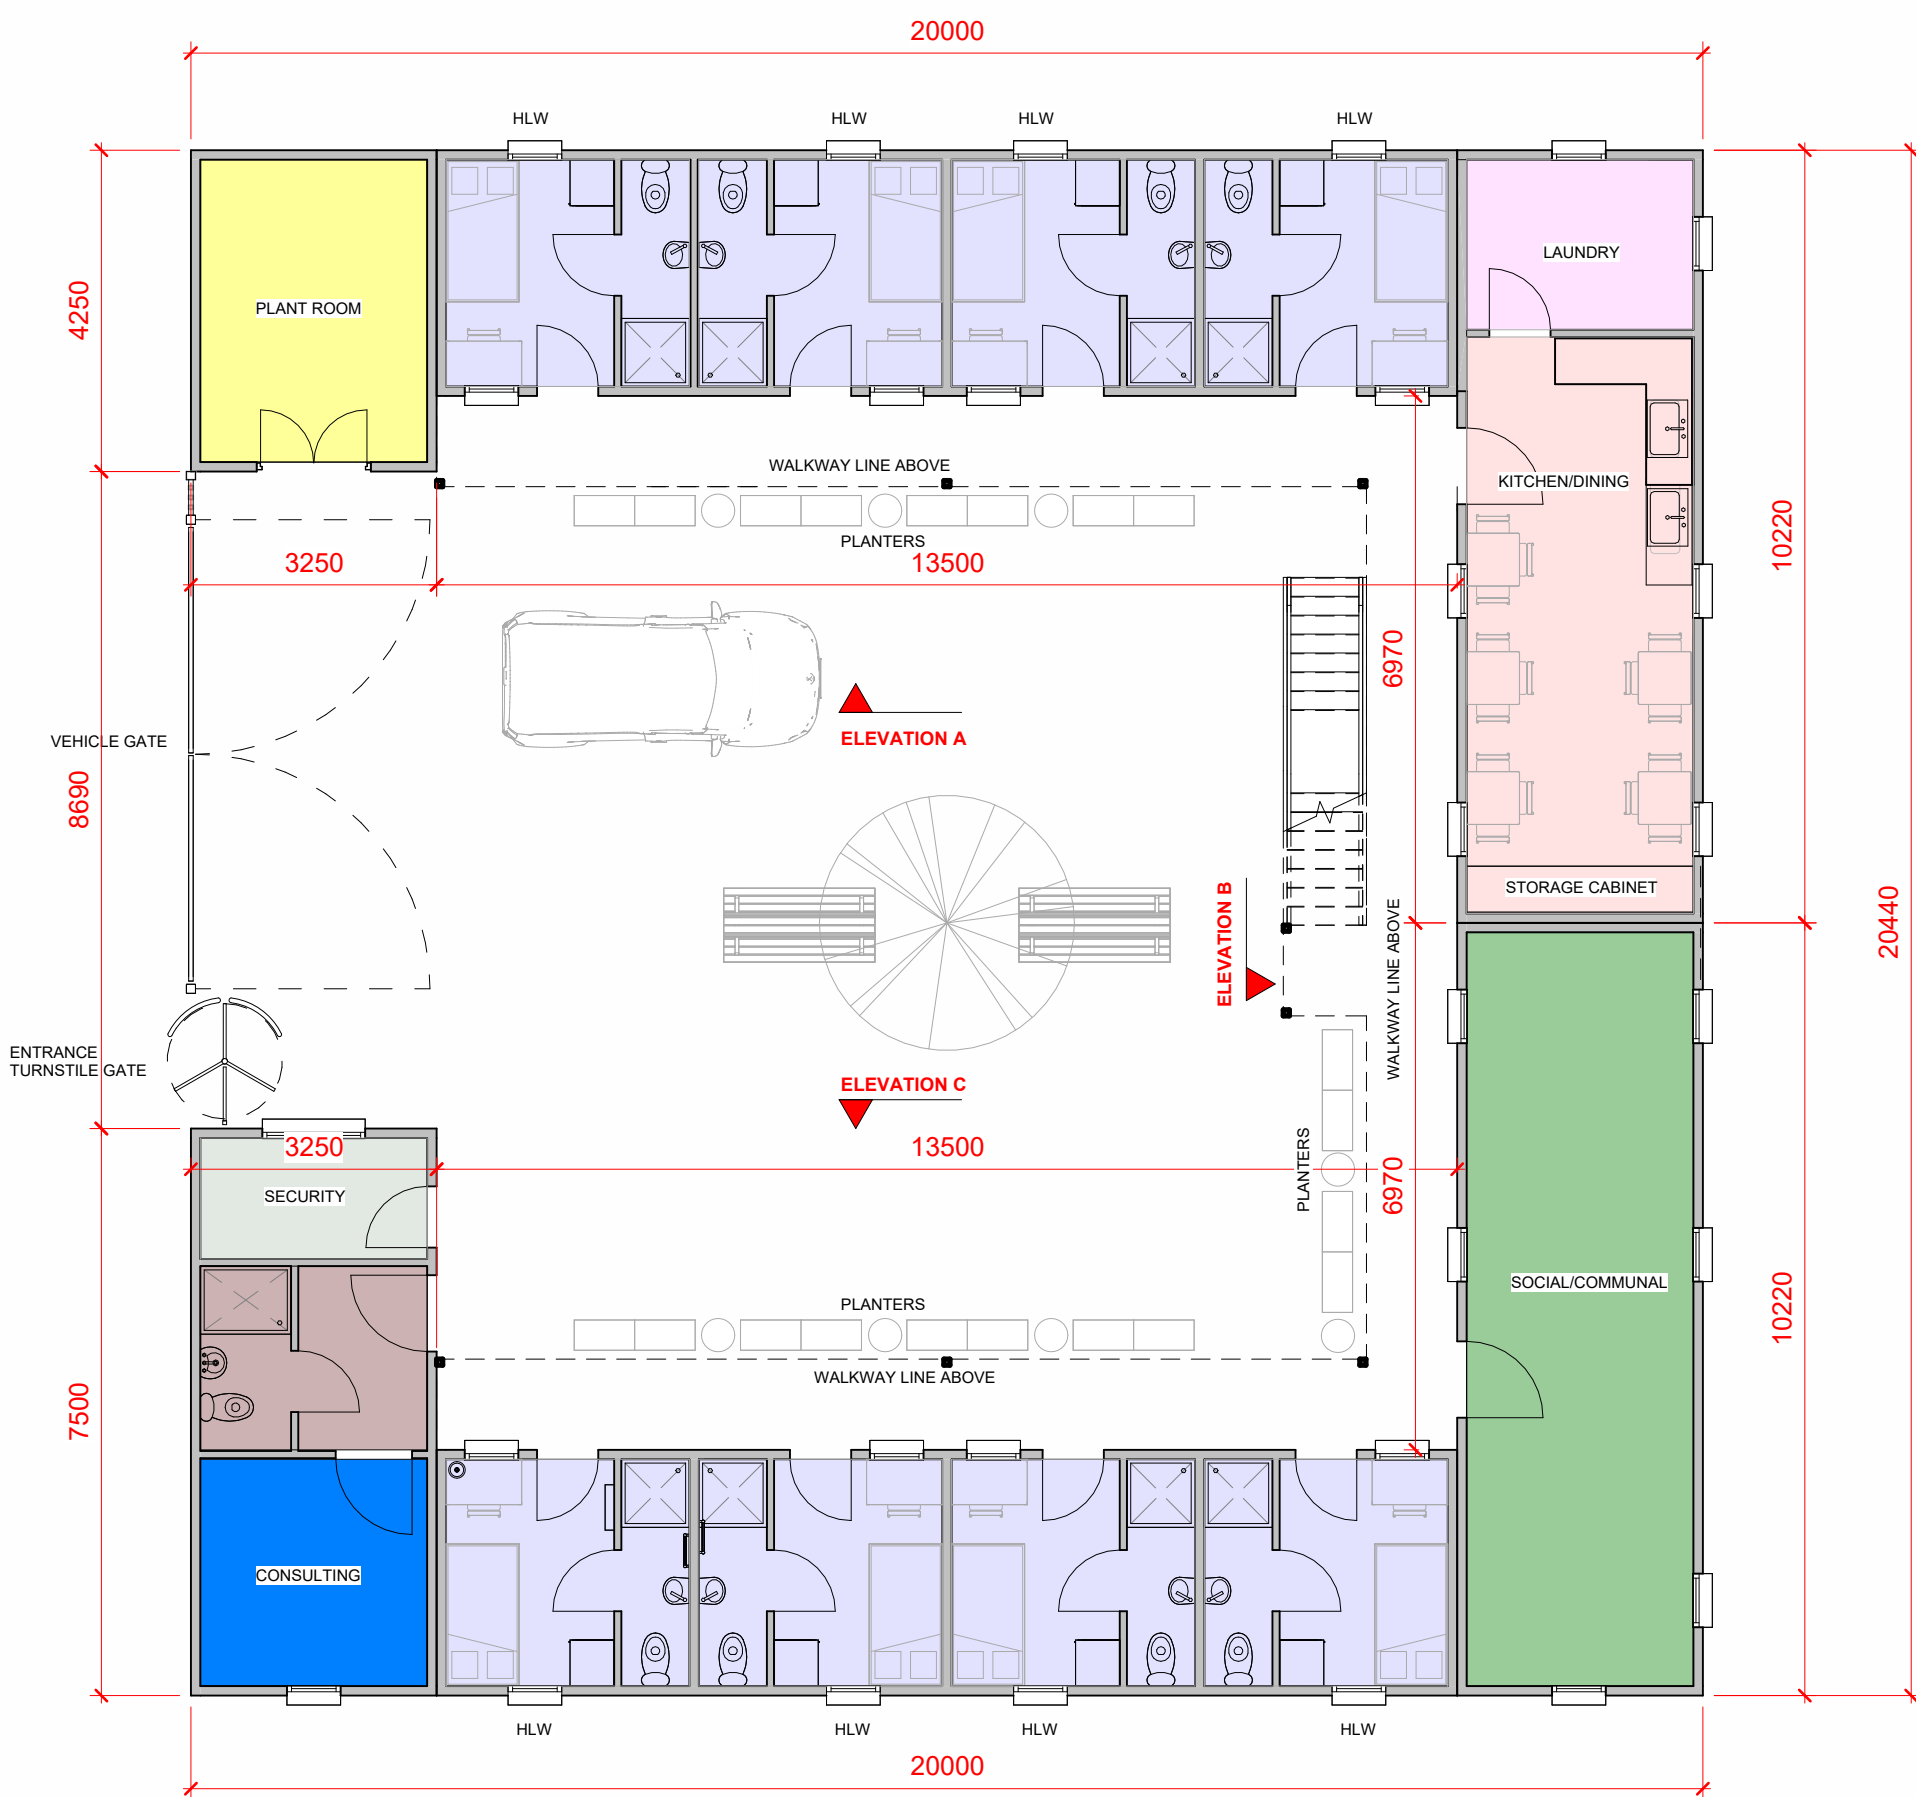

GROUND FLOOR PLAN
1 : 100

- EXTRACT FAN
- IP65 LIGHT
- STANDARD LIGHT
- LIGHT SWITCH
- TWIN SWITCH SOCKETS
- SPUR
- SMOKE AND CARBOR MONOXIDE DETECTOR
- ELECTRIC RADIATOR
- TOWEL RAIL
- LL LOW LEVEL
- HL HIGH LEVEL
- DOUBLE ROOM (FAMILY)
- SINGLE ROOM
- KITCHEN / DINING
- LAUNDRY
- SOCIAL / COMMUNAL
- CONSULTING
- WC/SHOWER/LOBBY
- SECURITY
- PLANT ROOM



TYPICAL BEDROOM LAYOUT



ISOMETRIC VIEW

Safety, Health & Environmental Information

The following hazards/residual risk associated with the work detailed on this drawing have not been eliminated during design. These are highlighted in addition to risks that a competent contractor undertaking this work should be aware of and including within their safe systems of work.


CONSTRUCTION

There is no residual risks that a competent contractor would not otherwise be aware of by looking at the drawing.


Notes: All dimensions are in millimeters (mm) otherwise noted.

This drawing and any information or descriptive matter set herein are the confidential and copyright property of JRL Caledonian Modular Ltd. and must not be disclosed, loaned, copied or used for manufacturing, tendering or any other purpose without the prior consent in writing from JRL Caledonian Modular Ltd.

Rev	Date	Description	By	Chk
CONCEPT				
JRL MODULAR LIMITED				
NEWARK				
Carlton Works, Ossington Road, Newark, NG23 6NT				
Tel: 01636 821 645 www.jrlgroup.co.uk				
CLIENT				
PROJECT				
Project Name				
Enter address here				
TITLE				
Unnamed				
CREATION	DATE	SCALE @ A1	OR	STATUS
01/23/2017	As Indicated	Author	Chk	Checker
JRL CALEDONIAN NO.				
PROJECT NO/COORDINATOR/ZONE/LEVEL/TYPE/ROLE/NUMBER				
CHG. NO.				
REVISION				
© COPYRIGHT. ALL RIGHTS RESERVED.				
THIS DRAWING MUST BE USED IN CONNECTION WITH ALL OTHER RELEVANT DRAWINGS AND INFORMATION.				
ANY DISCREPANCIES MUST BE REPORTED TO JRL CALEDONIAN IMMEDIATELY.				
DO NOT SCALE OFF DRAWINGS. USE DISPLAYED DIMENSIONS.				

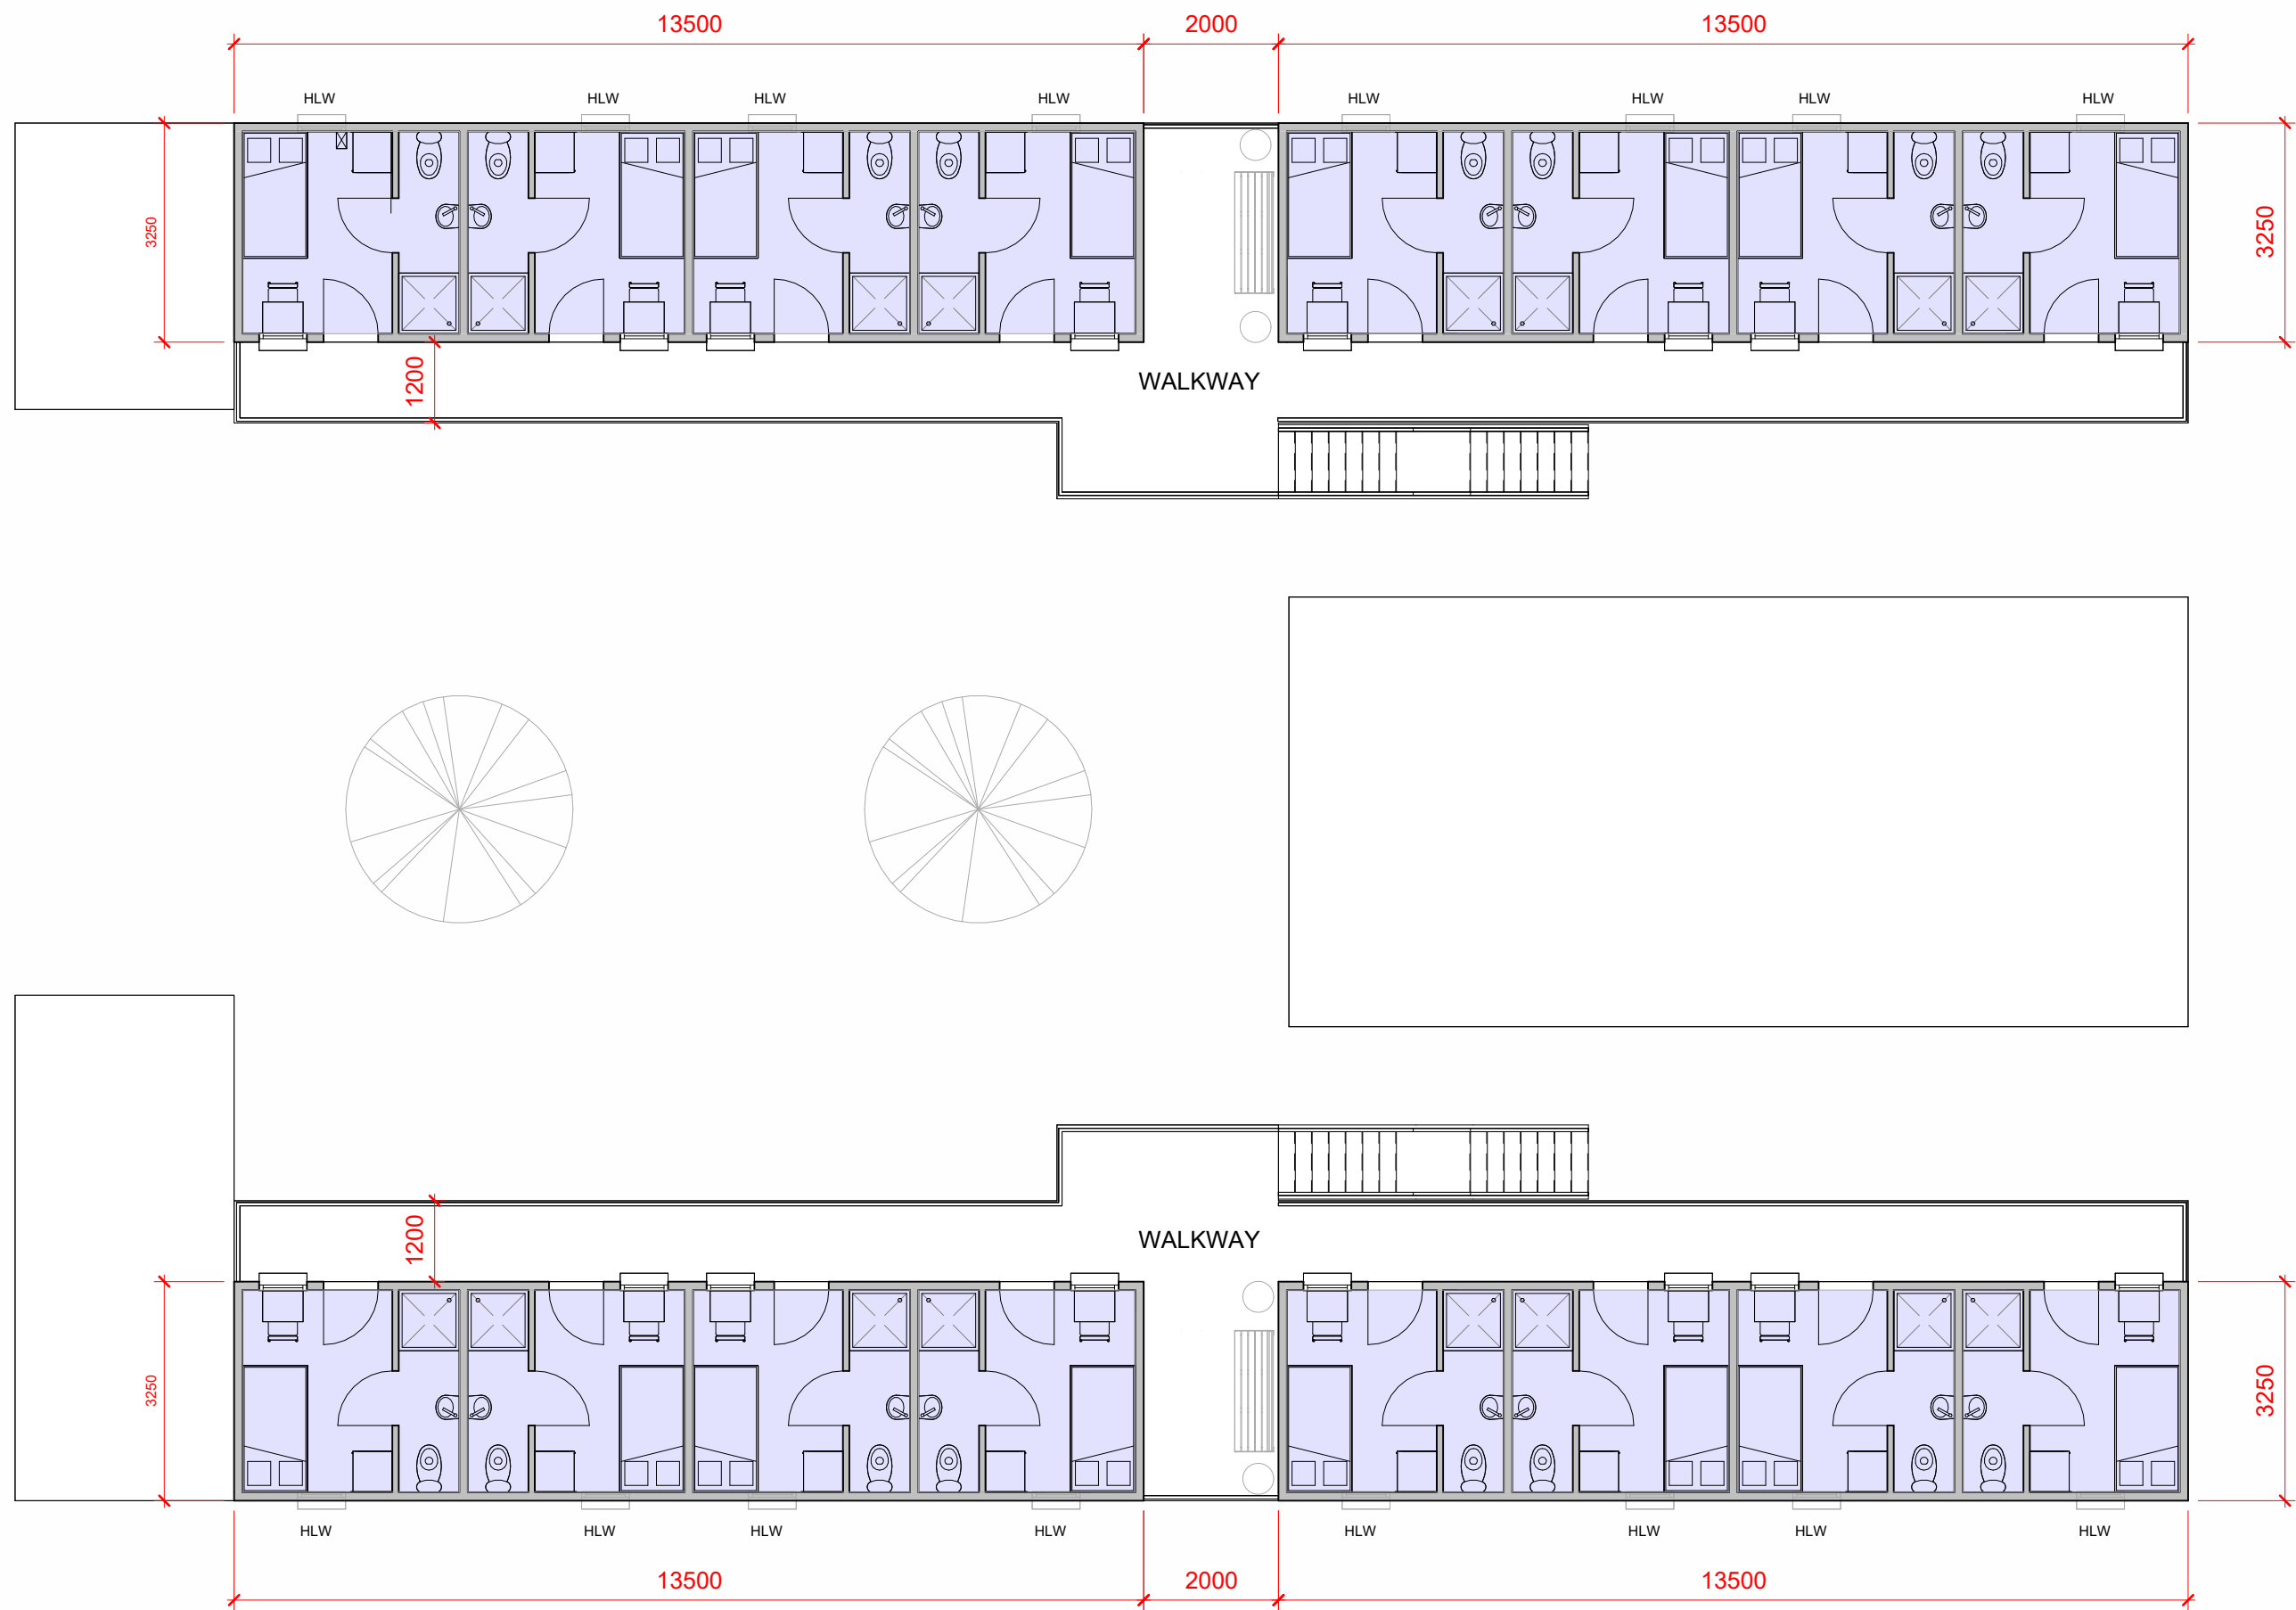

FIRST FLOOR PLAN
1 : 100

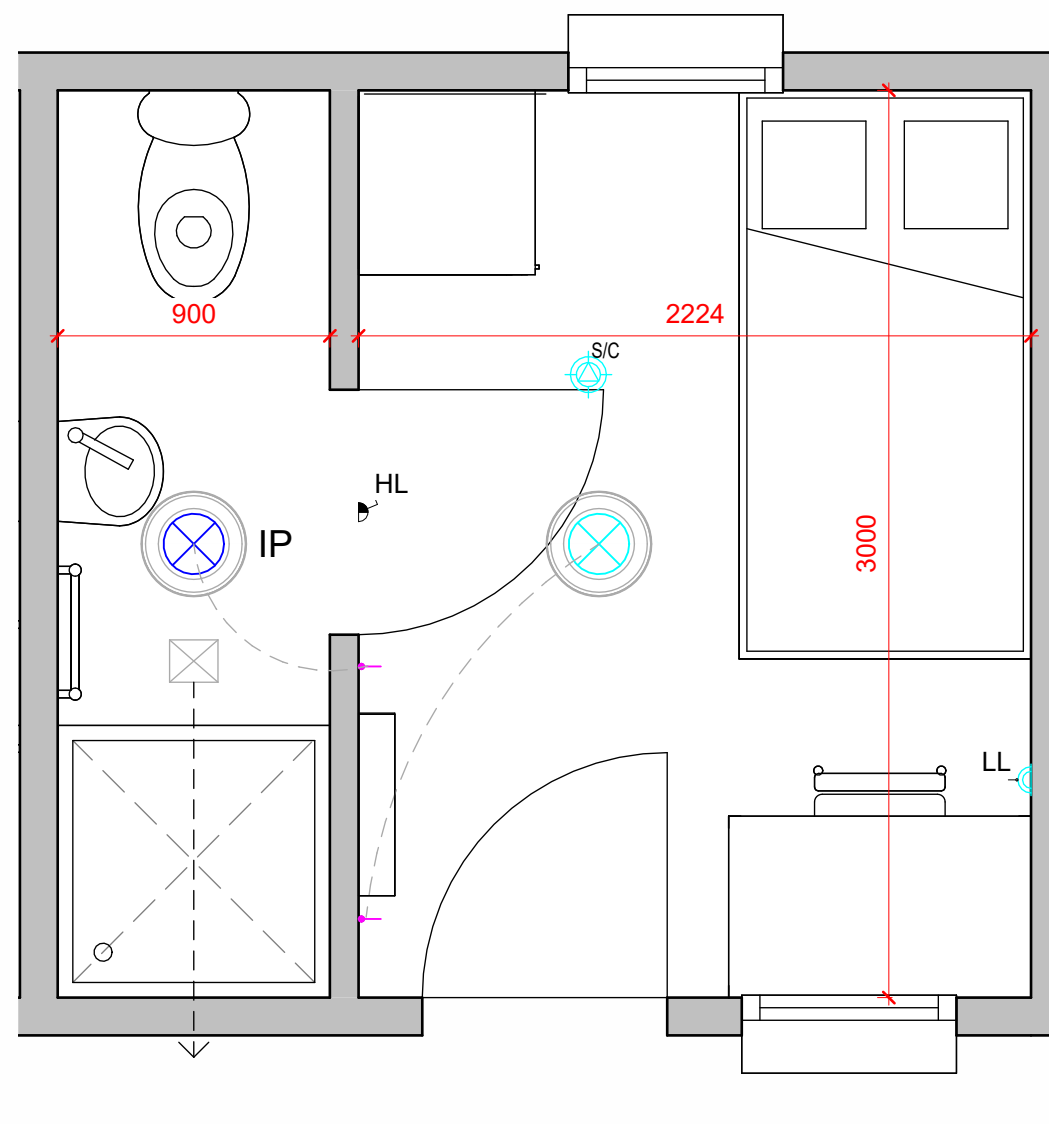


TYPICAL BEDROOM LAYOUT
1 : 25


- EXTRACT FAN
- IP65 LIGHT
- STANDARD LIGHT
- LIGHT SWITCH
- TWIN SWITCH SOCKETS
- SPUR
- SMOKE AND CARBOR MONOXIDE DETECTOR
- ELECTRIC RADIATOR
- TOWEL RAIL
- LL LOW LEVEL
- HL HIGH LEVEL
- SINGLE ROOM
- ACCESSIBLE ROOM
- DOUBLE ROOM (FAMILY)
- KITCHEN / DINING
- LAUNDRY
- SOCIAL / COMMUNAL
- CONSULTING
- WC/SHOWER/LOBBY
- SECURITY
- PLANT ROOM



TYPICAL BEDROOM LAYOUT

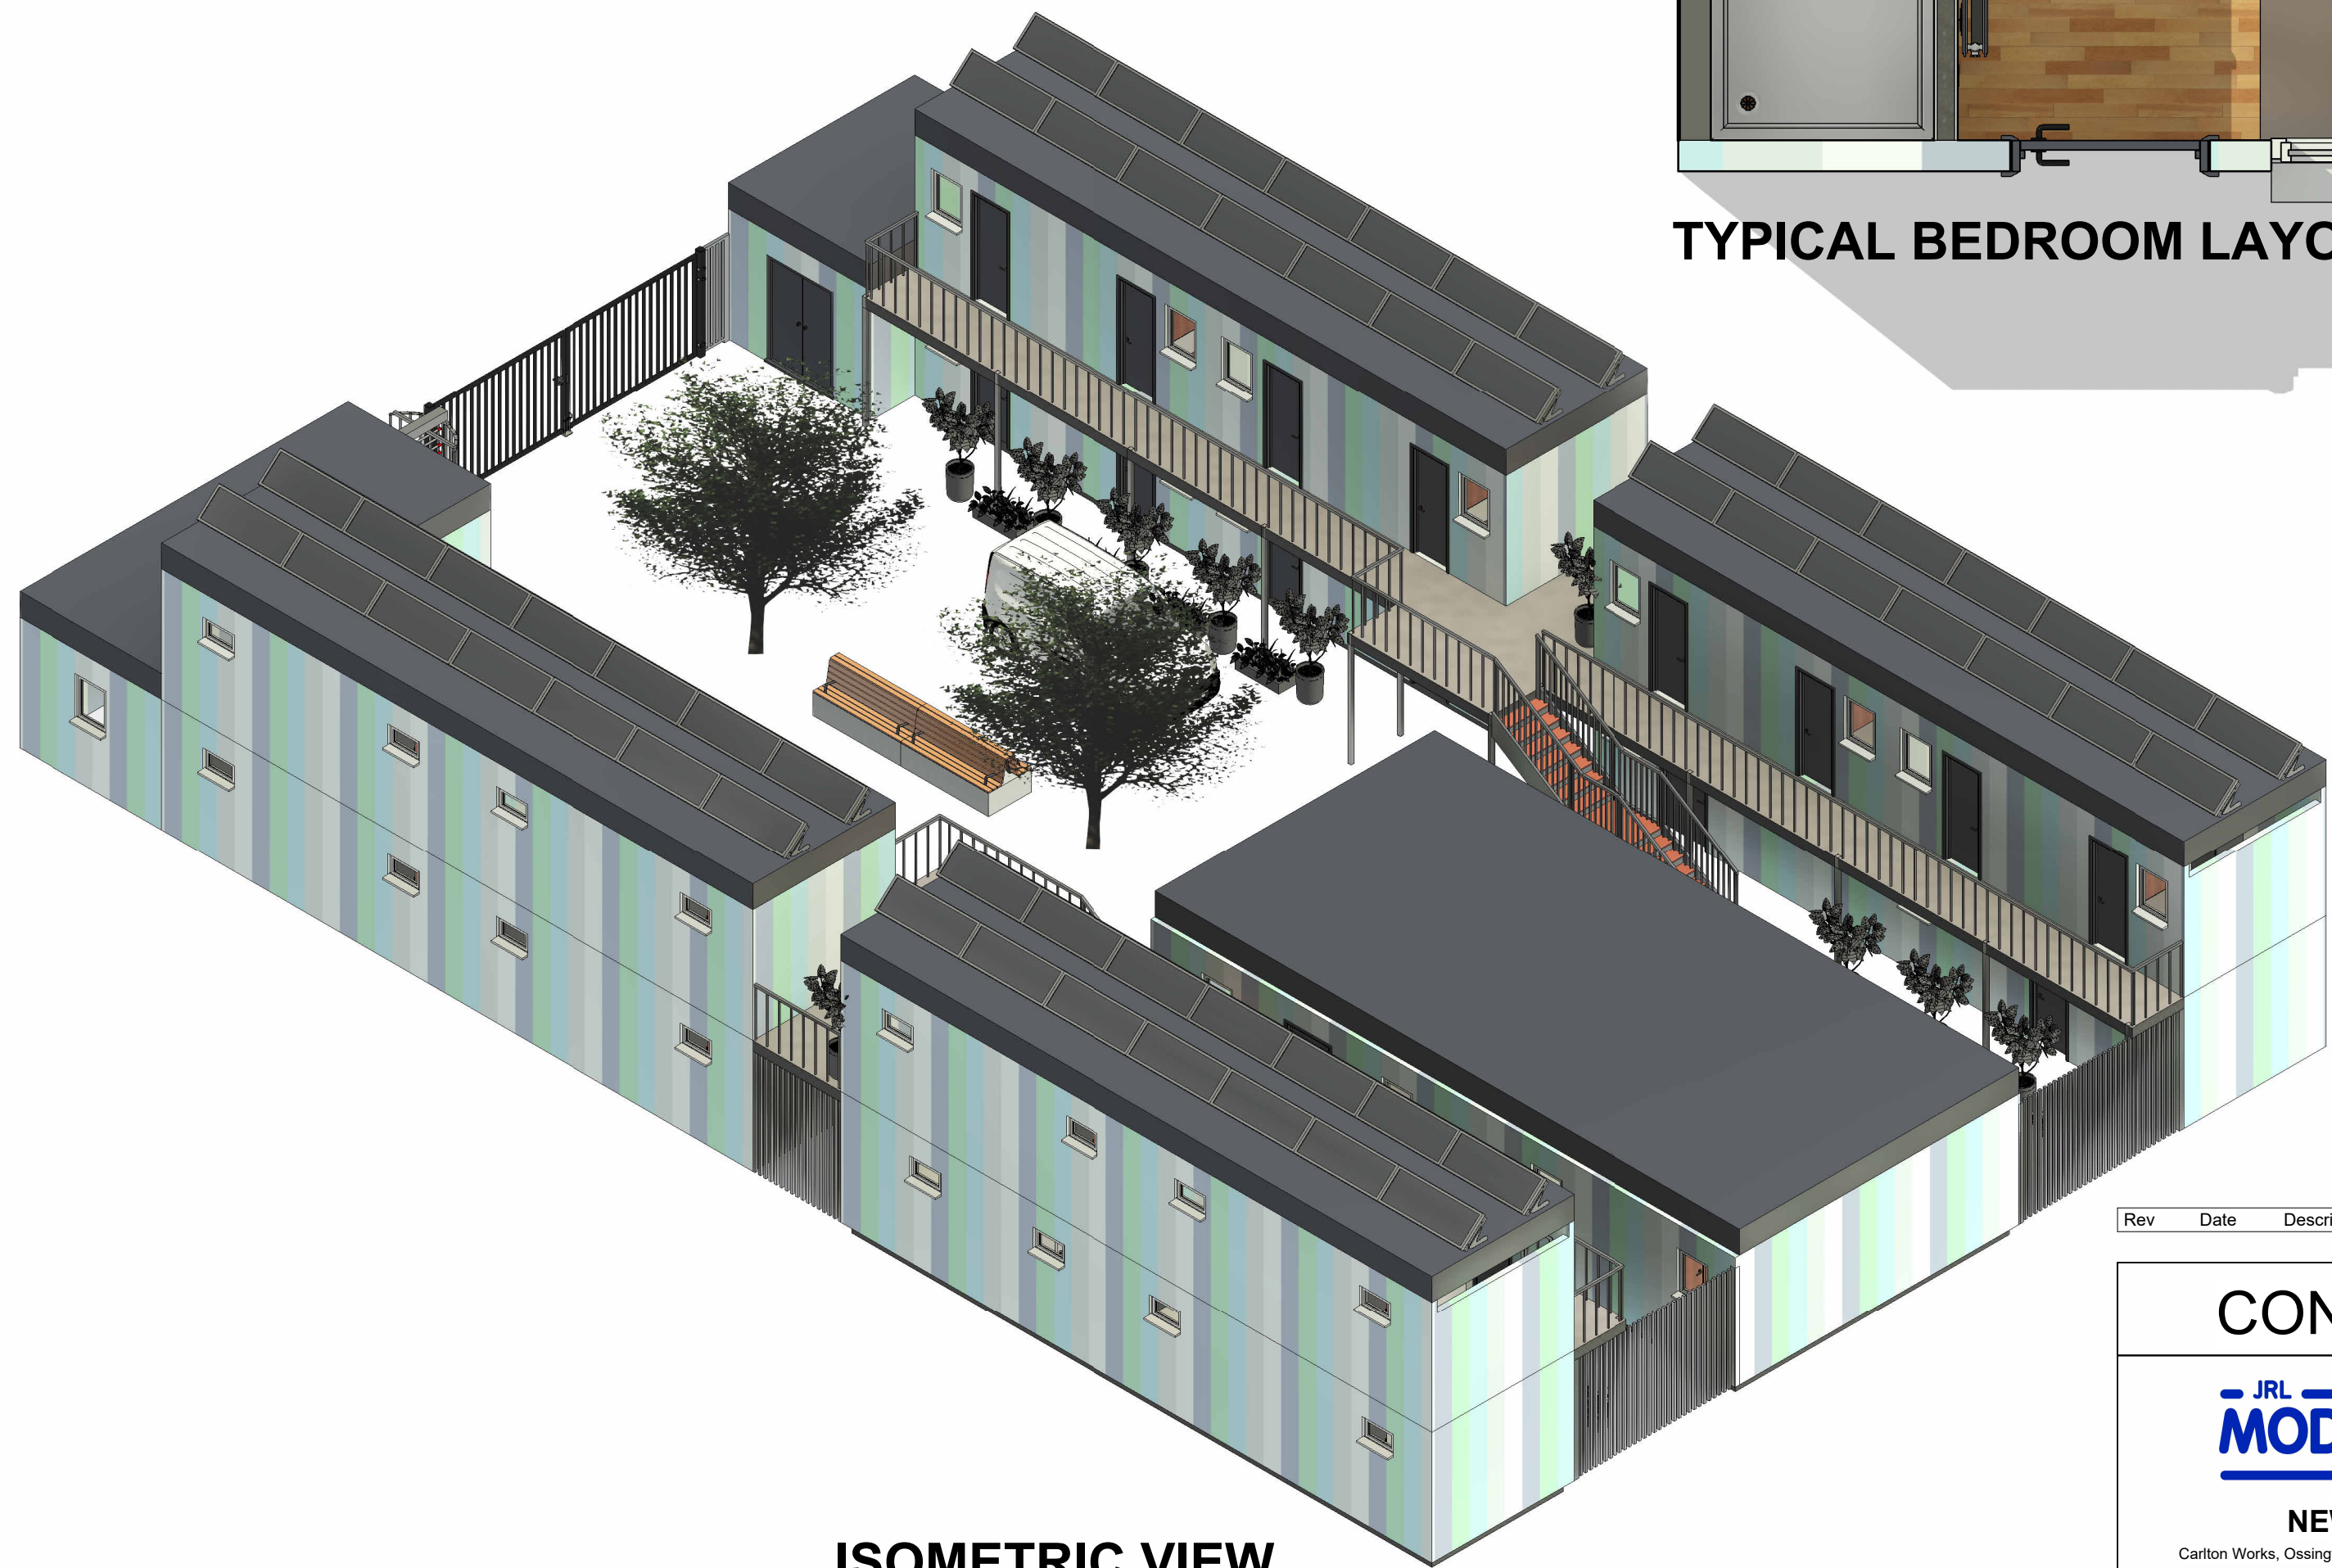

ISOMETRIC VIEW

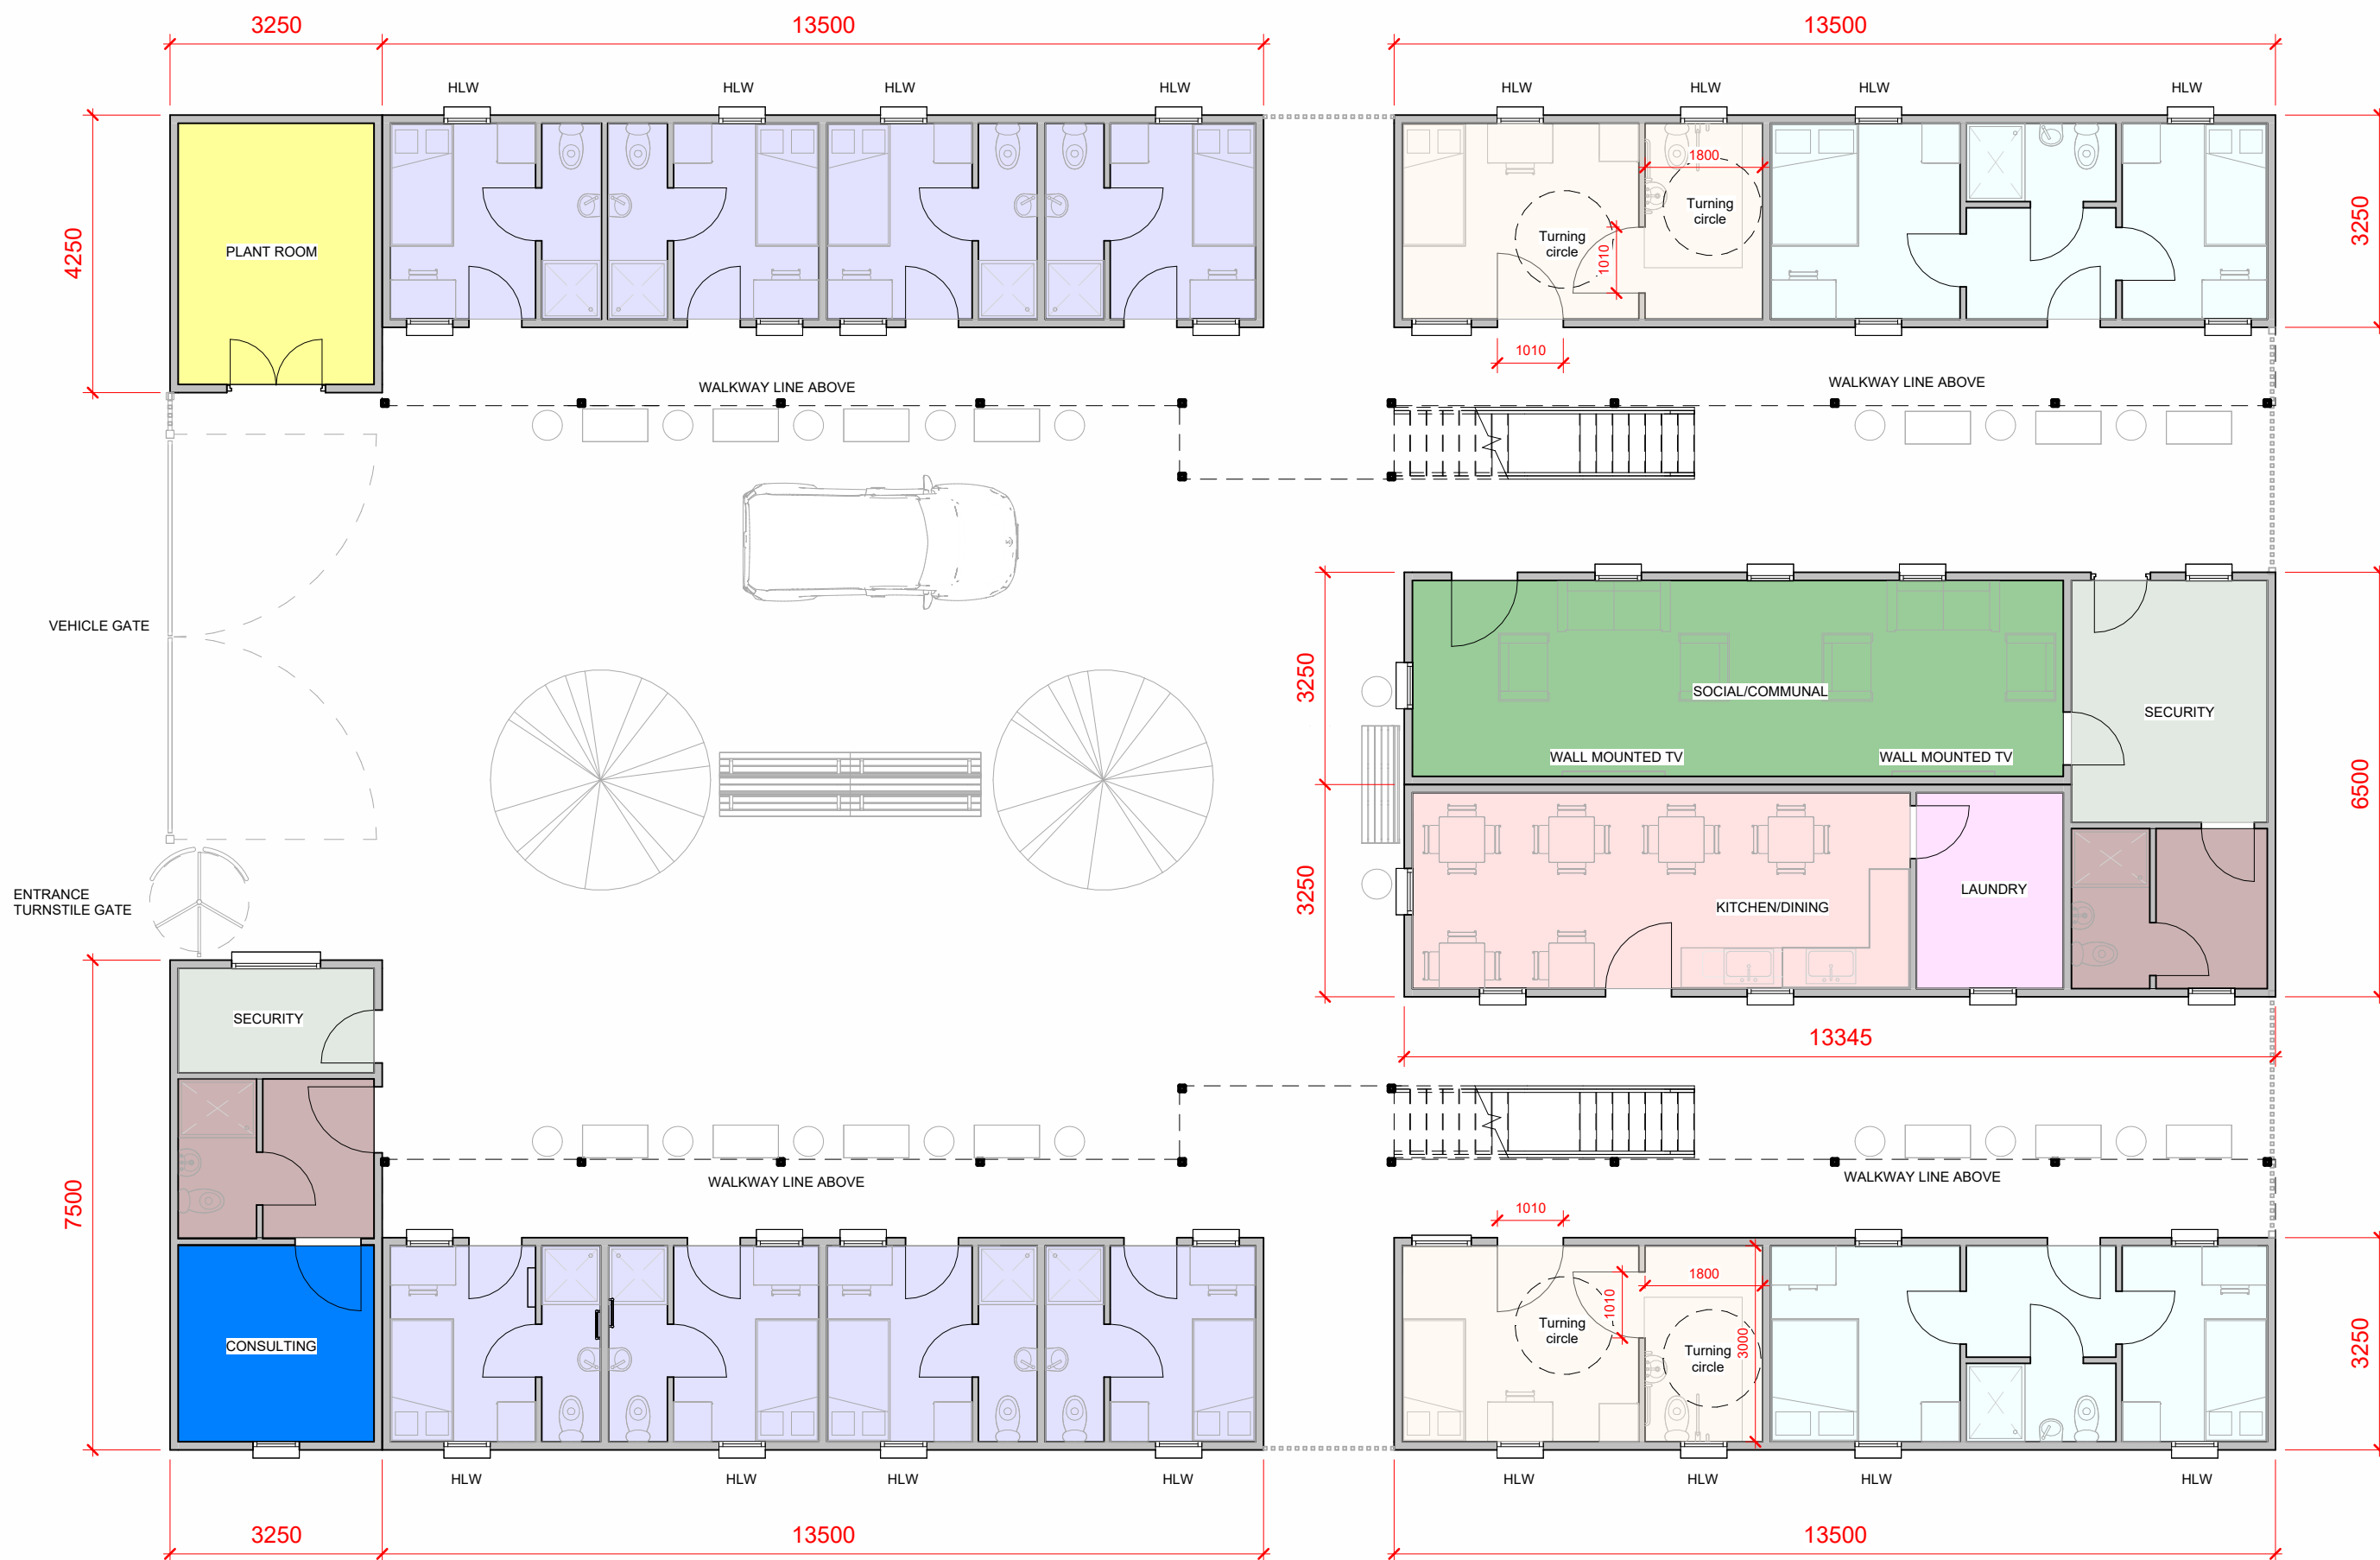


GROUND FLOOR PLAN
1 : 100


Safety, Health & Environmental Information
The following hazards/residual risk associated with the work detailed on this drawing have not been eliminated during design. These are highlighted in addition to risks that a competent contractor undertaking this works should be aware and including within their safe systems of work.
CONSTRUCTION
There is no residual risks that a competent contractor would not otherwise be aware of by looking at the drawing.

Notes: All dimensions are in millimeters (mm) otherwise noted.
This drawing and any information or descriptive matter set herein are the confidential and copyright property of JRL Caledonian Modular Ltd. and must not be disclosed, loaned, copied or used for manufacturing, tendering or any other purpose without the prior consent in writing from JRL Caledonian Modular Ltd.


Rev	Date	Description	By	Chk
CONCEPT				
JRL MODULAR LIMITED				
NEWARK				
Carlton Works, Ossington Road, Newark, NG23 6NT Tel: 01636 821 645 www.jrlgroup.co.uk				
CLIENT				
PROJECT Project Name Enter address here				
TITLE Unnamed				
CREATION DATE 01/23/2017	SCALE @ A1 As Indicated	DR Author	CH Checker	STATUS
JRL CALEDONIAN NO.				
PROJECT NO/ORGANIZATION/LEVEL/TYPE/ROLE/NUMBER				
CWL NO.				
REVISION				
© COPYRIGHT. ALL RIGHTS RESERVED. THIS DRAWING MUST BE USED IN CONNECTION WITH ALL OTHER RELEVANT DRAWINGS AND INFORMATION. ANY DISCREPANCIES MUST BE REPORTED TO JRL CALEDONIAN IMMEDIATELY. FOR CONSTRUCTION. DO NOT SCALE OFF DRAWINGS. USE DISPLAYED DIMENSIONS.				

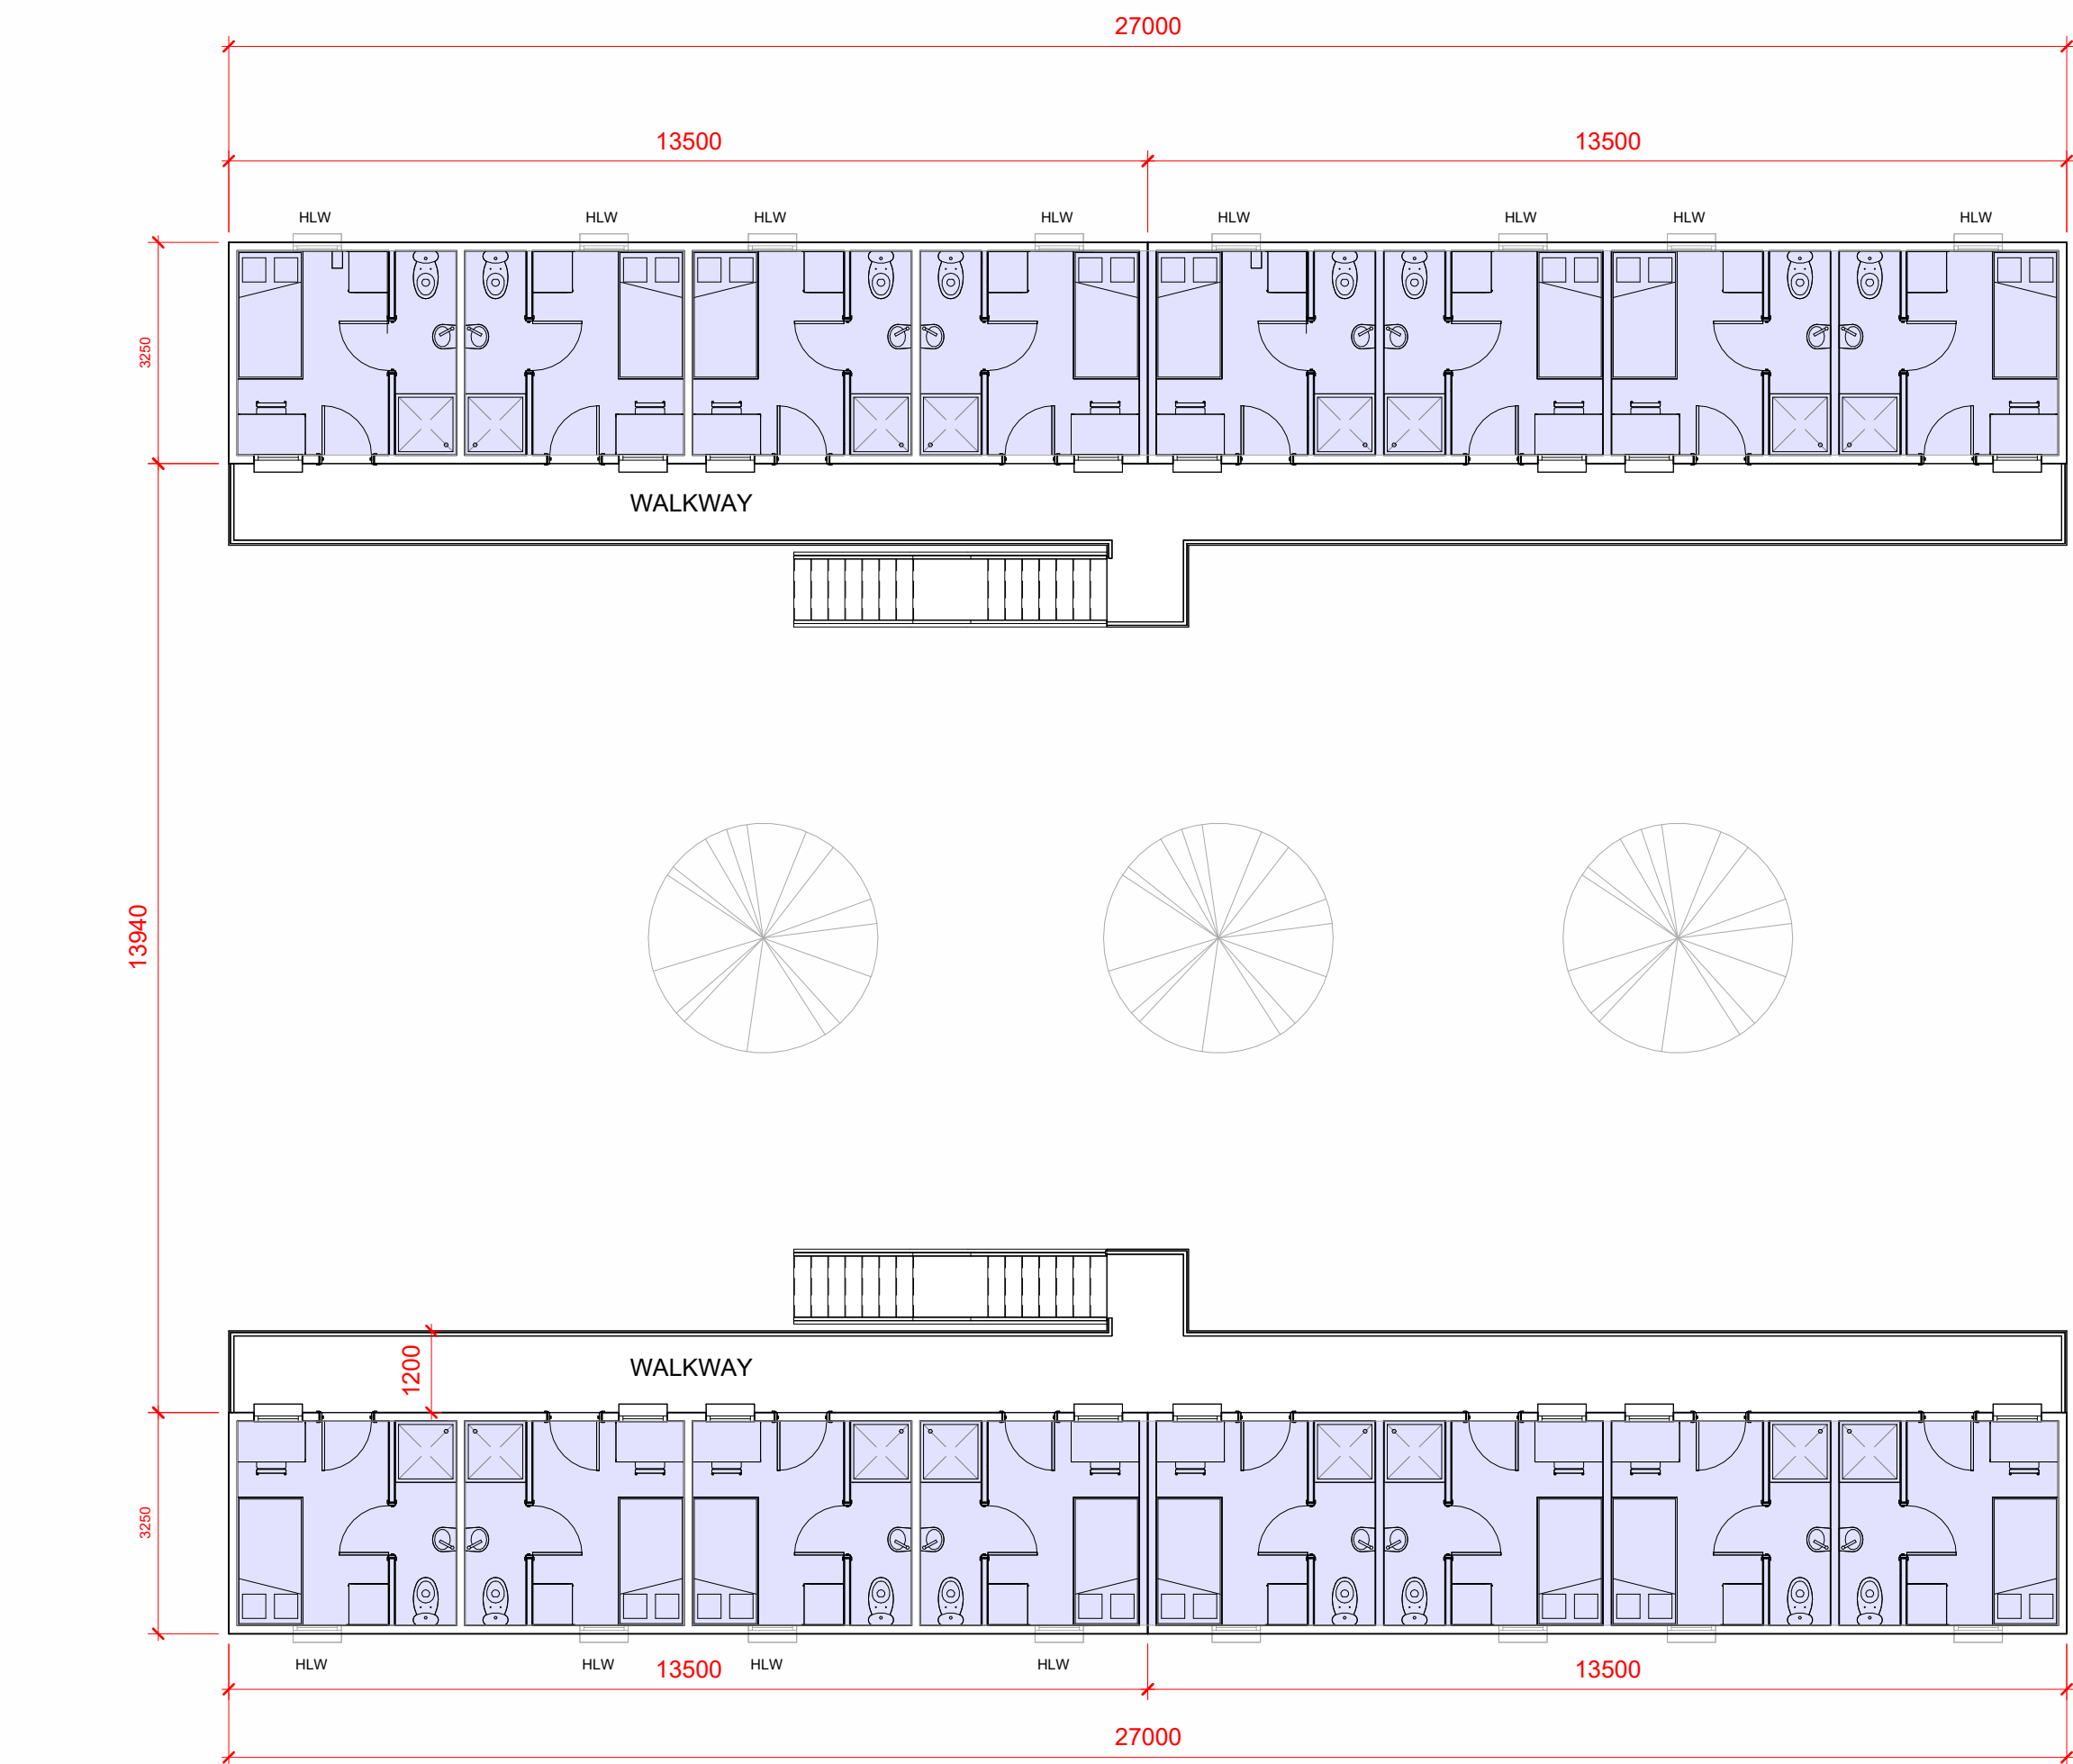

FIRST FLOOR PLAN
1 : 100

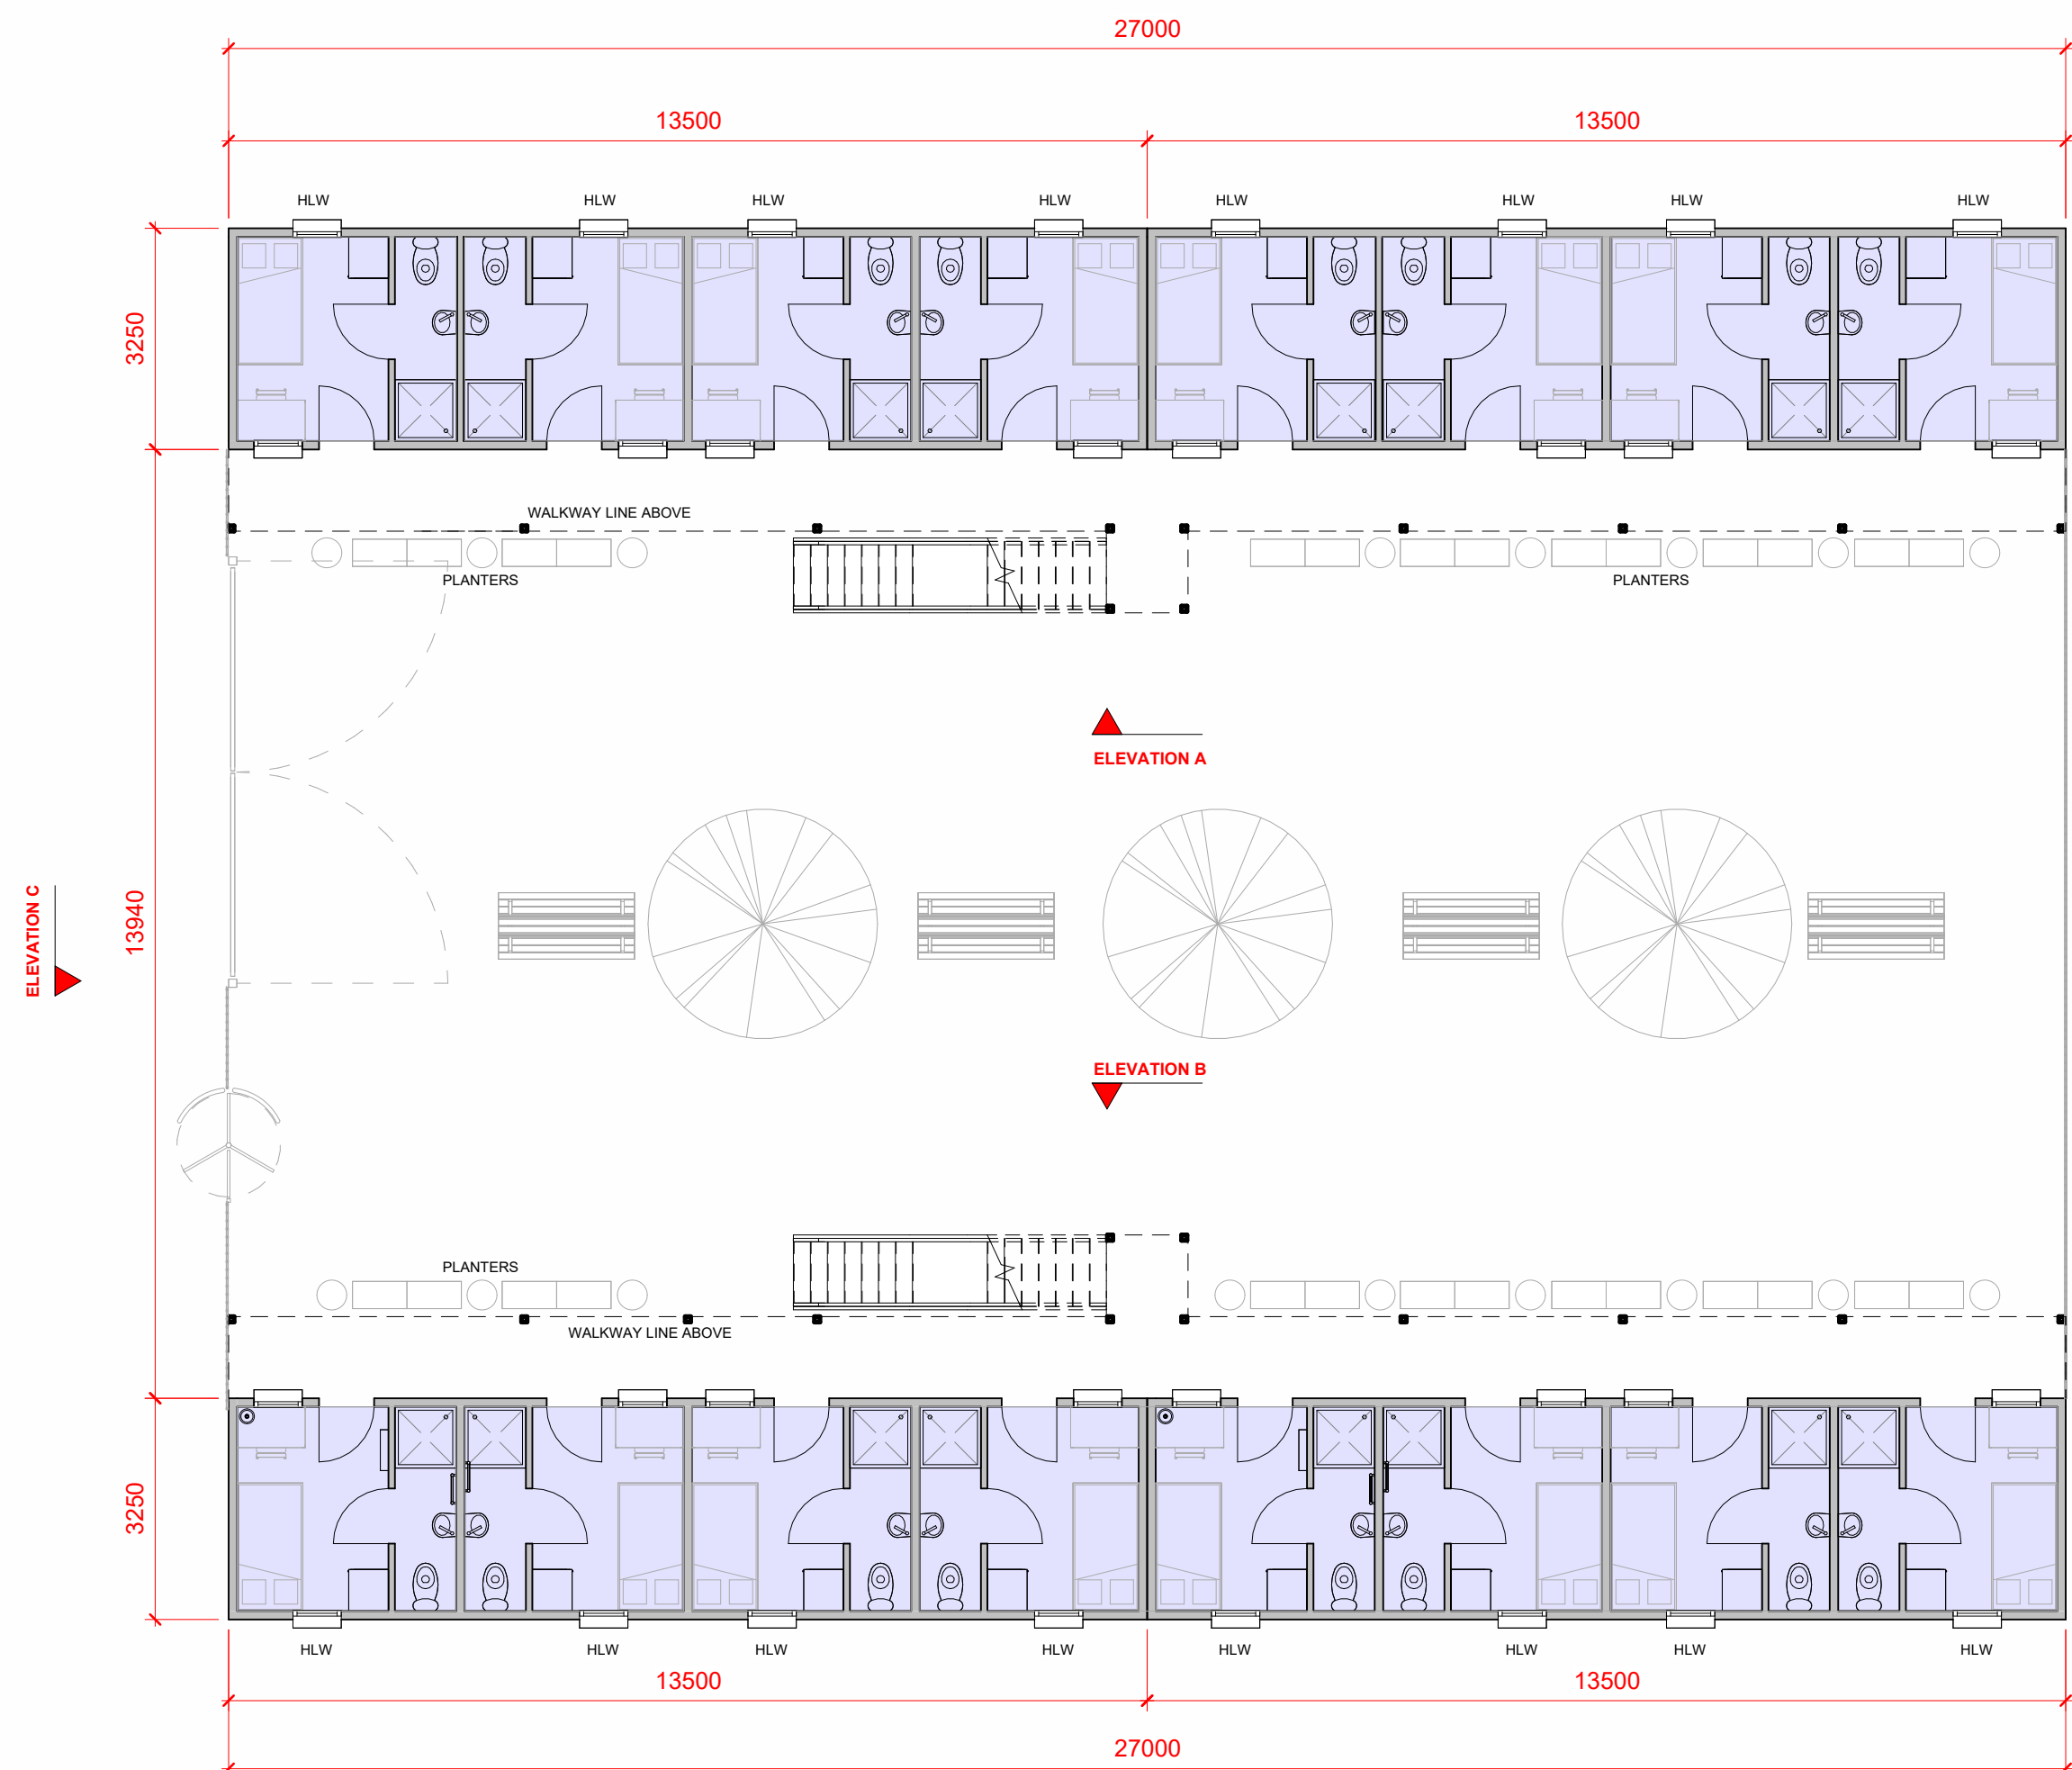

GROUND FLOOR PLAN
1 : 100

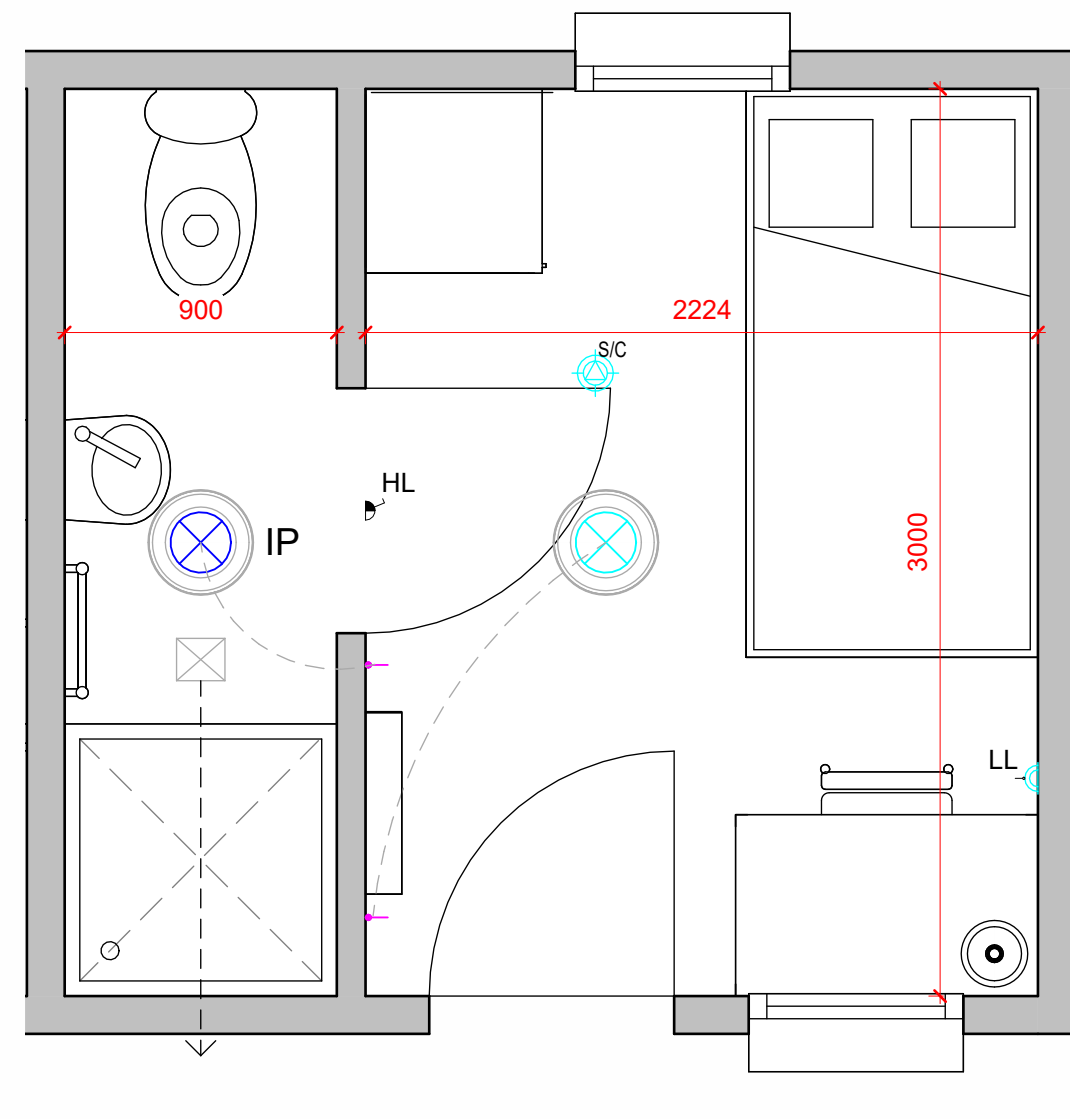

TYPICAL BEDROOM LAYOUT
1 : 25

- EXTRACT FAN
- IP65 LIGHT
- STANDARD LIGHT
- LIGHT SWITCH
- TWIN SWITCH SOCKETS
- SPUR
- SMOKE AND CARBOR MONOXIDE DETECTOR
- ELECTRIC RADIATOR
- TOWEL RAIL
- LL LOW LEVEL
- HL HIGH LEVEL



TYPICAL BEDROOM LAYOUT




ELEVATION A
1 : 100



ELEVATION B
1 : 100



ELEVATION C
1 : 100

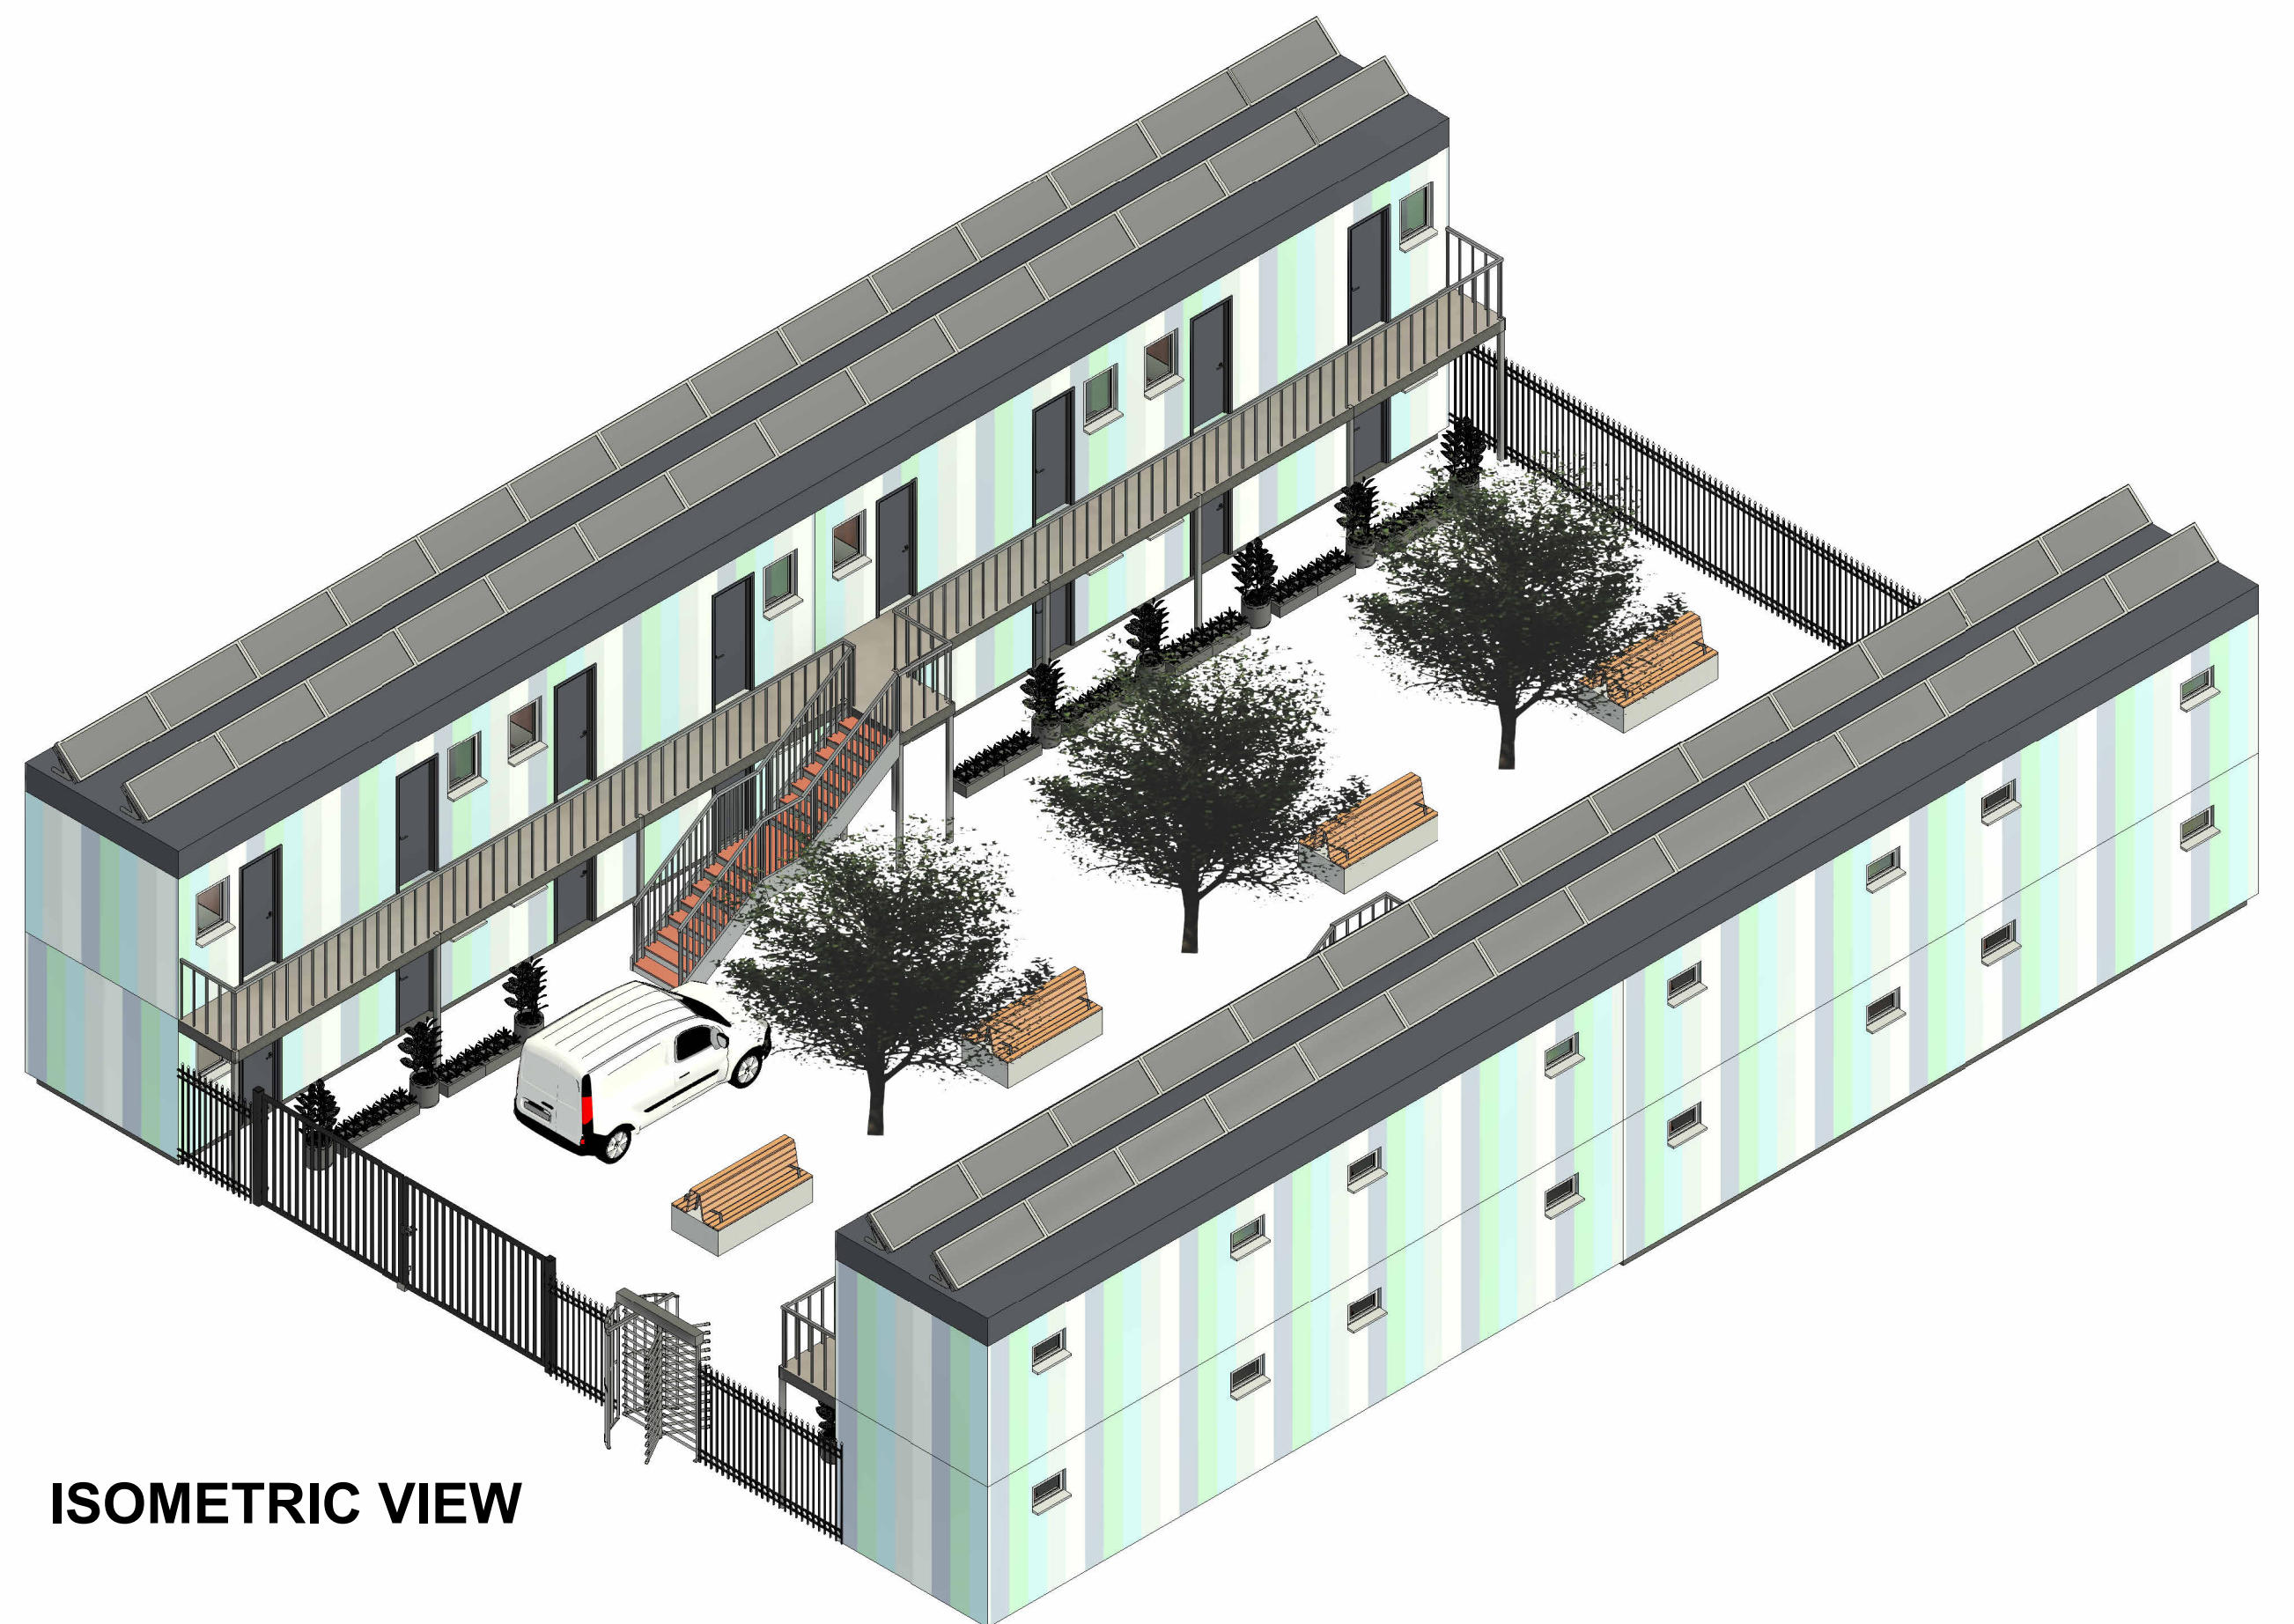


ISOMETRIC VIEW

Rev	Date	Description	By	CHK
CONCEPT 4				
JRL MODULAR LIMITED				
NEWARK				
Carlton Works, Ovington Road, Newark, NG23 8RT				
Tel: 01636 621 645 www.jrlgroup.co.uk				
Client				
Project Name				
Enter address here				
Title				
Unnamed				
DESIGNER	SCALE	DATE	BY	CHK
JRL	As Issued	10/10/2023	CH	CH
PROJECT MODIFICATION ZONES & LAYOUTS				
REVISION				
COPYRIGHT: ALL RIGHTS RESERVED. NO PART OF THIS DOCUMENT MAY BE REPRODUCED OR TRANSMITTED IN ANY FORM OR BY ANY MEANS, ELECTRONIC OR MECHANICAL, WITHOUT PERMISSION IN WRITING FROM JRL MODULAR LIMITED. ALL RIGHTS RESERVED.				


RAPID RELIEF SHELTER UNIT - SINGLE OCCUPANCY ROOM

4 ROOM UNIT

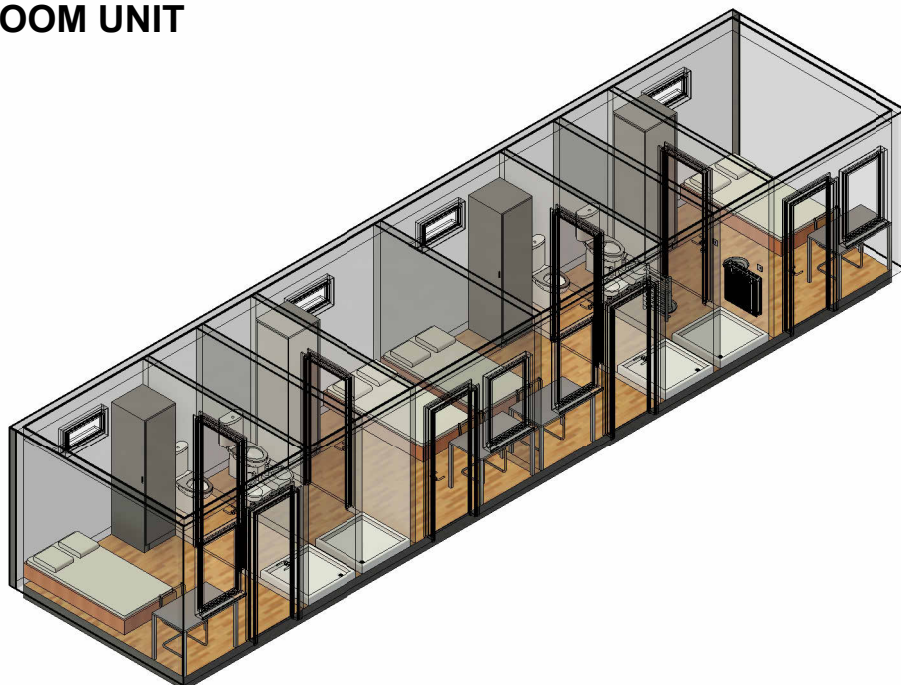

TYPICAL ROOM LAYOUT

ISOMETRIC VIEW

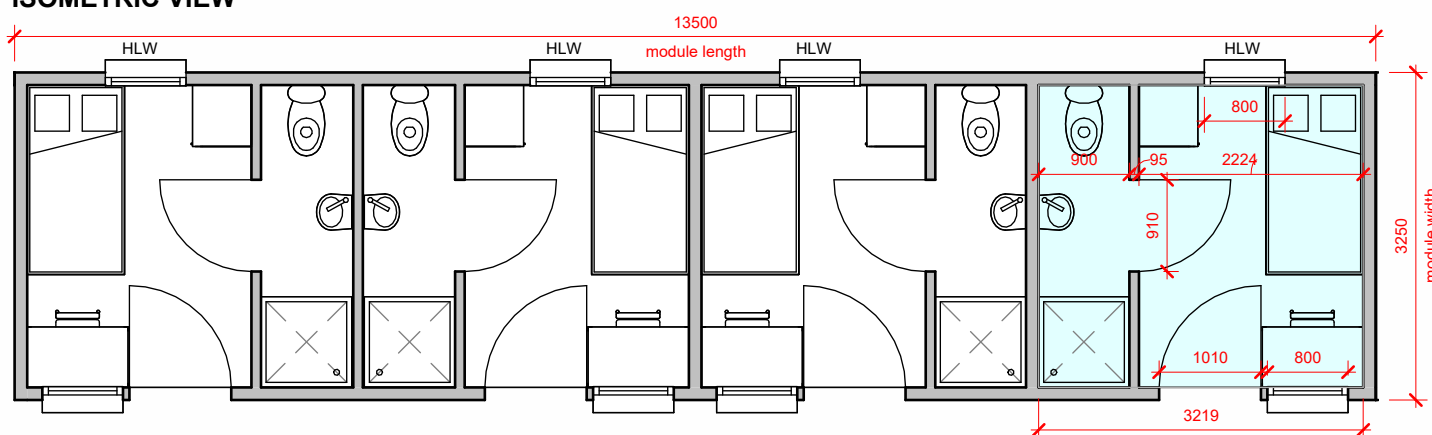

MODULE PLAN

DESCRIPTION

- Insulated walls, floors and ceiling to building Regulation
- Fire compartment - compartmentation exceeds Building Regulations
- Acoustic performance to Building Regulation
- Wifi points for internet connectivity.
- Fully furnished bedroom and shower room
- Separate communal facilities and amenities to promote co-living: such as, Shared kitchen; shared dining/living and laundry can be offered based upon clients spec.
- Standard uPVC Double Glazed windows and doors (Optional PAS24 window and doors)
- Modern Method of Construction are all built off site and quality checked throughout the process in controlled factory environment.
- Fully tested and commissioned pre delivery and final connection
- BOPAS accredited to 60 years lifespan in static location.
- Configure Module design up to 3 storeys – stackable.
- Utility electric, water and waste connection, usage manage with submeter to aid management and monitoring.
- PV panels (Optional)
- Electric heating
- LIGHTING: PIR or Switch

SPECIFICATION

U VALUES OF BUILDING ELEMENTS:

FLOOR - 0.18W/m²K

EXTERNAL WALLS - 0.26W/m²K

ROOF - 0.16W/m²K

WINDOWS - 1.6W/m²K

DOORS - 1.6W/m²K

BUILDING FIRE RATED : (REI 60) EN 1301-2

EXTERNAL WALL CONSTRUCTION:

Rainscreen cladding, design/finish to suit client choice incorporating cavity insulation, JRL Modular propriety wall build up.

FLOOR CONSTRUCTION:

All floors to be constructed to insulated 60 mins fire rated floor.

ROOF CONSTRUCTION:

Roof construction to comprise of structural steel frame overdrawn with 15mm OSB board, on timber firrings to form a 1° pitch, insulation between joist, vapour control layer and 12.5mm plaster board, Single ply water proof membrane. Over all roof build up to achieve u-value of 0.16W/m²K

DOORS AND WINDOWS:

EXTERNAL DOORS:

- Standard uPVC external door with spy hole to achieve u-value of 1.6W/m²K

(PAS24 Door with spy hole) - Optional

INTERNAL DOORS

- 900x2100mm s/o internal door

WINDOWS:

- 800 x 1200mm Standard uPVC Double Glazed ((Argon) Window (4mm thick each pane) - CILL@ 900mm high to achieve u-value of 1.6W/m²K (Window Fire Rated -REI 30)
- 800 x 450mm HLW uPVC Double Glazed Window (4mm thick each pane) - CILL@1650mm high to achieve u-value of 1.6W/m²K

(PAS24 Windows) - Optional

- With 6.8mm thick laminated glass

Low energy lightinh-switched **PIR** optional

TOILET AREA:

WALL FINISHES:

- Polyclad Wall Lining on 9mm ply including shower

CEILING FINISHES:

- Painted white (Anti Moisture paint)

FLOOR FINISHES:

- Polysafe 2mm non slip vinyl

FITTINGS:

WC: Floor mounted toilet pan
900x900mm Square shower tray
Wall hung WHB, Vanity, toilet, robe hook, elec. towel, shaver and elec shower.

SHOWER SCREEN: Shower Curtain
Glass Screen (Optional)


BEDROOM :

- 3/4 Single Bed
- Double Room (Family)
- Desk, Chair
- Wardrobe
- Elec Radiator


Price

£ 75,000

Ex Vat.

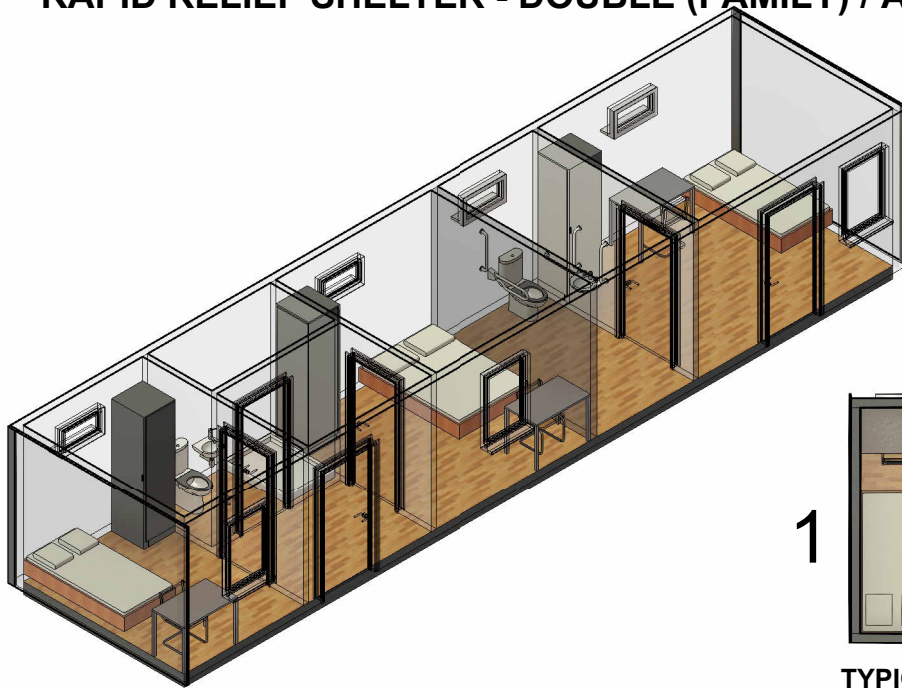

2

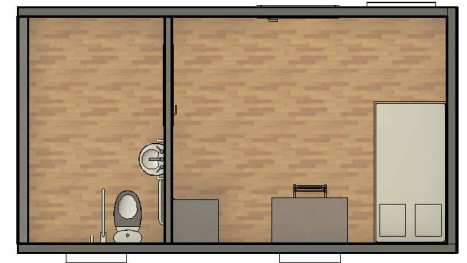


1



TYPICAL BEDROOM LAYOUT

ISOMETRIC VIEW

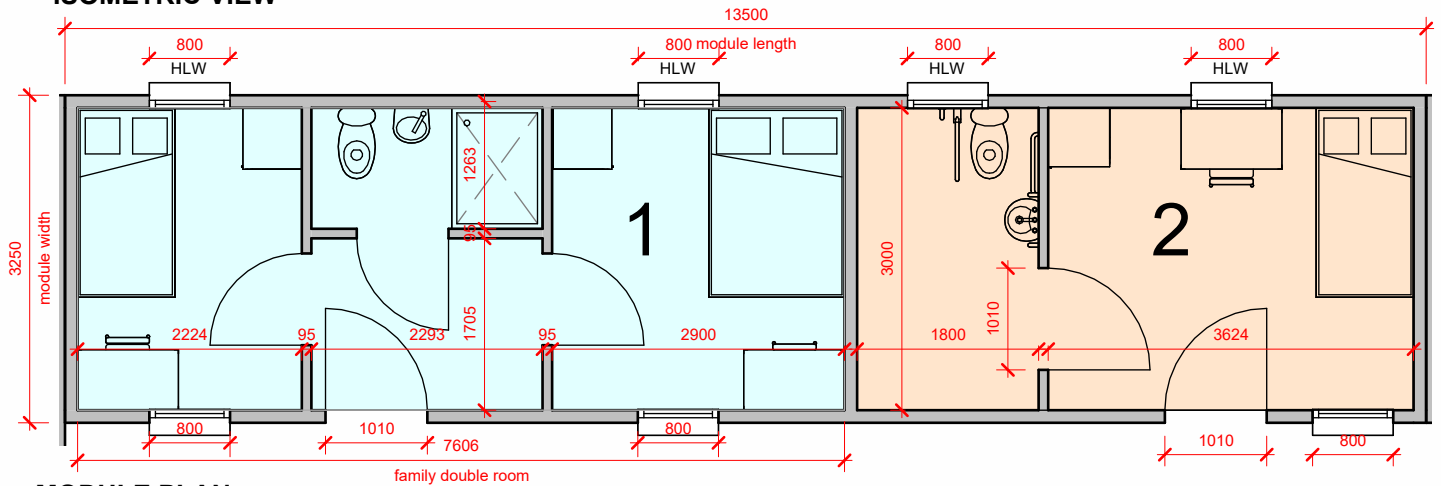

MODULE PLAN

DESCRIPTION

- Insulated walls, floors and ceiling to building Regulation
- Fire compartment - compartmentation exceeds Building Regulations
- Acoustic performance to Building Regulation
- Wifi points for internet connectivity.
- Fully furnished bedroom and shower room
- Separate communal facilities and amenities to promote co-living: such as, Shared kitchen; shared dining/living and laundry can be offered based upon clients spec.
- Standard uPVC Double Glazed windows and doors (Optional PAS24 window and doors)
- Modern Method of Construction are all built off site and quality checked throughout the process in controlled factory environment.
- Fully tested and commissioned pre delivery and final connection
- BOPAS accredited to 60 years lifespan in static location.
- Configure Module design up to 3 storeys – stackable.
- Utility electric, water and waste connection, usage manage with submeter to aid management and monitoring.
- PV panels (Optional)
- Electric heating
- LIGHTING: PIR or Swich

SPECIFICATION

U VALUES OF BUILDING ELEMENTS:

FLOOR - 0.18W/m²K

EXTERNAL WALLS - 0.26W/m²K

ROOF - 0.16W/m²K

WINDOWS - 1.6W/m²K

DOORS - 1.6W/m²K

BUILDING FIRE RATED : (REI 60) EN 1301-2

EXTERNAL WALL CONSTRUCTION:

Rainscreen cladding, design/finish to suit client choice incorporating cavity insulation, JRL Modular propriety wall build up.

FLOOR CONSTRUCTION:

All floors to be constructed to insulated 60 mins fire rated floor.

ROOF CONSTRUCTION:

Roof construction to comprise of structural steel frame overdrawn with 15mm OSB board, on timber firrings to form a 1° pitch, insulation between joist, vapour control layer and 12.5mm plaster board, Single ply water proof membrane. Over all roof build up to achieve u-value of 0.16W/m²K

DOORS AND WINDOWS:

EXTERNAL DOORS:

- Standard uPVC external door with spy hole to achieve u-value of 1.6W/m²K

(PAS24 Door with spy hole) - Optional

INTERNAL DOORS

- 900x2100mm s/o internal door

WINDOWS:

- 800 x 1200mm Standard uPVC Double Glazed ((Argon) Window (4mm thick each pane) - CILL@ 900mm high to achieve u-value of 1.6W/m²K (Window Fire Rated -REI 30)
- 800 x 450mm HLW uPVC Double Glazed Window (4mm thick each pane) - CILL@1650mm high to achieve u-value of 1.6W/m²K

(PAS24 Windows) - Optional

- With 6.8mm thick laminated glass

Low energy lightinh-switched **PIR** optional

TOILET AREA:

WALL FINISHES:

- Polyclad Wall Lining on 9mm ply including shower

CEILING FINISHES:

- Painted white (Anti Moisture paint)

FLOOR FINISHES:

- Polysafe 2mm non slip vinyl

FITTINGS:

WC: Floor mounted toilet pan
900x900mm Square shower tray
Wall hung WHB, Vanity, toilet, robe hook, elec. towel, shaver and elec shower.

SHOWER SCREEN: Shower Curtain
Glass Screen (Optional)

BEDROOM :

- 3/4 Single Bed
- Double Room (Family)
- Desk, Chair
- Wardrobe
- Elec Radiator

Price

£ 70,000


Ex Vat.



ISOMETRIC VIEW



TYPICAL ROOM LAYOUT

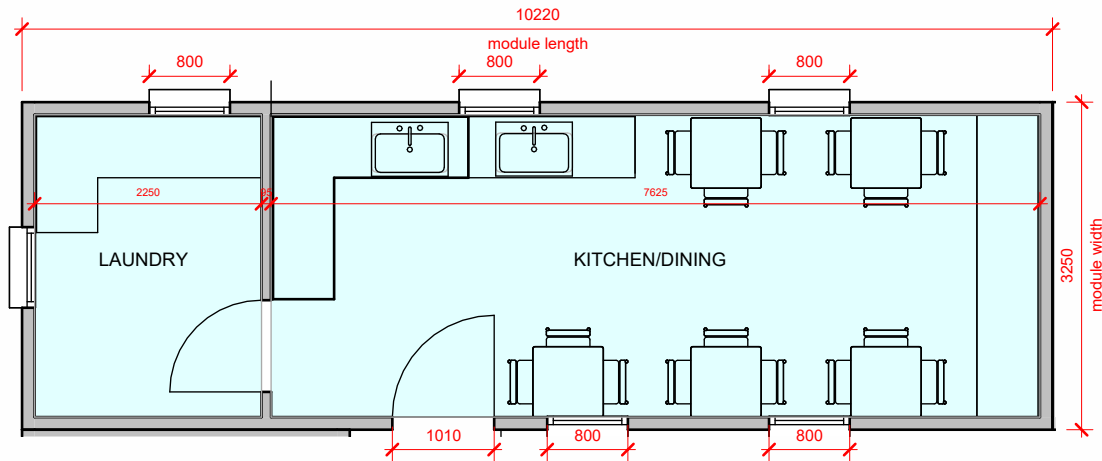

MODULE PLAN

DESCRIPTION

- Insulated walls, floors and ceiling to building Regulation
- Fire compartment - compartmentation exceeds Building Regulations
- Acoustic performance to Building Regulation
- Wifi points for internet connectivity.
- Fully furnished bedroom and shower room
- Separate communal facilities and amenities to promote co-living: such as, Shared kitchen; shared dining/living and laundry can be offered based upon clients spec.
- Standard uPVC Double Glazed windows and doors (Optional PAS24 window and doors)
- Modern Method of Construction are all built off site and quality checked throughout the process in controlled factory environment.
- Fully tested and commissioned pre delivery and final connection
- BOPAS accredited to 60 years lifespan in static location.
- Configure Module design up to 3 storeys – stackable.
- Utility electric, water and waste connection, usage manage with submeter to aid management and monitoring.
- PV panels (Optional)
- Electric heating
- LIGHTING: PIR or Swich

SPECIFICATION

U VALUES OF BUILDING ELEMENTS:

FLOOR - 0.18W/m²K

EXTERNAL WALLS - 0.26W/m²K

ROOF - 0.16W/m²K

WINDOWS - 1.6W/m²K

DOORS - 1.6W/m²K

BUILDING FIRE RATED : (REI 60) EN 1301-2

EXTERNAL WALL CONSTRUCTION:

Rainscreen cladding, design/finish to suit client choice incorporating cavity insulation, JRL Modular propriety wall build up.

FLOOR CONSTRUCTION:

All floors to be constructed to insulated 60 mins fire rated floor.

ROOF CONSTRUCTION:

Roof construction to comprise of structural steel frame overdrawn with 15mm OSB board, on timber firrings to form a 1° pitch, insulation between joist, vapour control layer and 12.5mm plaster board, Single ply water proof membrane. Over all roof build up to achieve u-value of 0.16W/m²K

DOORS AND WINDOWS:

EXTERNAL DOORS:

- Standard uPVC external door with spy hole to achieve u-value of 1.6W/m²K

(PAS24 Door with spy hole) - Optional

INTERNAL DOORS

- 900x2100mm s/o internal door

WINDOWS:

- 800 x 1200mm Standard uPVC Double Glazed ((Argon) Window (4mm thick each pane) - CILL@ 900mm high to achieve u-value of 1.6W/m²K (Window Fire Rated -**REI 30**)
- 800 x 450mm HLW uPVC Double Glazed Window (4mm thick each pane) - CILL@1650mm high to achieve u-value of 1.6W/m²K

(PAS24 Windows) - Optional

- With 6.8mm thick laminated glass

Low energy lightin-h-switched **PIR** optional

TOILET AREA:

WALL FINISHES:

- Polyclad Wall Lining on 9mm ply including shower

CEILING FINISHES:

- Painted white (Anti Moisture paint)

FLOOR FINISHES:

- Polysafe 2mm non slip vinyl

FITTINGS:

WC: Floor mounted toilet pan
900x900mm Square shower tray
Wall hung WHB, Vanity, toilet, robe hook, elec. towel, shaver and elec shower.

SHOWER SCREEN: Shower Curtain
Glass Screen (Optional)

KITCHEN/DINING/LAUNDRY :


- Worktop with 2 sink and 1 Hob
- Laundry work surface prep'd for washer/ dryer

Price

£ 40,000


Ex Vat.

(White Box except Shower room)

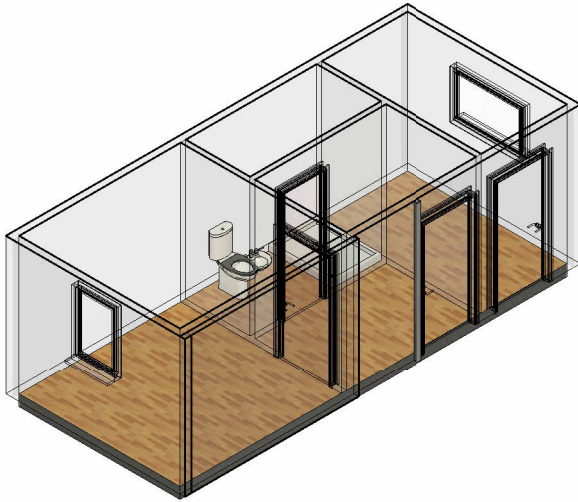

TYPICAL ROOM LAYOUT

ISOMETRIC VIEW

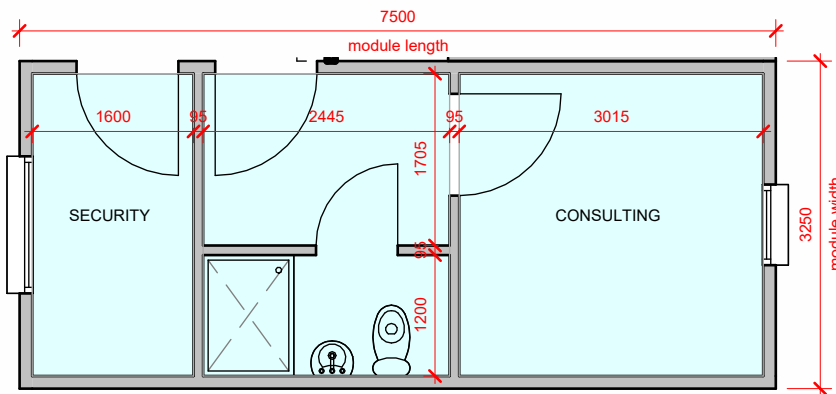

MODULE PLAN

DESCRIPTION

- Insulated walls, floors and ceiling to building Regulation
- Fire compartment - compartmentation exceeds Building Regulations
- Acoustic performance to Building Regulation
- Wifi points for internet connectivity.
- Fully furnished bedroom and shower room
- Separate communal facilities and amenities to promote co-living: such as, Shared kitchen; shared dining/living and laundry can be offered based upon clients spec.
- Standard uPVC Double Glazed windows and doors (Optional PAS24 window and doors)
- Modern Method of Construction are all built off site and quality checked throughout the process in controlled factory environment.
- Fully tested and commissioned pre delivery and final connection
- BOPAS accredited to 60 years lifespan in static location.
- Configure Module design up to 3 storeys – stackable.
- Utility electric, water and waste connection, usage manage with submeter to aid management and monitoring.
- PV panels (Optional)
- Electric heating
- LIGHTING: PIR or Swich

SPECIFICATION

U VALUES OF BUILDING ELEMENTS:

FLOOR - 0.18W/m²K

EXTERNAL WALLS - 0.26W/m²K

ROOF - 0.16W/m²K

WINDOWS - 1.6W/m²K

DOORS - 1.6W/m²K

BUILDING FIRE RATED : (REI 60) EN 1301-2

EXTERNAL WALL CONSTRUCTION:

Rainscreen cladding, design/finish to suit client choice incorporating cavity insulation, JRL Modular propriety wall build up.

FLOOR CONSTRUCTION:

All floors to be constructed to insulated 60 mins fire rated floor.

ROOF CONSTRUCTION:

Roof construction to comprise of structural steel frame overdrawn with 15mm OSB board, on timber firrings to form a 1° pitch, insulation between joist, vapour control layer and 12.5mm plaster board, Single ply water proof membrane. Over all roof build up to achieve u-value of 0.16W/m²K

DOORS AND WINDOWS:

EXTERNAL DOORS:

- Standard uPVC external door with spy hole to achieve u-value of 1.6W/m²K

(PAS24 Door with spy hole) - Optional

INTERNAL DOORS

- 900x2100mm s/o internal door

WINDOWS:

- 800 x 1200mm Standard uPVC Double Glazed ((Argon) Window (4mm thick each pane) - CILL@ 900mm high to achieve u-value of 1.6W/m²K (Window Fire Rated -REI 30)
- 800 x 450mm HLW uPVC Double Glazed Window (4mm thick each pane) - CILL@1650mm high to achieve u-value of 1.6W/m²K

(PAS24 Windows) - Optional

- With 6.8mm thick laminated glass

Low energy lightinh-switched **PIR** optional

TOILET AREA:

WALL FINISHES:

- Polyclad Wall Lining on 9mm ply including shower

CEILING FINISHES:

- Painted white (Anti Moisture paint)

FLOOR FINISHES:

- Polysafe 2mm non slip vinyl

FITTINGS:

WC: Floor mounted toilet pan
900x900mm Square shower tray
Wall hung WHB, Vanity, toilet, robe hook, elec. towel, shaver and elec shower.

SHOWER SCREEN: Shower Curtain
Glass Screen (Optional)

BEDROOM :

- 3/4 Single Bed
- Double Room (Family)
- Desk, Chair
- Wardrobe
- Elec Radiator


Price

£ 50,000


Ex Vat.



ISOMETRIC VIEW

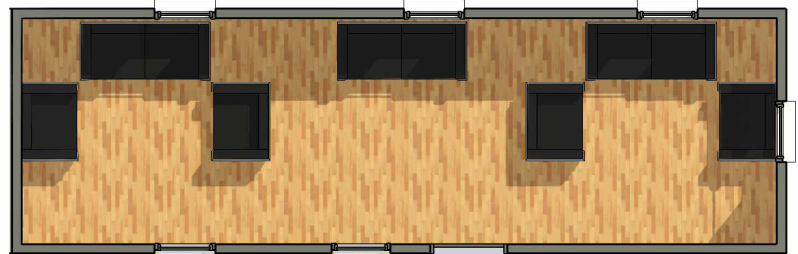

TYPICAL ROOM LAYOUT

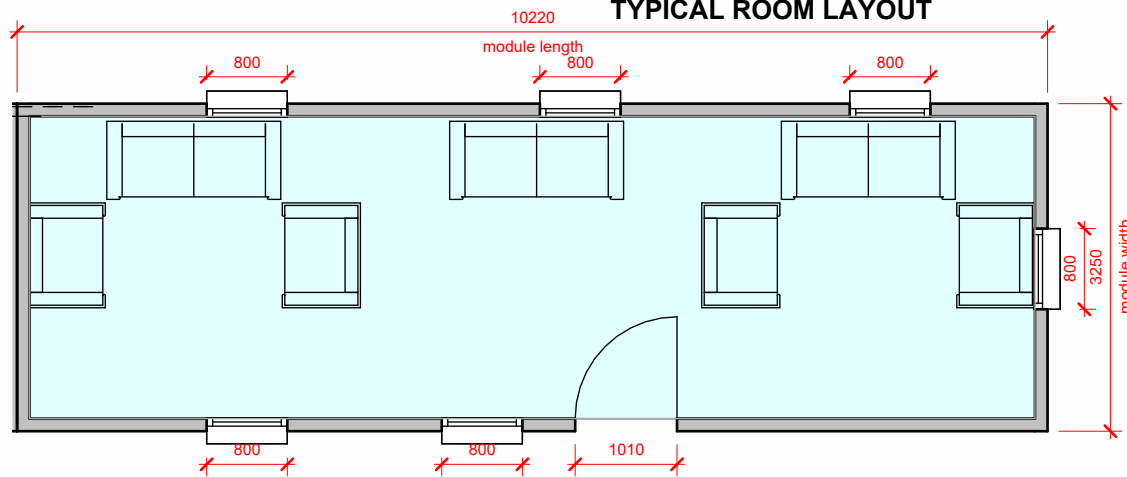

MODULE PLAN

DESCRIPTION

- Insulated walls, floors and ceiling to building Regulation
- Fire compartment - compartmentation exceeds Building Regulations
- Acoustic performance to Building Regulation
- Wifi points for internet connectivity.
- Fully furnished bedroom and shower room
- Separate communal facilities and amenities to promote co-living: such as, Shared kitchen; shared dining/living and laundry can be offered based upon clients spec.
- Standard uPVC Double Glazed windows and doors (Optional PAS24 window and doors)
- Modern Method of Construction are all built off site and quality checked throughout the process in controlled factory environment.
- Fully tested and commissioned pre delivery and final connection
- BOPAS accredited to 60 years lifespan in static location.
- Configure Module design up to 3 storeys – stackable.
- Utility electric, water and waste connection, usage manage with submeter to aid management and monitoring.
- PV panels (Optional)
- Electric heating
- LIGHTING: PIR or Swich

SPECIFICATION

U VALUES OF BUILDING ELEMENTS:

FLOOR - 0.18W/m²K

EXTERNAL WALLS - 0.26W/m²K

ROOF - 0.16W/m²K

WINDOWS - 1.6W/m²K

DOORS - 1.6W/m²K

BUILDING FIRE RATED : (REI 60) EN 1301-2

EXTERNAL WALL CONSTRUCTION:

Rainscreen cladding, design/finish to suit client choice incorporating cavity insulation, JRL Modular propriety wall build up.

FLOOR CONSTRUCTION:

All floors to be constructed to insulated 60 mins fire rated floor.

ROOF CONSTRUCTION:

Roof construction to comprise of structural steel frame overdrawn with 15mm OSB board, on timber firrings to form a 1° pitch, insulation between joist, vapour control layer and 12.5mm plaster board, Single ply water proof membrane. Over all roof build up to achieve u-value of 0.16W/m²K

DOORS AND WINDOWS:

EXTERNAL DOORS:

- Standard uPVC external door with spy hole to achieve u-value of 1.6W/m²K

(PAS24 Door with spy hole) - Optional

INTERNAL DOORS

- 900x2100mm s/o internal door

WINDOWS:

- 800 x 1200mm Standard uPVC Double Glazed ((Argon) Window (4mm thick each pane) - CILL@ 900mm high to achieve u-value of 1.6W/m²K (Window Fire Rated -REI 30)
- 800 x 450mm HLW uPVC Double Glazed Window (4mm thick each pane) - CILL@1650mm high to achieve u-value of 1.6W/m²K

(PAS24 Windows) - Optional

- With 6.8mm thick laminated glass

Low energy lightinh-switched **PIR** optional

TOILET AREA:

WALL FINISHES:

- Polyclad Wall Lining on 9mm ply including shower

CEILING FINISHES:

- Painted white (Anti Moisture paint)

FLOOR FINISHES:

- Polysafe 2mm non slip vinyl

FITTINGS:

WC: Floor mounted toilet pan
900x900mm Square shower tray
Wall hung WHB, Vanity, toilet, robe hook, elec. towel, shaver and elec shower.

SHOWER SCREEN: Shower Curtain
Glass Screen (Optional)

BEDROOM :

- 3/4 Single Bed
- Double Room (Family)
- Desk, Chair
- Wardrobe
- Elec Radiator

Price

£ 40,000

Ex Vat.