



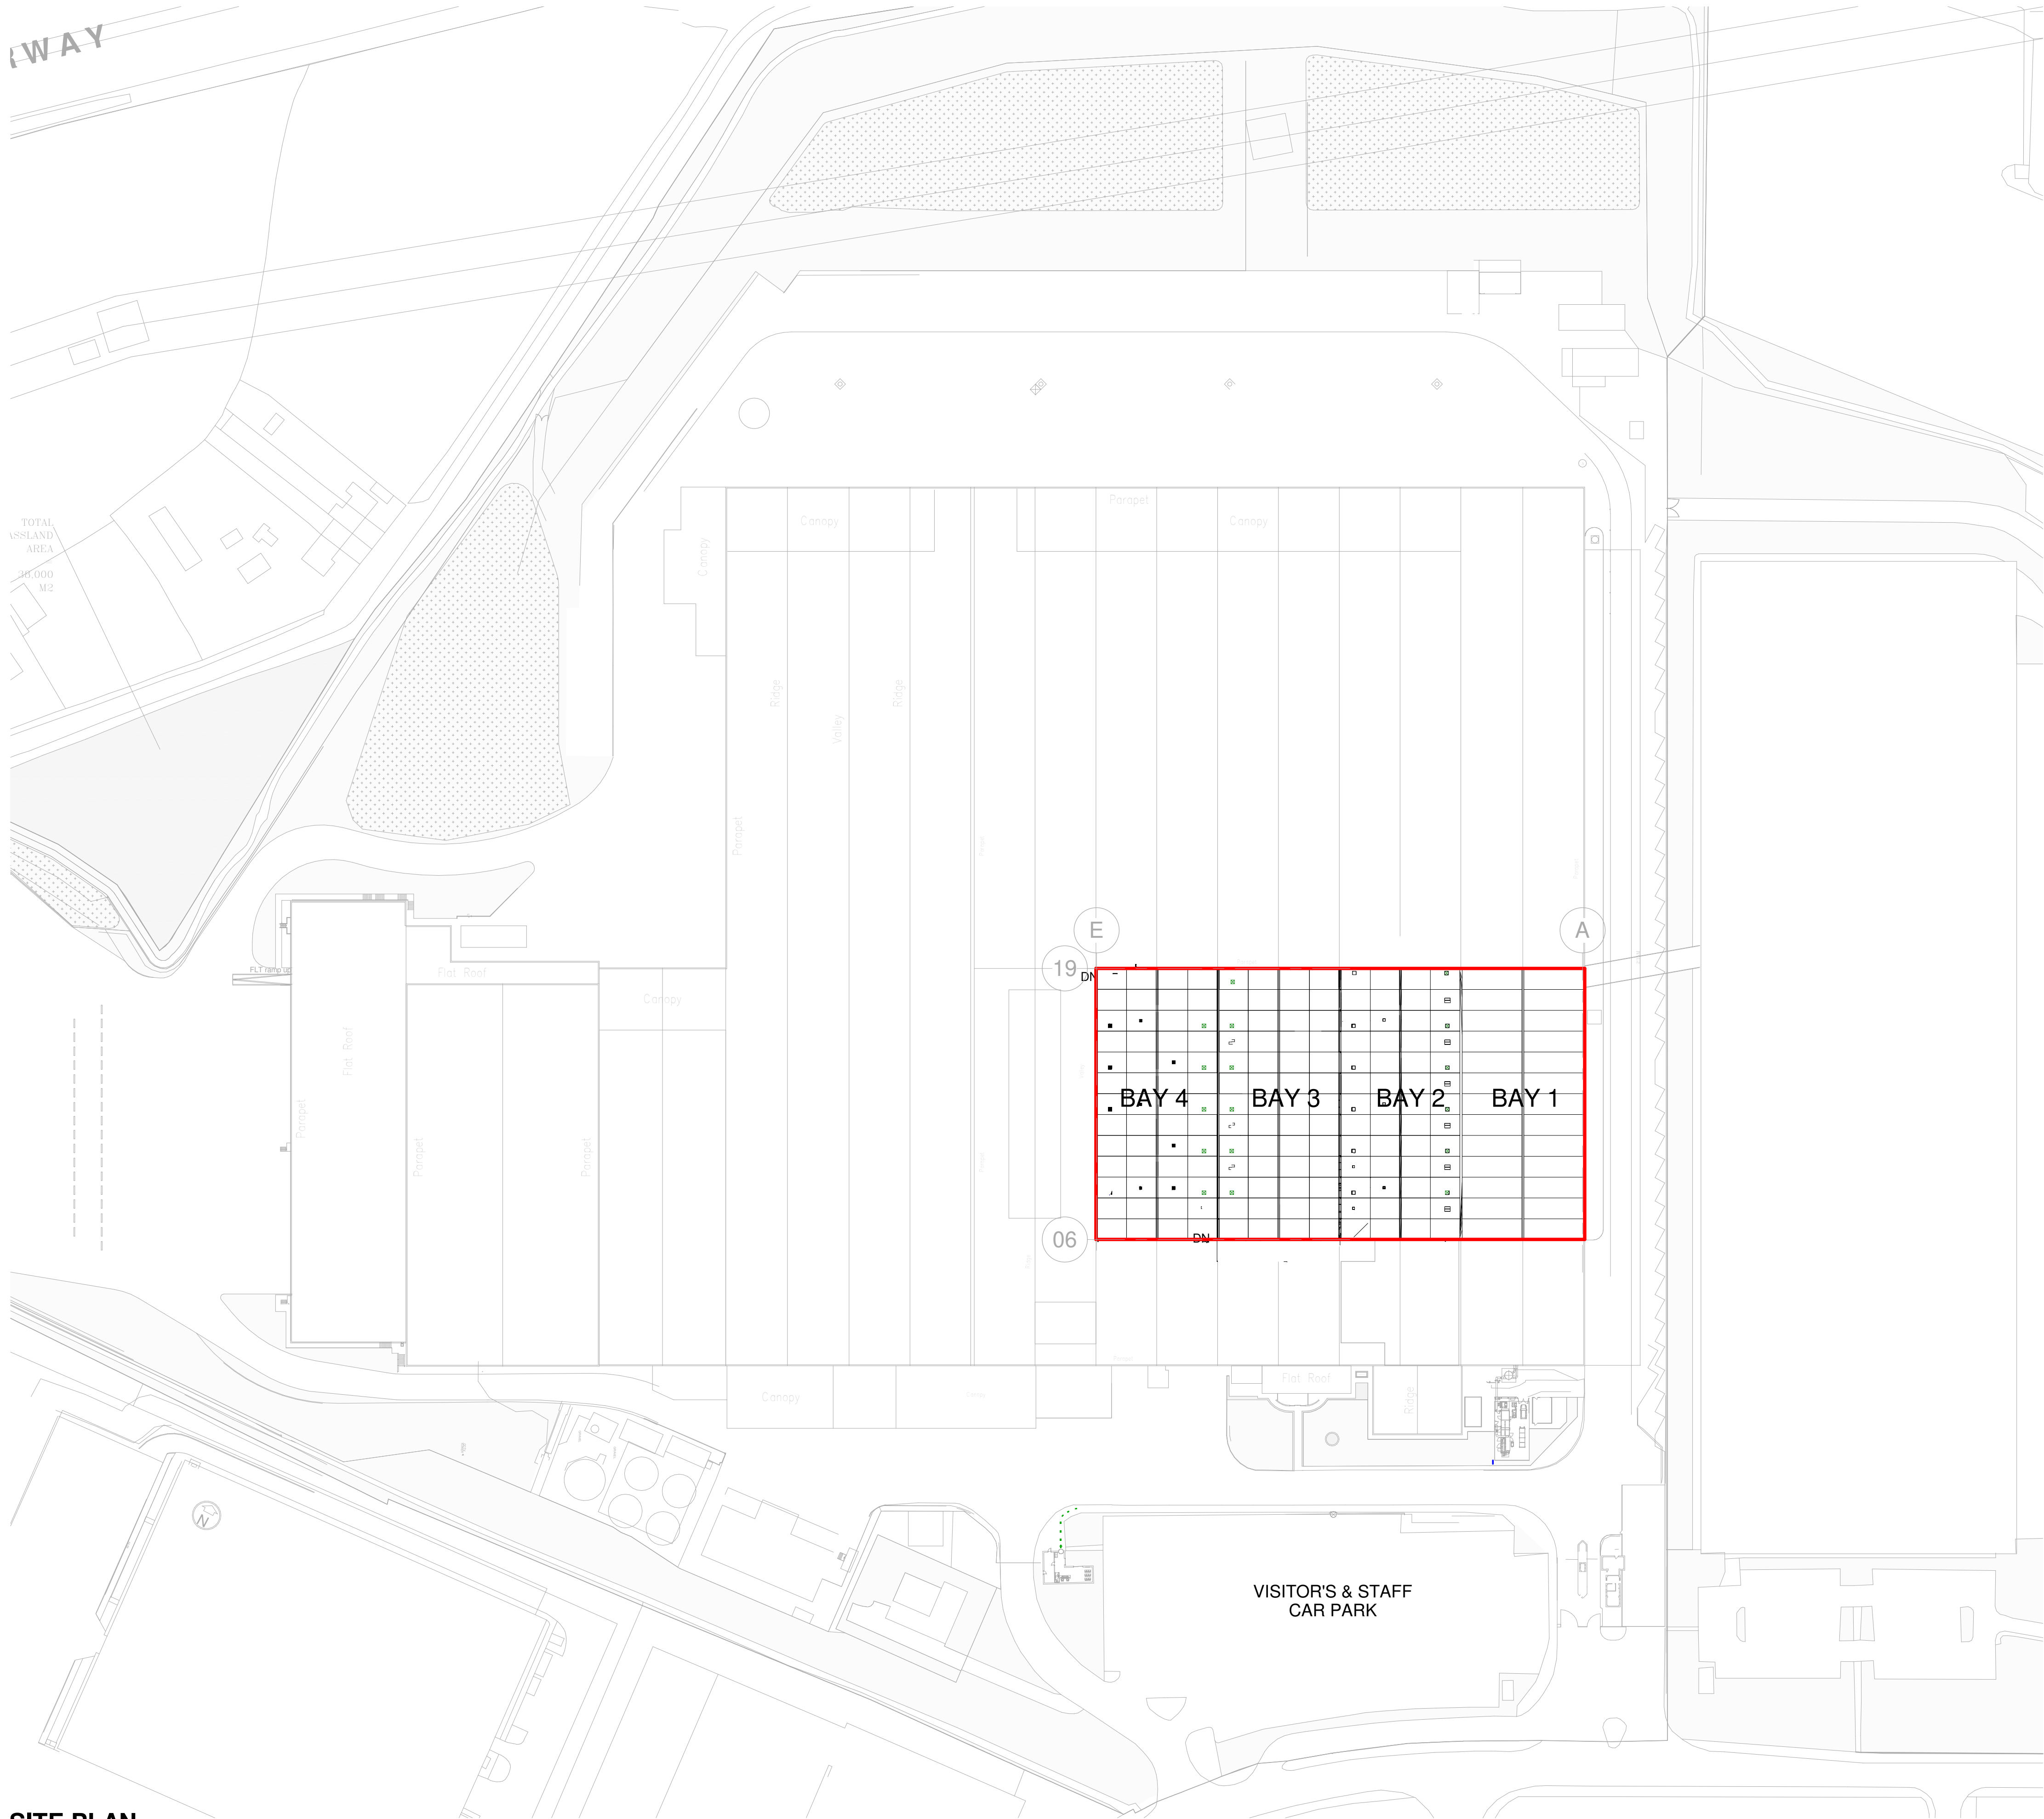

SITE PLAN
1 : 1000

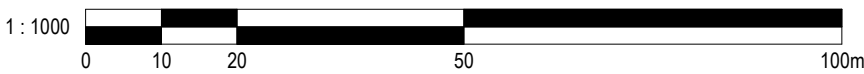

NOTE:

DO NOT SCALE FROM THIS DRAWING
VERIFY ALL DIMENSIONS AND SETTING OUT ON-SITE
NOTIFY ANY DISCREPANCIES TO THE ARCHITECT.
FOR STRUCTURAL INFORMATION, REFER TO
STRUCTURAL ENGINEERS DRAWINGS.
FOR M&E INFORMATION, REFER TO M&E ENGINEER'S
AND SUB-CONTRACTOR'S DRAWINGS.
FOR HEALTH & SAFETY INFORMATION, REFER TO
HEALTH & SAFETY RISK ASSESSMENTS.

NOTE:

A MEASURED SURVEY HAS NOT YET BEEN
UNDERTAKEN ON THIS BUILDING, AND THESE
DRAWINGS HAVE BEEN PRODUCED BASED ON
EXISTING DRAWING INFORMATION PROVIDED BY CCE.

PLEASE DO NOT SCALE FROM THIS DRAWING.

1	29.04.22	Tender Issue	PN	LH
Rev	Date	Description	By	Chk

TENDER

DB3

LEEDS

10 South Parade, Leeds, LS1 5QS
Tel: 0113 244 2931 www.darntonb3.com

CLIENT
COCA-COLA EUROPEAN PARTNERS

PROJECT
CCEP WALK-ON CEILING

TITLE
SITE PLAN

CREATION DATE	SCALE (@ A1)	DRN	CHK	STATUS
29 APR 2022	As Indicated	PN	LH	


SHEET NO.	REVISION
13656 - DB3 - B04 - 00 - DR - A - 90001	1

PROJECT NO (ORIGINATOR) ZONE LEVEL TYPE (ROLE) NUMBER

© COPYRIGHT: ALL RIGHTS RESERVED.
THIS DOCUMENT MUST BE KEPT IN CONJUNCTION WITH ALL OTHER RELEVANT DRAWINGS AND INFORMATION
AND NO PARTS OF IT MAY BE REPRODUCED OR TRANSMITTED IN ANY FORM OR BY ANY MEANS WITHOUT THE
WRITTEN PERMISSION OF DARNTON B3.


DO NOT SCALE OFF DRAWINGS. USE DISPLAYED DIMENSIONS.

PLOT DATE: 10/04/2022 15:38:51

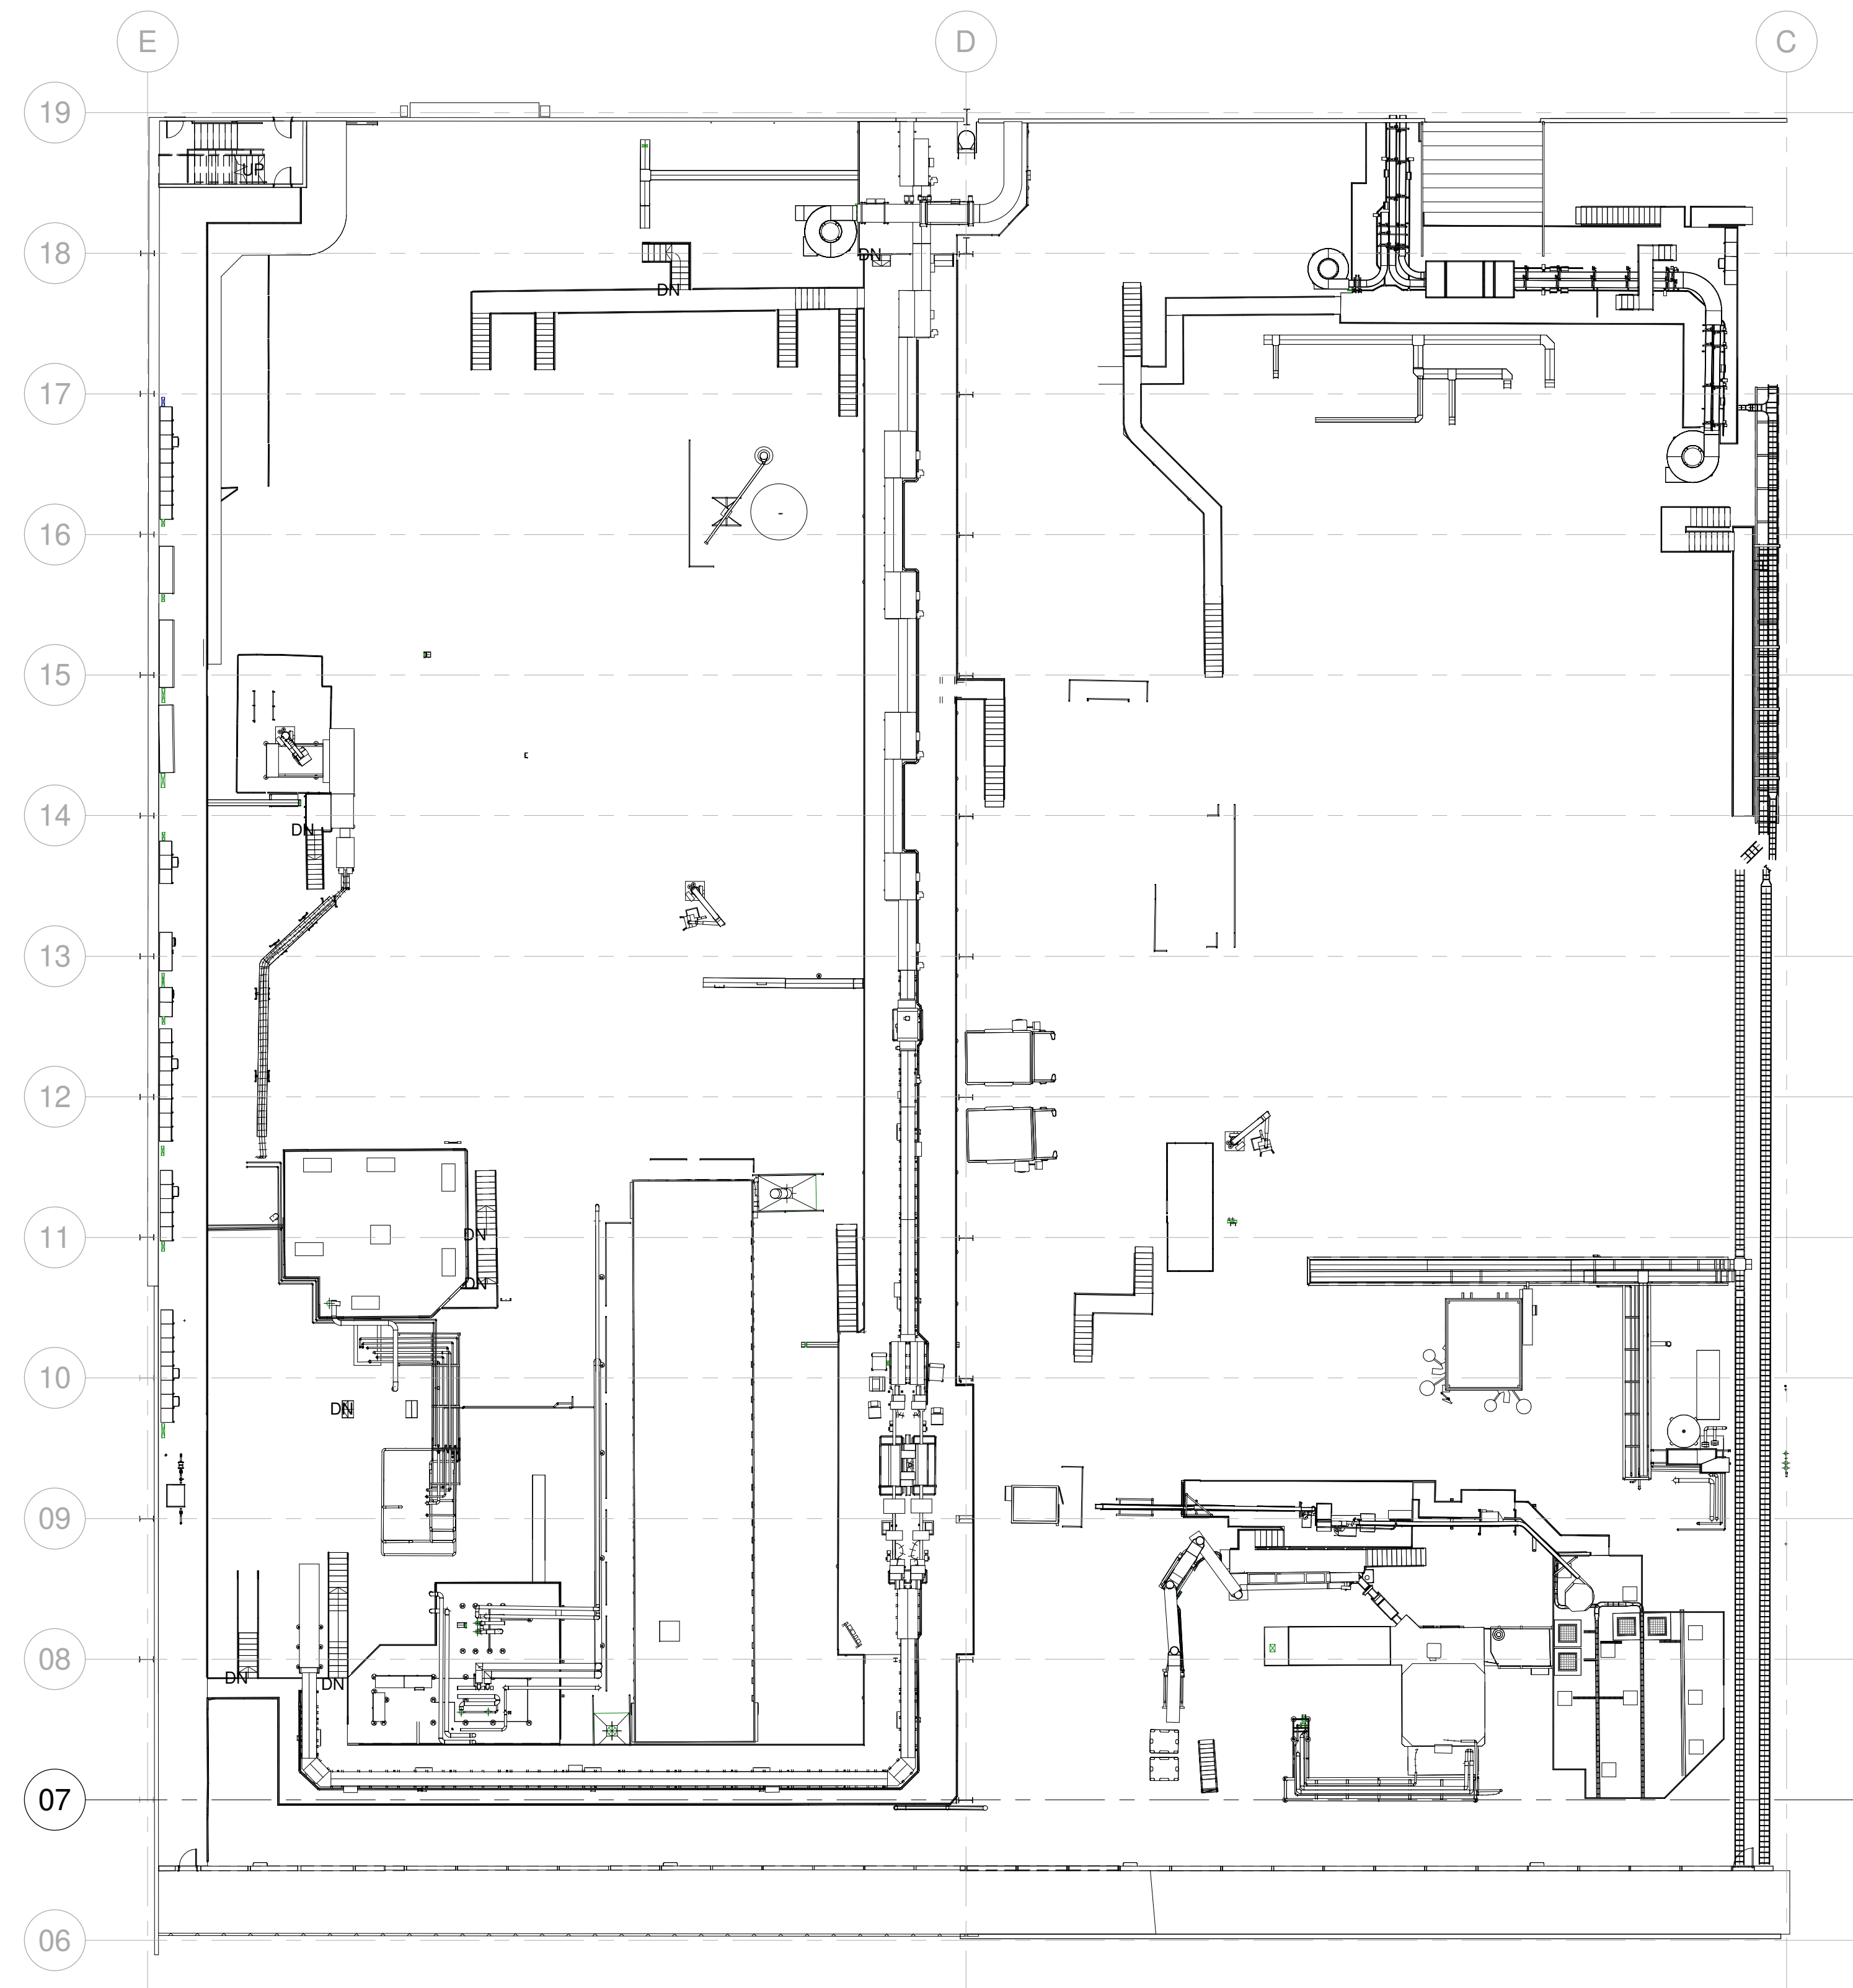

BAY 3 & 4 EXISTING GROUND FLOOR WALKWAYS

1 : 200

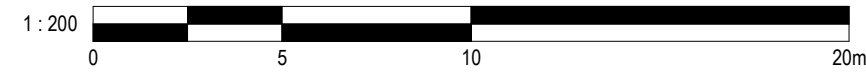

NOTE:

DO NOT SCALE FROM THIS DRAWING
VERIFY ALL DIMENSIONS AND SETTING OUT ON-SITE
NOTIFY ANY DISCREPANCIES TO THE ARCHITECT.
FOR STRUCTURAL INFORMATION, REFER TO
STRUCTURAL ENGINEERS DRAWINGS.
FOR M&E INFORMATION, REFER TO M&E ENGINEER'S
AND SUB-CONTRACTOR'S DRAWINGS.
FOR HEALTH & SAFETY INFORMATION, REFER TO
HEALTH & SAFETY RISK ASSESSMENTS.


NOTE:

A MEASURED SURVEY HAS NOT YET BEEN
UNDERTAKEN ON THIS BUILDING, AND THESE
DRAWINGS HAVE BEEN PRODUCED BASED ON
EXISTING DRAWING INFORMATION PROVIDED BY CCE.

PLEASE DO NOT SCALE FROM THIS DRAWING.

1	29.04.22	Tender Issue	PN	LH
Rev	Date	Description	By	Chk

TENDER

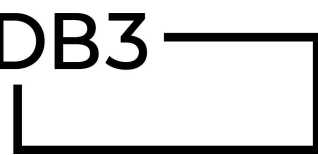

LEEDS

10 South Parade, Leeds, LS1 5QS
Tel: 0113 244 2931 www.darntonb3.com

CLIENT

COCA-COLA EUROPEAN PARTNERS

PROJECT

CCEP WALK-ON CEILING


TITLE

BAY 3 & 4 EXISTING GROUND FLOOR
WALKWAYS GENERAL ARRANGEMENT

CREATION DATE	SCALE @ A1	DRN	CHK	STATUS
29 APR 2022	As indicated	PN	LH	

SHEET NO.	REVISION
13656 - DB3 - B04 - 01 - DR - A - 20005	1

© COPYRIGHT: ALL RIGHTS RESERVED.
THIS DOCUMENT MUST BE KEPT IN CONFIDENTIALITY WITH ALL OTHER RELEVANT DRAWINGS AND INFORMATION
AND NO INFORMATION MUST BE REPORTED TO ANY OTHER ORGANISATION.
ANY INFORMATION OR INFORMATION MUST NOT BE USED FOR CONSTRUCTION UNLESS EXPRESSLY ISSUED FOR
CONSTRUCTION.
DO NOT SCALE OFF DRAWINGS. USE DISPLAYED DIMENSIONS.
PLOT DATE: 29/04/2022 14:45:02

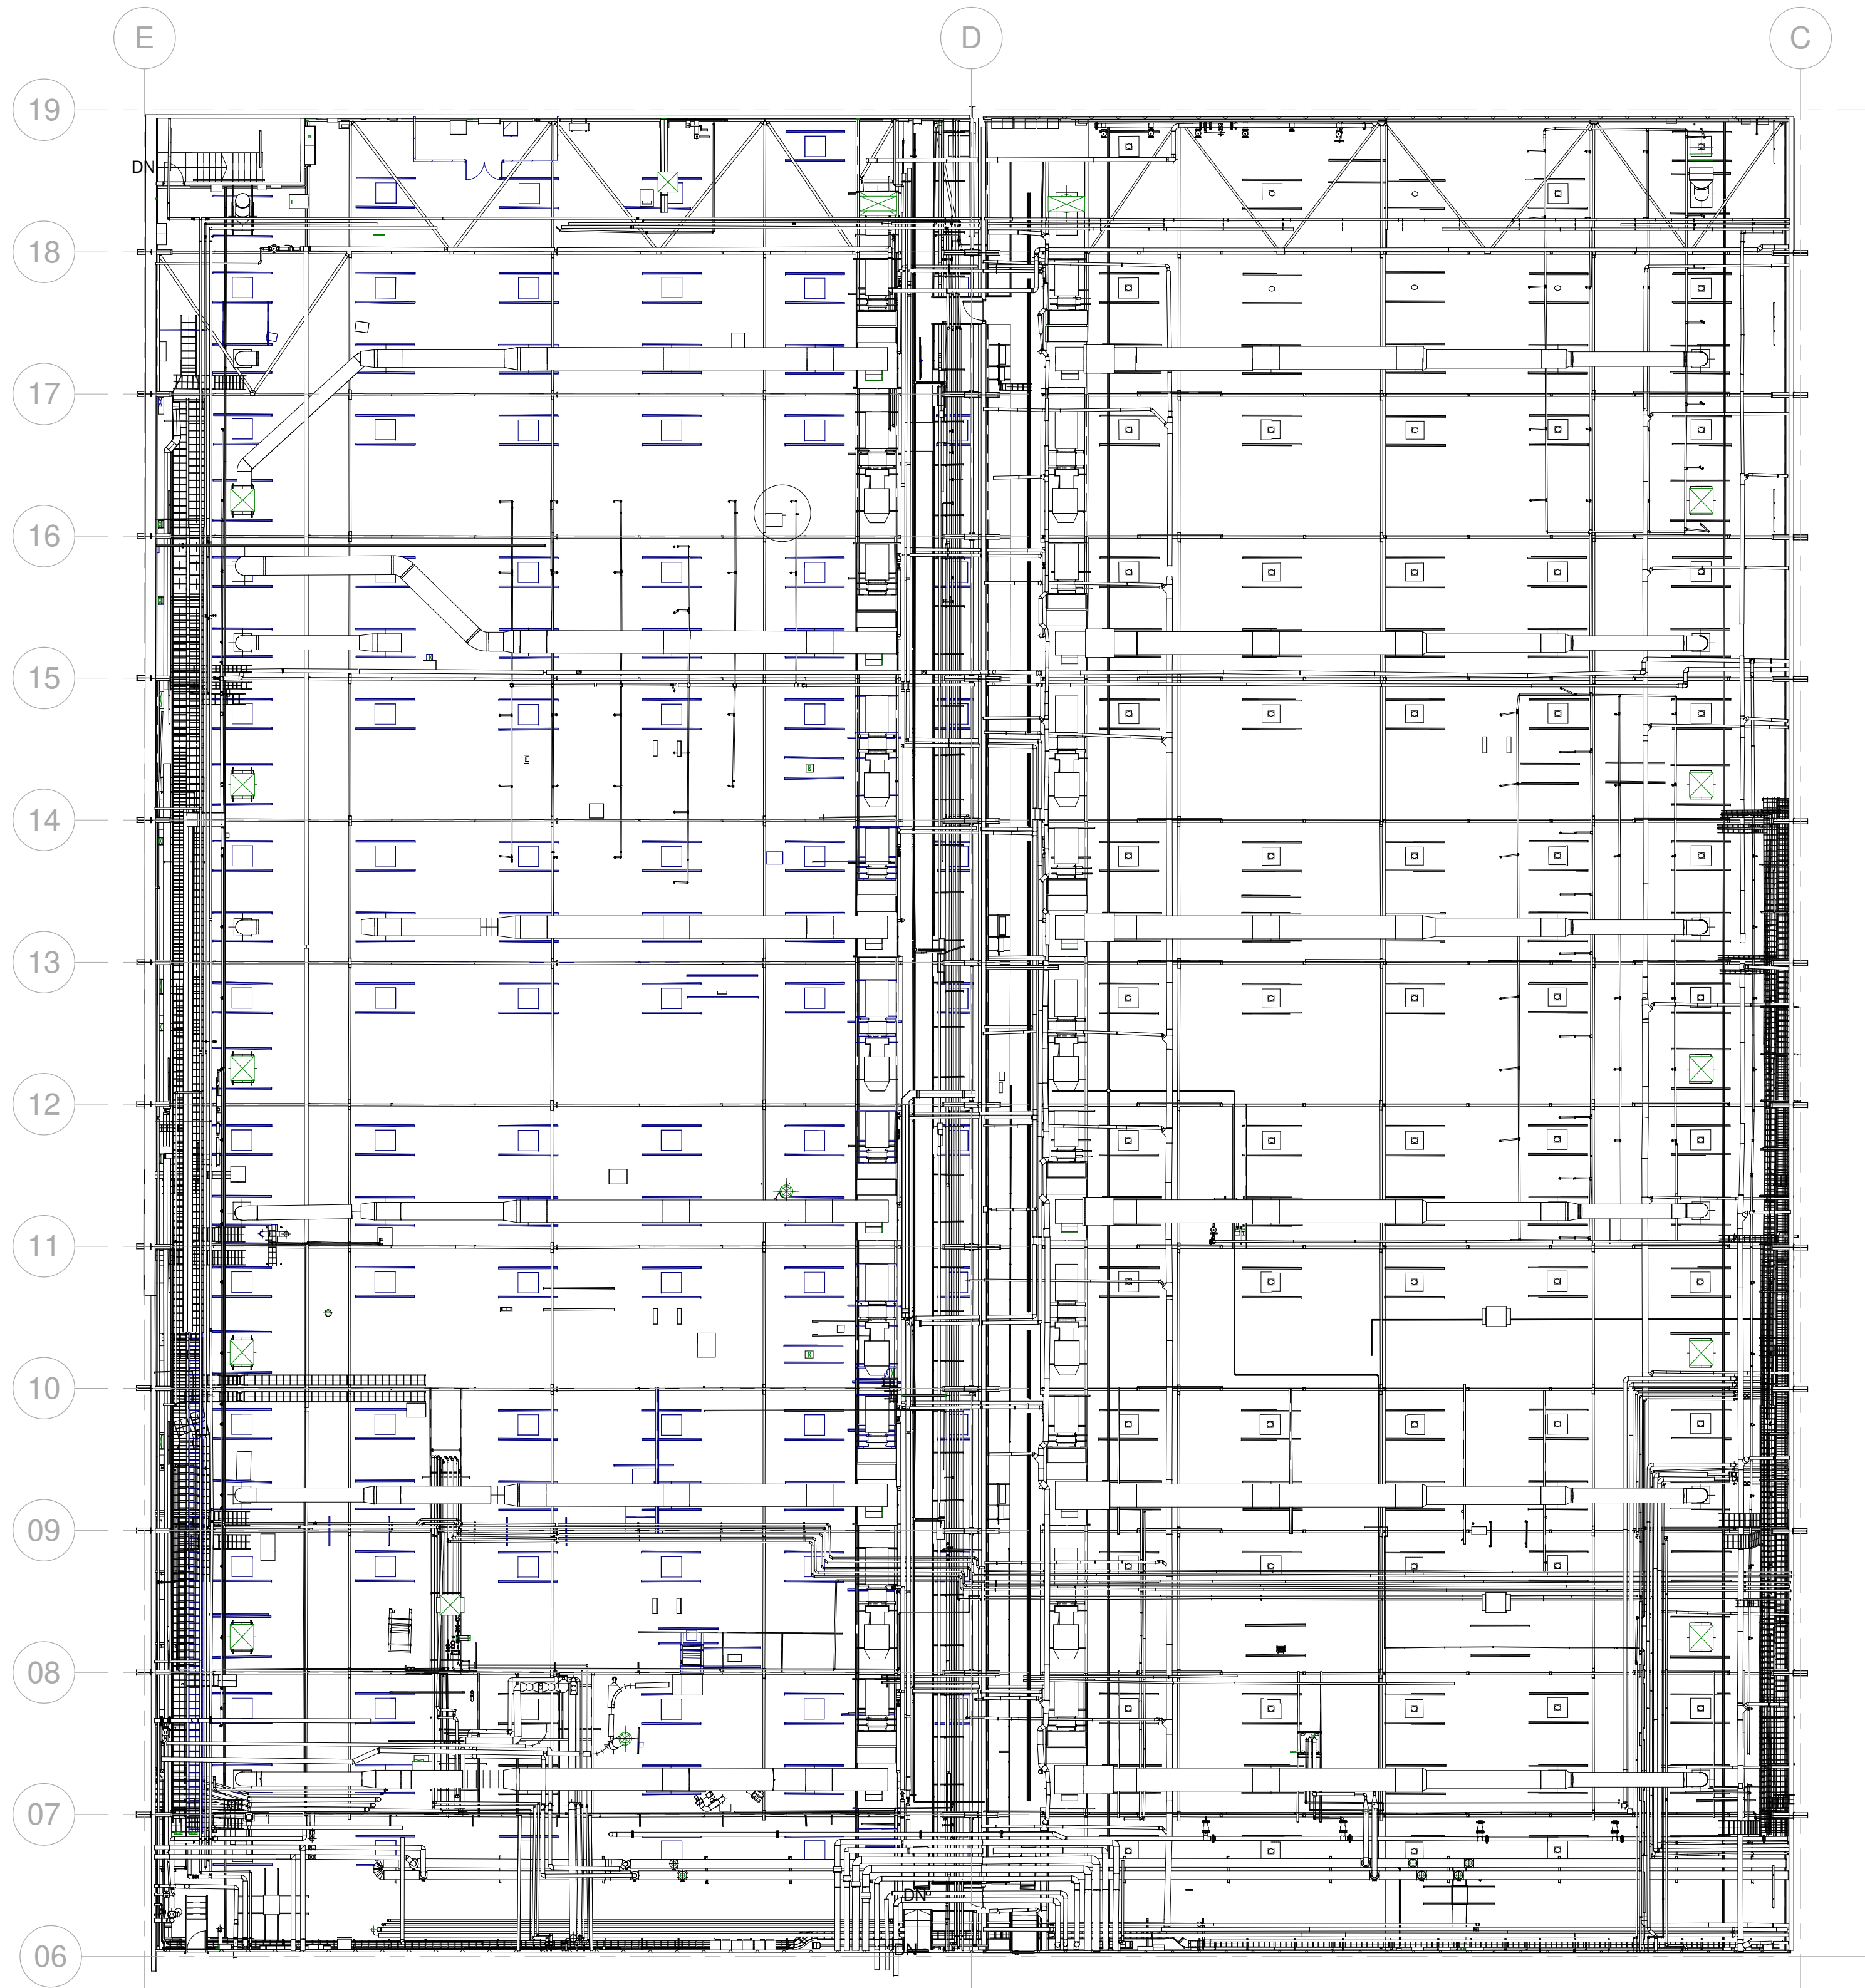

EXISTING WALK-ON CEILING PLAN - BAY 3 & 4

1 : 200



NOTE:

DO NOT SCALE FROM THIS DRAWING.
VERIFY ALL DIMENSIONS AND SETTING OUT ON-SITE.
NOTIFY ANY DISCREPANCIES TO THE ARCHITECT.
FOR STRUCTURAL INFORMATION, REFER TO
STRUCTURAL ENGINEERS DRAWINGS.
FOR M&E INFORMATION, REFER TO M&E ENGINEER'S
AND SUB-CONTRACTOR'S DRAWINGS.
FOR HEALTH & SAFETY INFORMATION, REFER TO
HEALTH & SAFETY RISK ASSESSMENTS.


NOTE:

A MEASURED SURVEY HAS NOT YET BEEN
UNDERTAKEN ON THIS BUILDING, AND THESE
DRAWINGS HAVE BEEN PRODUCED BASED ON
EXISTING DRAWING INFORMATION PROVIDED BY CCE.

PLEASE DO NOT SCALE FROM THIS DRAWING.

1	29.04.22	Tender Issue	PN	LH
Rev	Date	Description	By	Chk

TENDER

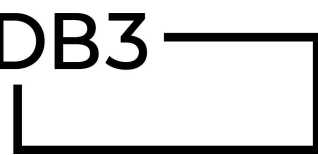

LEEDS

10 South Parade, Leeds, LS1 5QS
Tel: 0113 244 2931 www.darntonb3.com

CLIENT

COCA-COLA EUROPEAN PARTNERS

PROJECT

CCEP WALK-ON CEILING

TITLE

BAY 3 & 4 EXISTING GA WALK ON CEILING
PLAN

CREATION DATE	SCALE @ A1	DRN	CHK	STATUS
29 APR 2022	As indicated	PN	LH	


SHEET NO.	REVISION
13656 - DB3 - B04 - 02 - DR - A - 20004	1

PROJECT NO|ORIGINATOR|ZONE|LEVEL|TYPE|ROLE|NUMBER



© COPYRIGHT: ALL RIGHTS RESERVED.
THIS DOCUMENT MUST BE KEPT IN CONFIDENTIALITY WITH ALL OTHER RELEVANT DRAWINGS AND INFORMATION.
ANY DISCREPANCY MUST BE REPORTED TO THE ARCHITECT IMMEDIATELY.
THIS DOCUMENT IS NOT TO BE USED FOR CONSTRUCTION UNLESS EXPRESSLY ISSUED BY THE ARCHITECT.

DO NOT SCALE OFF DRAWINGS. USE DISPLAYED DIMENSIONS.



PLOT DATE: 10/04/2022 12:29:30

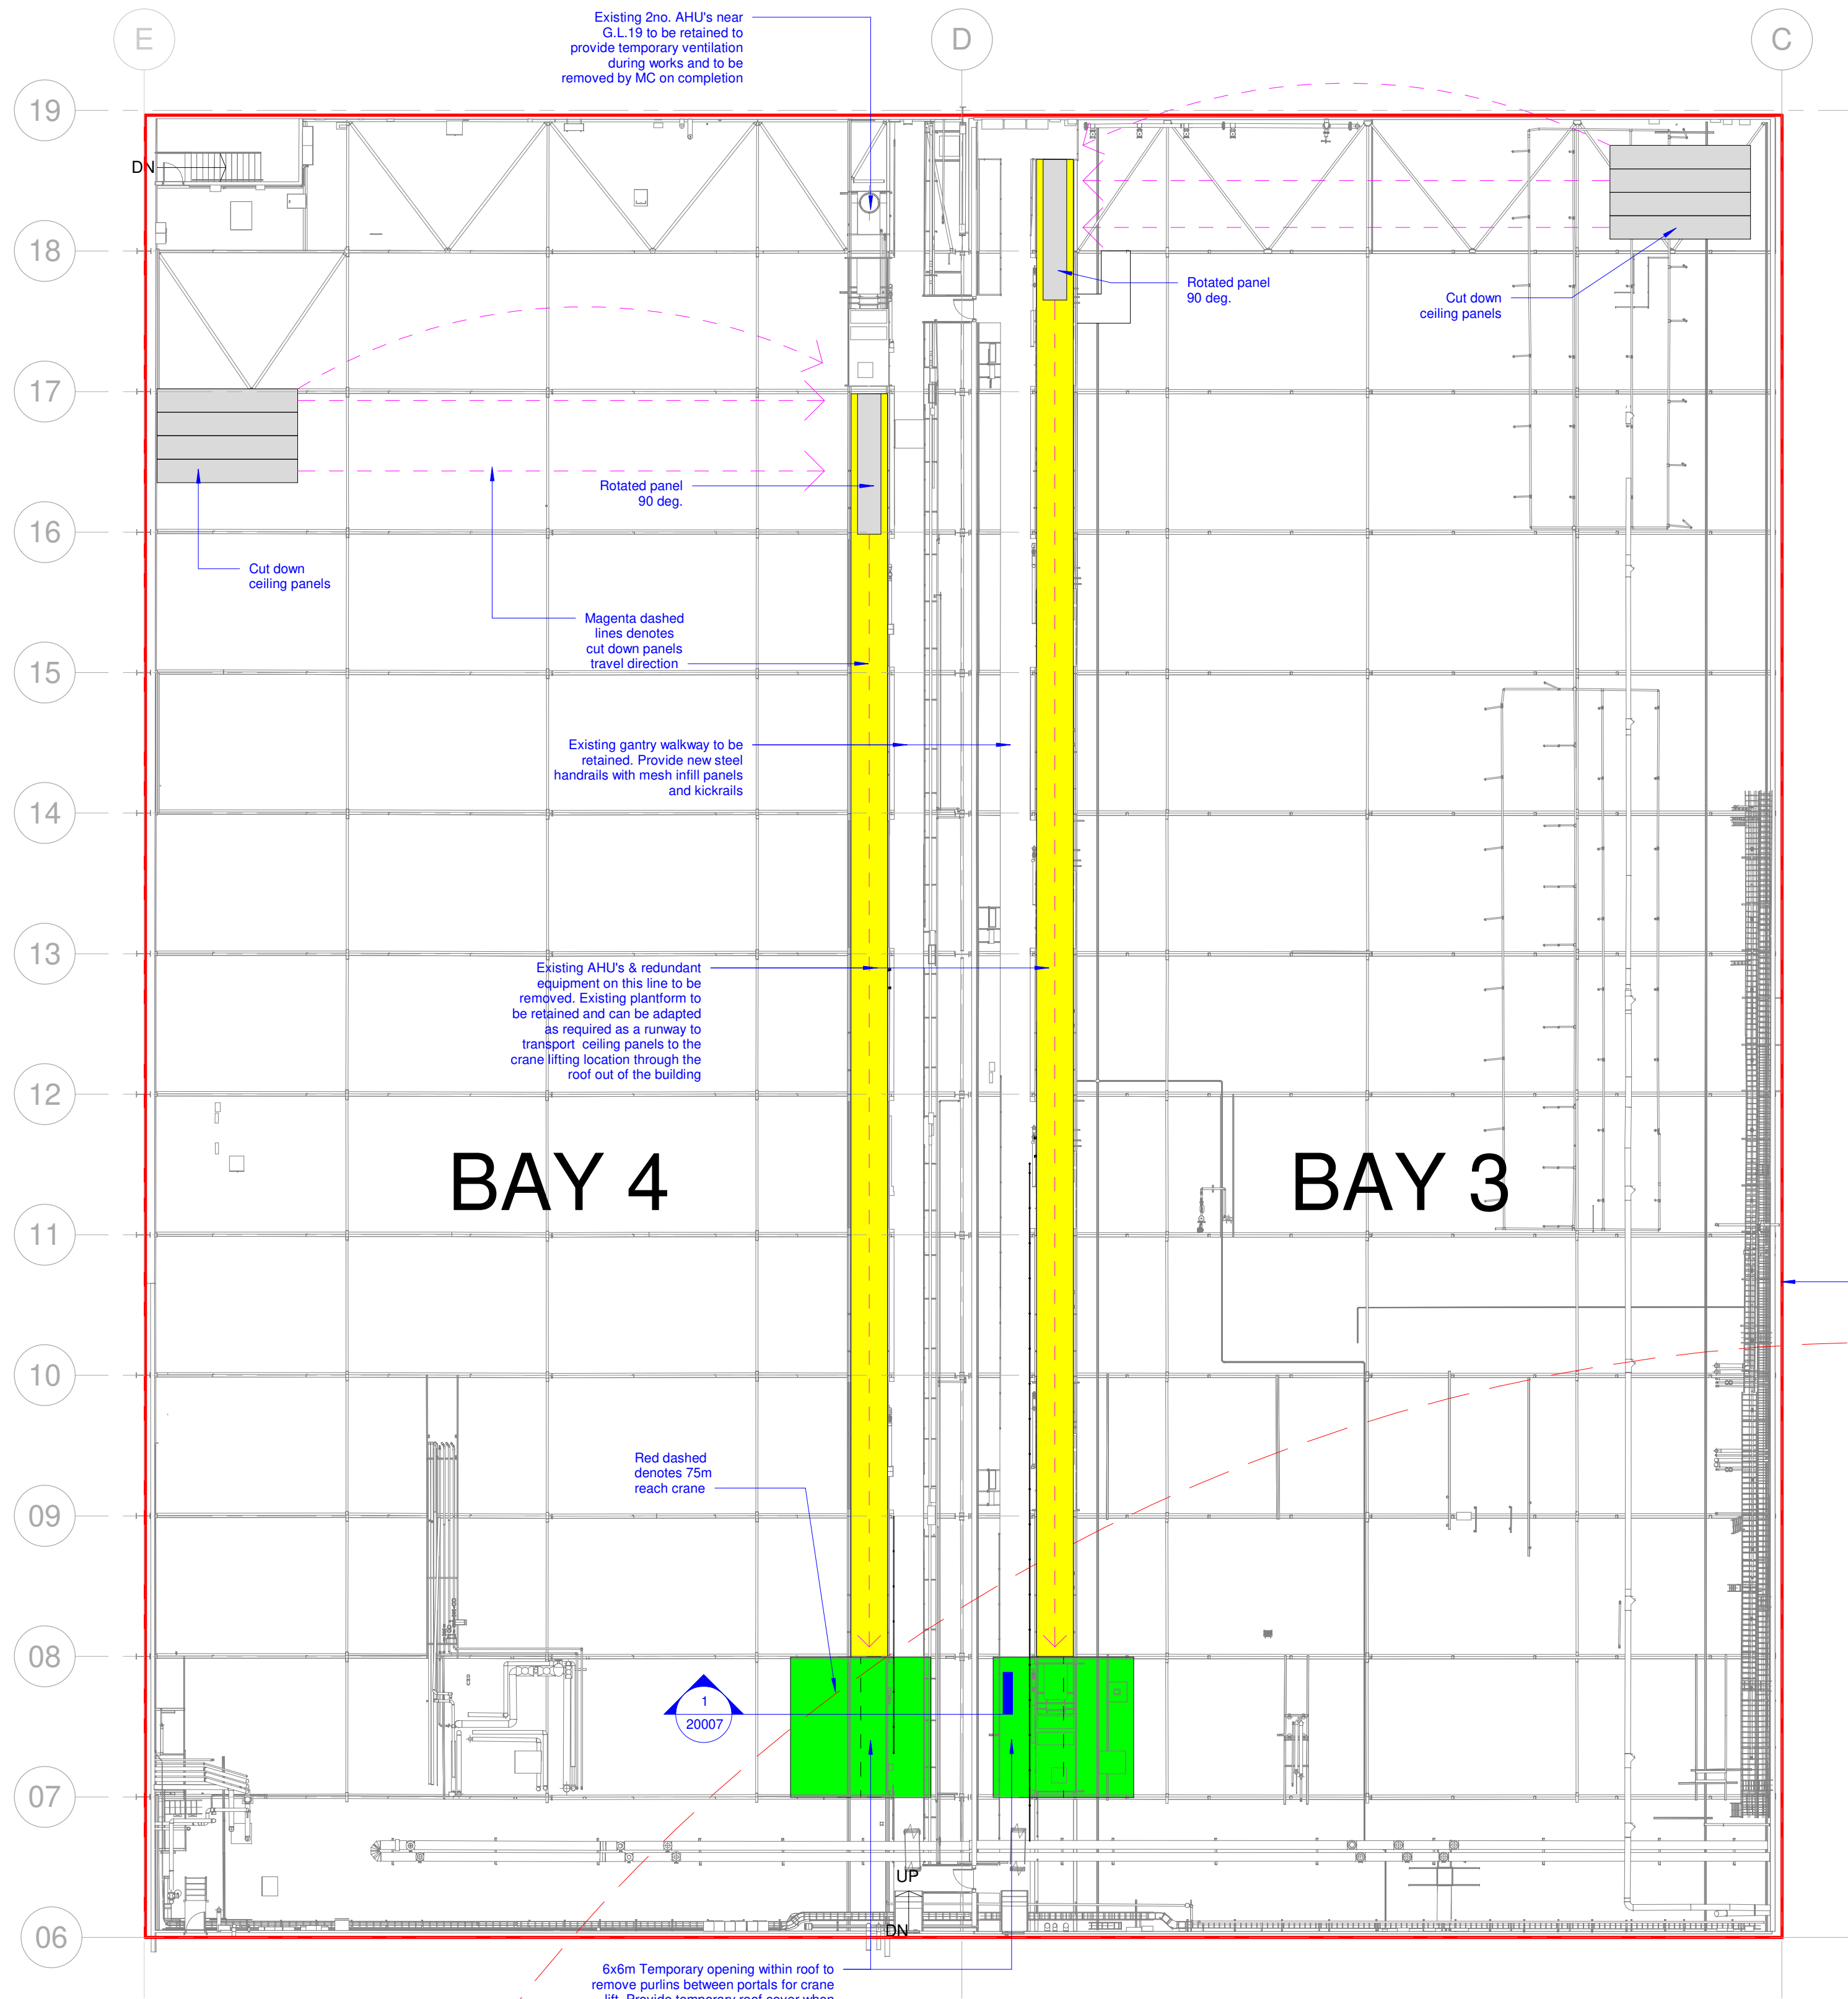


BAY 3 & 4 PROPOSED CEILING REMOVAL PLAN

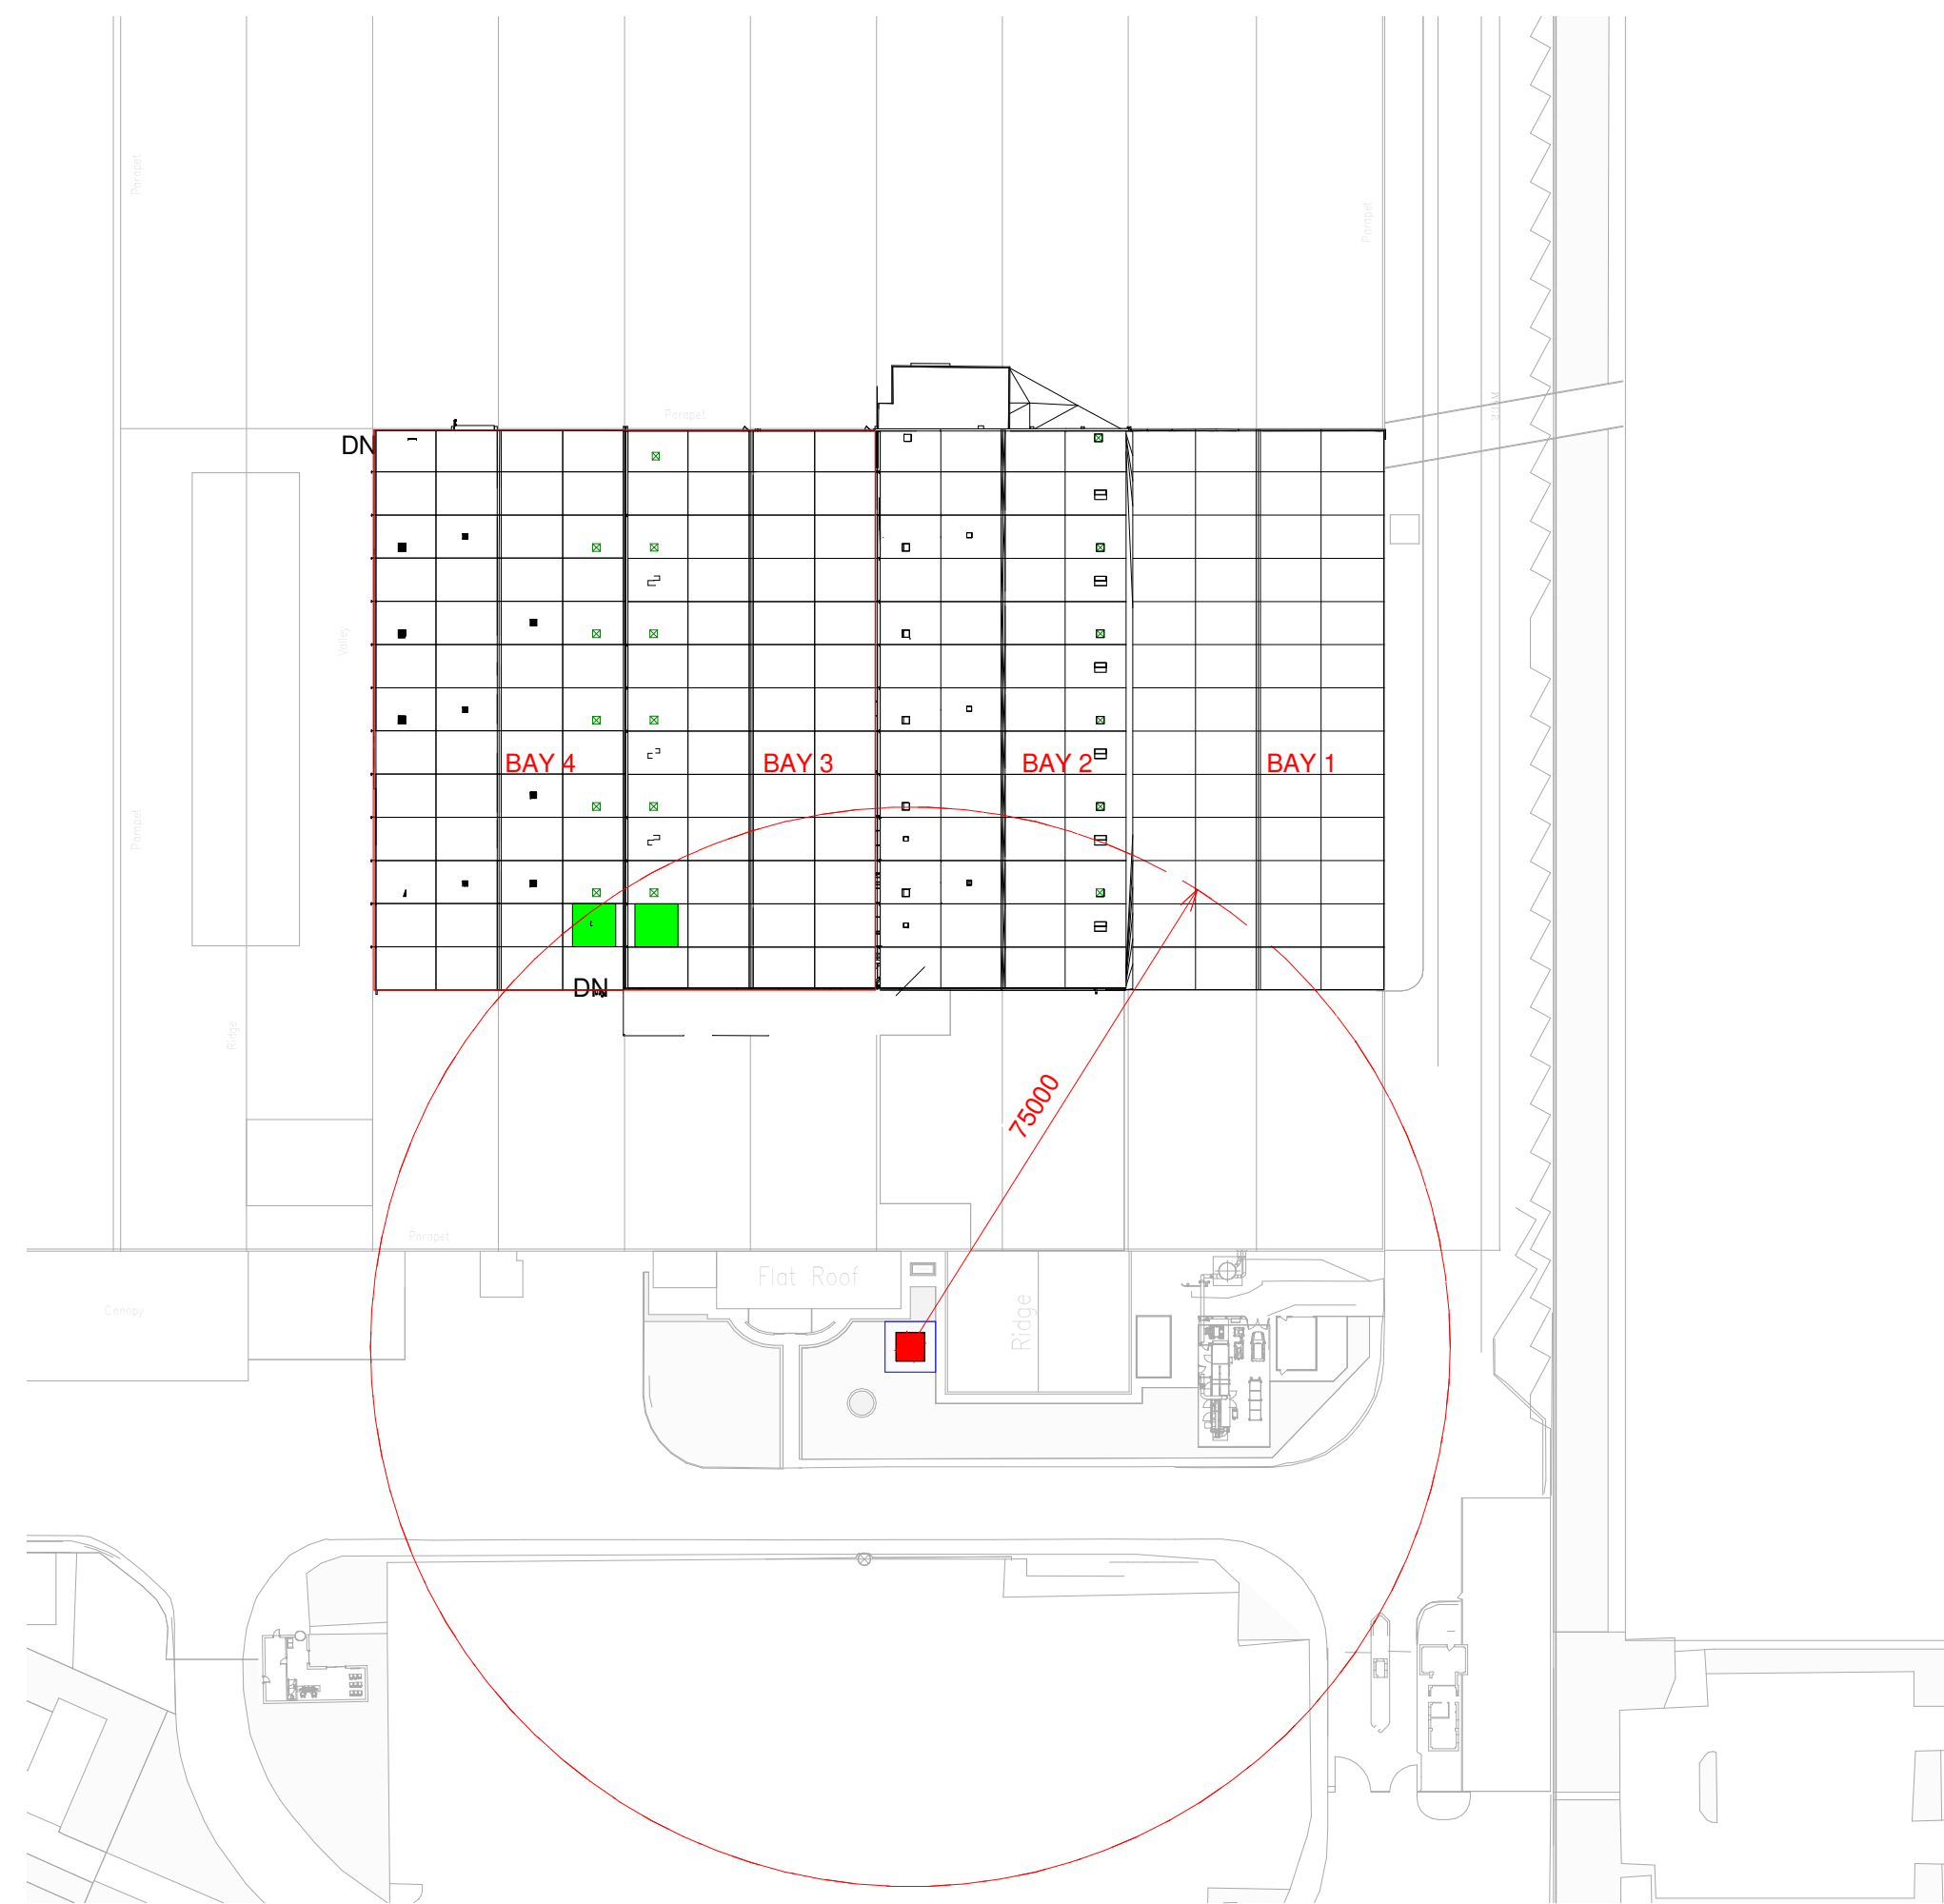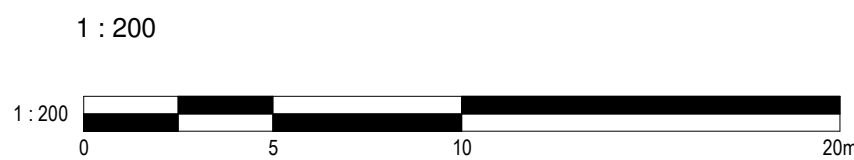

GA BUILDING ROOF PLAN

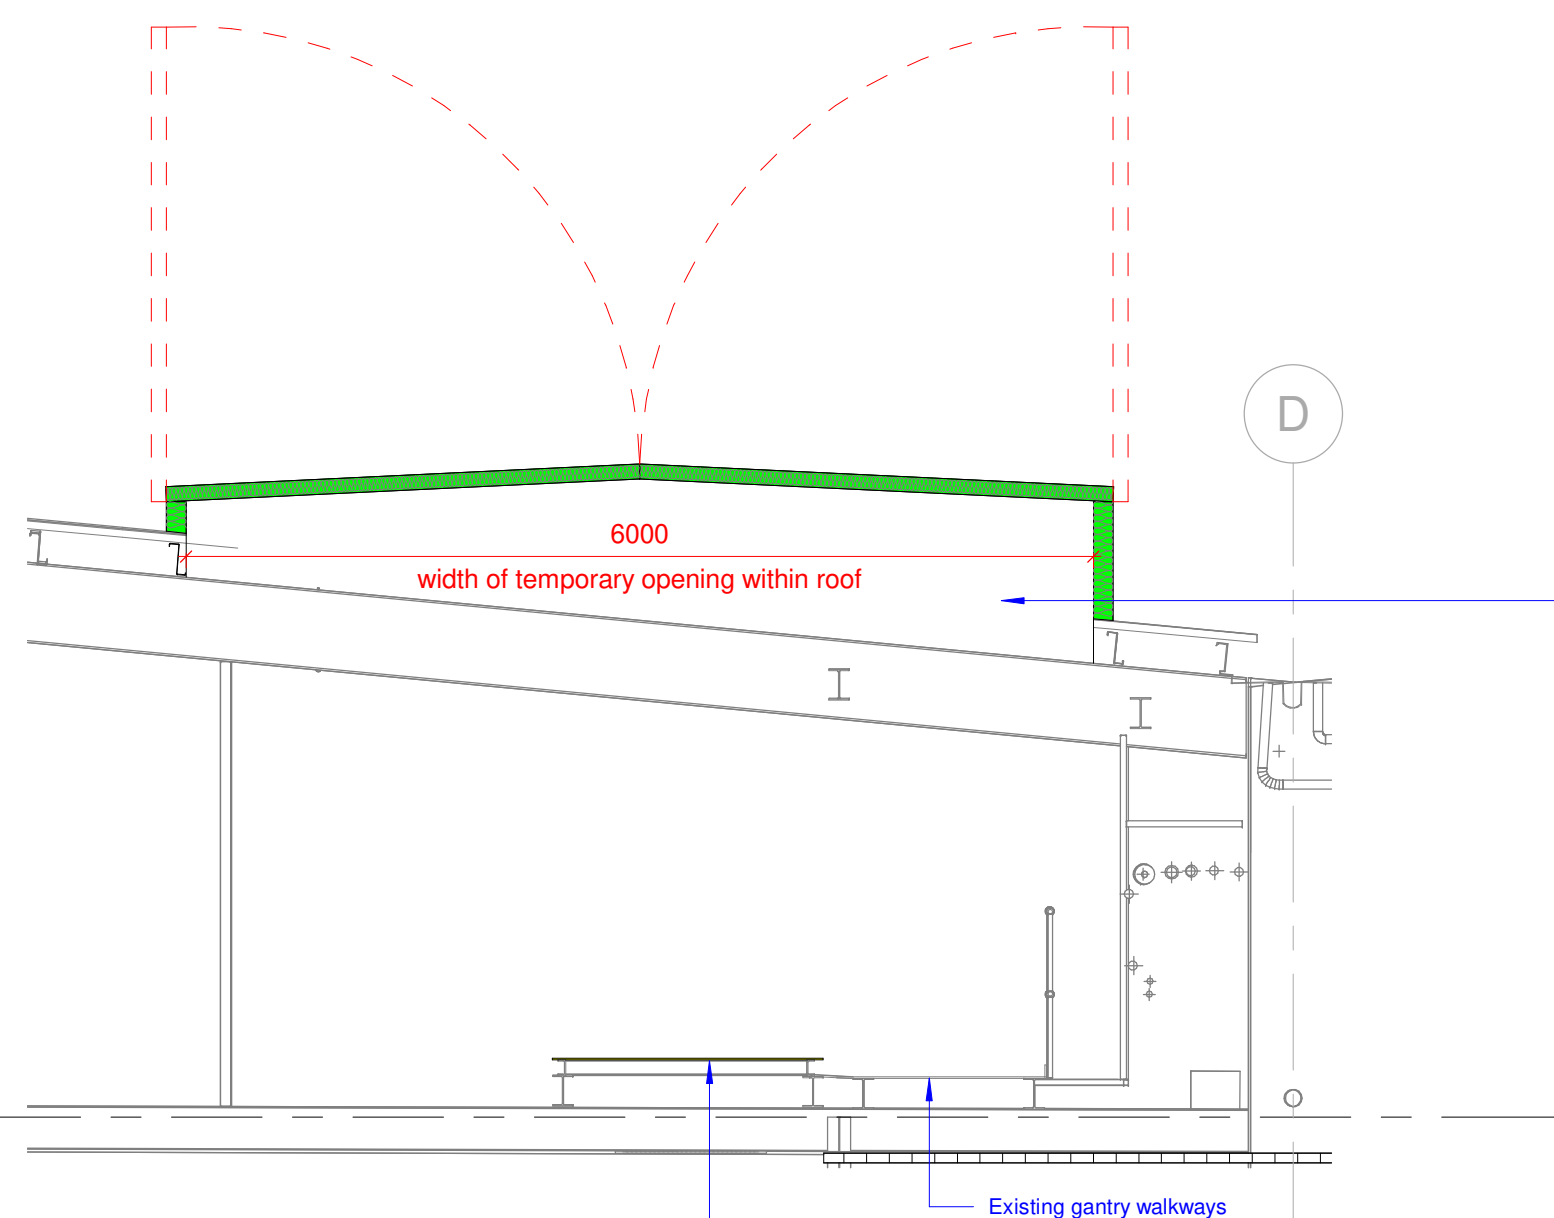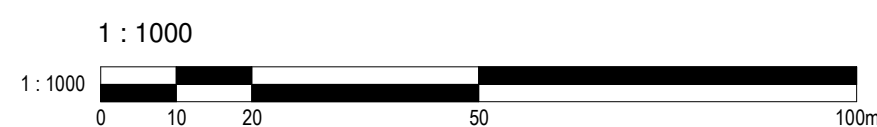

ROOF OPENING SECTION

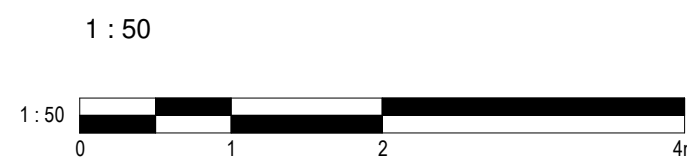

NOTE:
DO NOT SCALE FROM THIS DRAWING
VERIFY ALL DIMENSIONS AND SETTING OUT ON-SITE
NOTIFY ANY DISCREPANCIES TO THE ARCHITECT.
FOR STRUCTURAL INFORMATION, REFER TO
STRUCTURAL ENGINEERS DRAWINGS
FOR M&E INFORMATION, REFER TO M&E ENGINEER'S
AND SUB-CONTRACTOR'S DRAWINGS.
FOR HEALTH & SAFETY INFORMATION, REFER TO
HEALTH & SAFETY RISK ASSESSMENTS.


NOTE:
A MEASURED SURVEY HAS NOT YET BEEN
UNDERTAKEN ON THIS BUILDING, AND THESE
DRAWINGS HAVE BEEN PRODUCED BASED ON
EXISTING DRAWING INFORMATION PROVIDED BY CCE.
PLEASE DO NOT SCALE FROM THIS DRAWING.

KEY

- 6x6m Temporary opening within roof to remove purlins between portals for crane lift. Provide temporary roof cover when not in use. Made good on completion.
- Existing AHU's & redundant equipment on this line to be removed. Existing plantform to be retained and can be adapted as required as a runway to transport ceiling panels to the crane lifting location through the roof out of the building
- Cut down ceiling panels
- Red lines denotes area boundary of Bay 3 & 4 proposed walk-on ceiling works

1	29.04.22	Tender Issue	PN	LH
Rev	Date	Description	By	Chk

TENDER

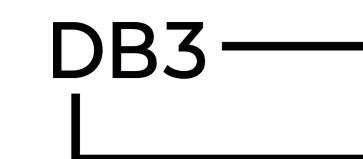

LEEDS

10 South Parade, Leeds, LS1 5QS
Tel: 0113 244 2931 www.darntonb3.com

CLIENT
COCA-COLA EUROPEAN PARTNERS

PROJECT
CCEP WALK-ON CEILING

TITLE
BAY 3 & 4 PROPOSED CEILING REMOVAL
STRATEGY PLAN

CREATION DATE	SCALE @ A1	DRN	CHK	STATUS
29 MAR 2022	As indicated	PN	LH	

SHEET NO.	REVISION
13656 - DB3 - B04 - 02 - DR - A - 20007	1


PROJECT NO (ORIGINATOR) (ZONE) (ELEVATION) (TYPE) (ROLE) (NUMBER)

© COPYRIGHT: ALL RIGHTS RESERVED.
THIS DOCUMENT MUST BE KEPT IN CONFIDENTIALITY WITH ALL OTHER RELEVANT DRAWINGS AND INFORMATION
AND NO INFORMATION MUST BE RELEASED TO ANY OTHER PARTY WITHOUT THE WRITTEN PERMISSION OF
THE ARCHITECT.
DO NOT SCALE OFF DRAWINGS. USE DISPLAYED DIMENSIONS.
PLOT DATE: 04/04/2022 15:25:00

NOTE


ALL PENETRATIONS TO THE WALLS TO BE SUITABLY SEALED AND MADE GOOD IN ORDER TO MAINTAIN FIRE INTEGRITY.

ANY OTHER REDUNDANT OPENING TO THE WALL TO BE SEALED AND MADE GOOD.

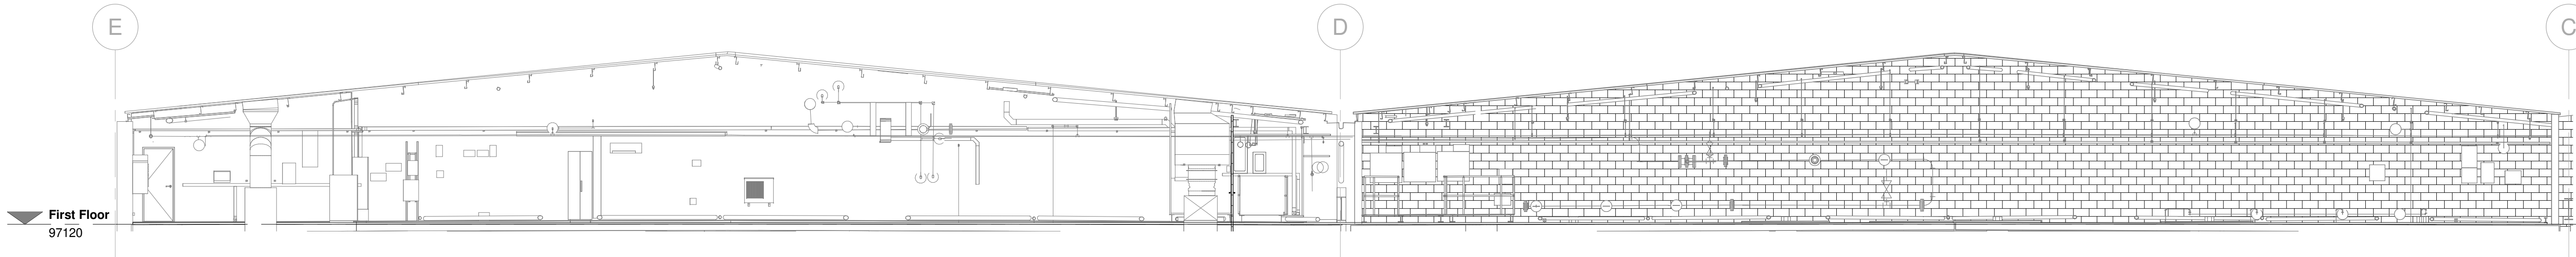


EXISTING INTERNAL ELEVATION

1 : 100

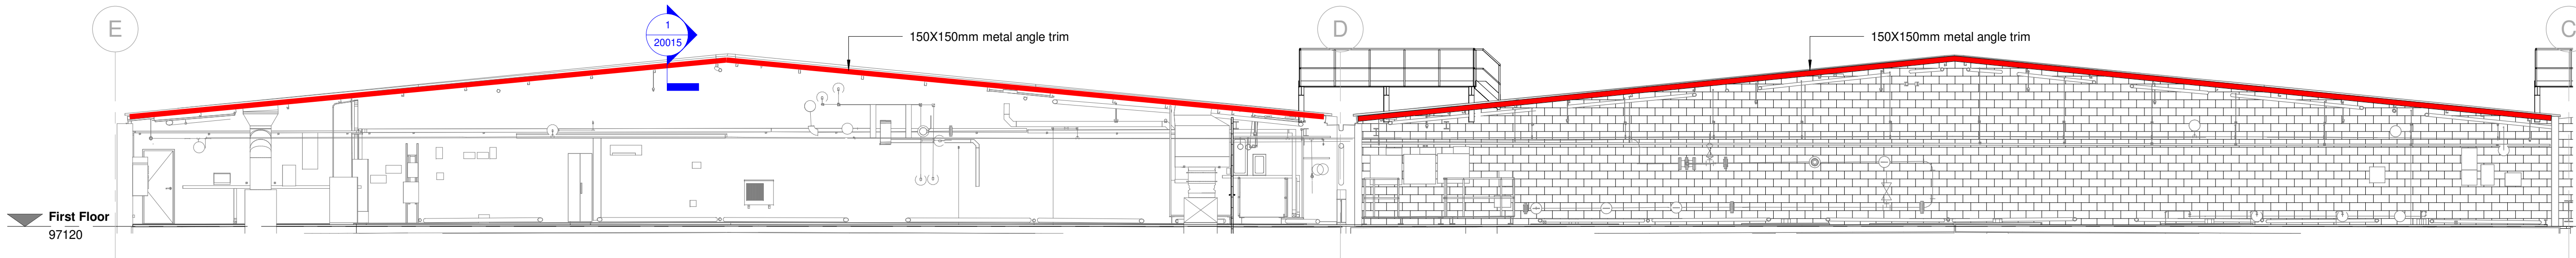


PROPOSED INTERNAL ELEVATION

1 : 100

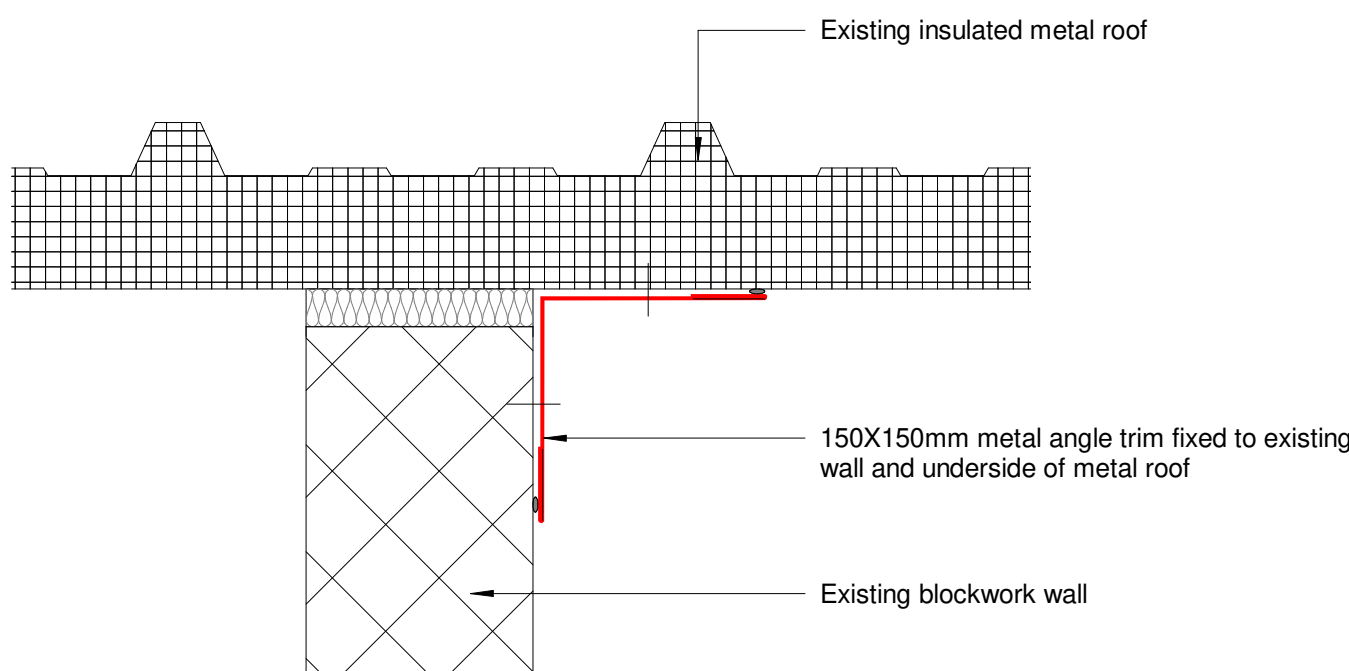

DETAIL 1

1 : 5

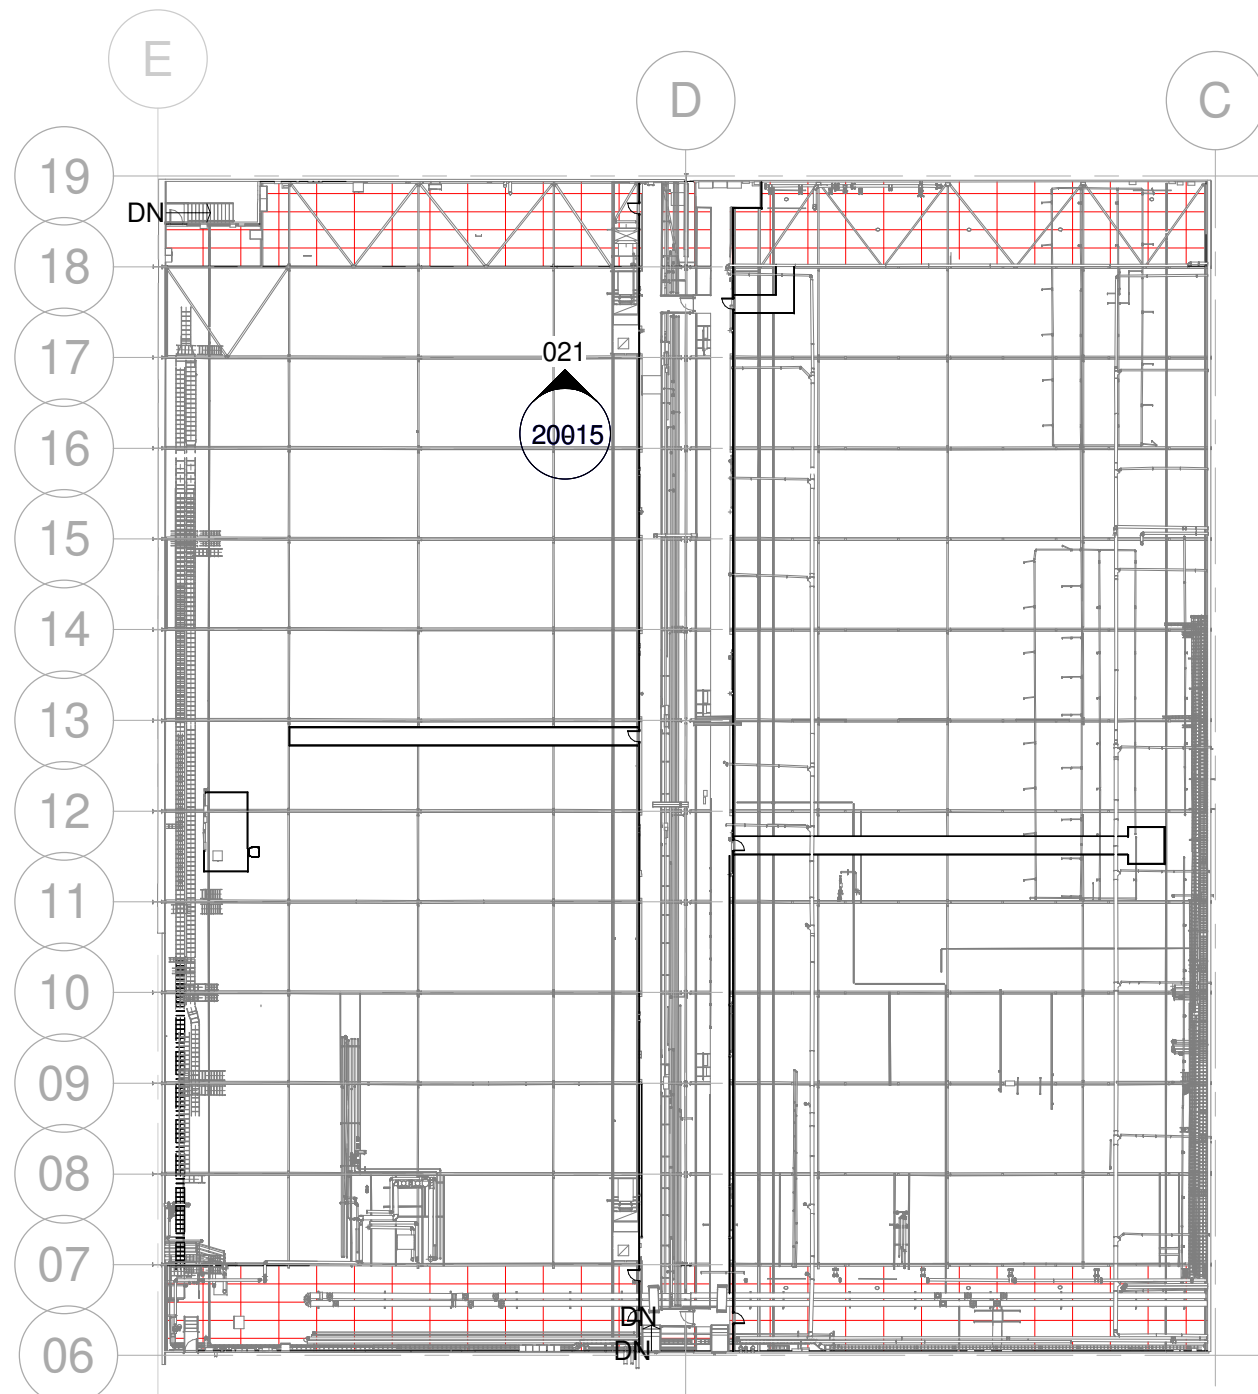


WALK-ON CEILING KEY PLAN - BAY 3 & 4

1 : 500

1	29.04.22	Tender Issue	PN	LH
Rev	Date	Description	By	Chk

TENDER

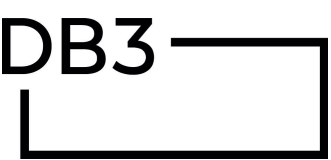

LEEDS

10 South Parade, Leeds, LS1 5QS
Tel: 0113 244 2931 www.darntonb3.com

CLIENT

COCA-COLA EUROPEAN PARTNERS

PROJECT

CCEP WALK-ON CEILING

TITLE

BAY 3 & 4 EXISTING & PROPOSED GABLE WALL
INTERNAL ELEVATION


CREATION DATE	SCALE @ A1	DRN	CHK	STATUS
29 APR 2022	As indicated	PN	LH	

SHEET NO.	REVISION
13656 - DB3 - B04 - 02 - DR - A - 20015	1

PROJECT NO (ORIGINATOR) (ZONE) (ELEVATION) (TYPE) (ROLE) (NUMBER)

© COPYRIGHT: ALL RIGHTS RESERVED.
THIS DOCUMENT MUST BE KEPT IN CONFIDENCE WITH ALL OTHER RELEVANT DRAWINGS AND INFORMATION.
ANY DISSEMINATION MUST BE REPORTED TO DARNTON IMMEDIATELY.
ANY DISSEMINATION MUST NOT BE USED FOR CONSTRUCTION UNLESS EXPRESSLY ISSUED FOR CONSTRUCTION.
DO NOT SCALE OFF DRAWINGS. USE DISPLAYED DIMENSIONS.


PLOT DATE: 15/04/2022 15:38:37

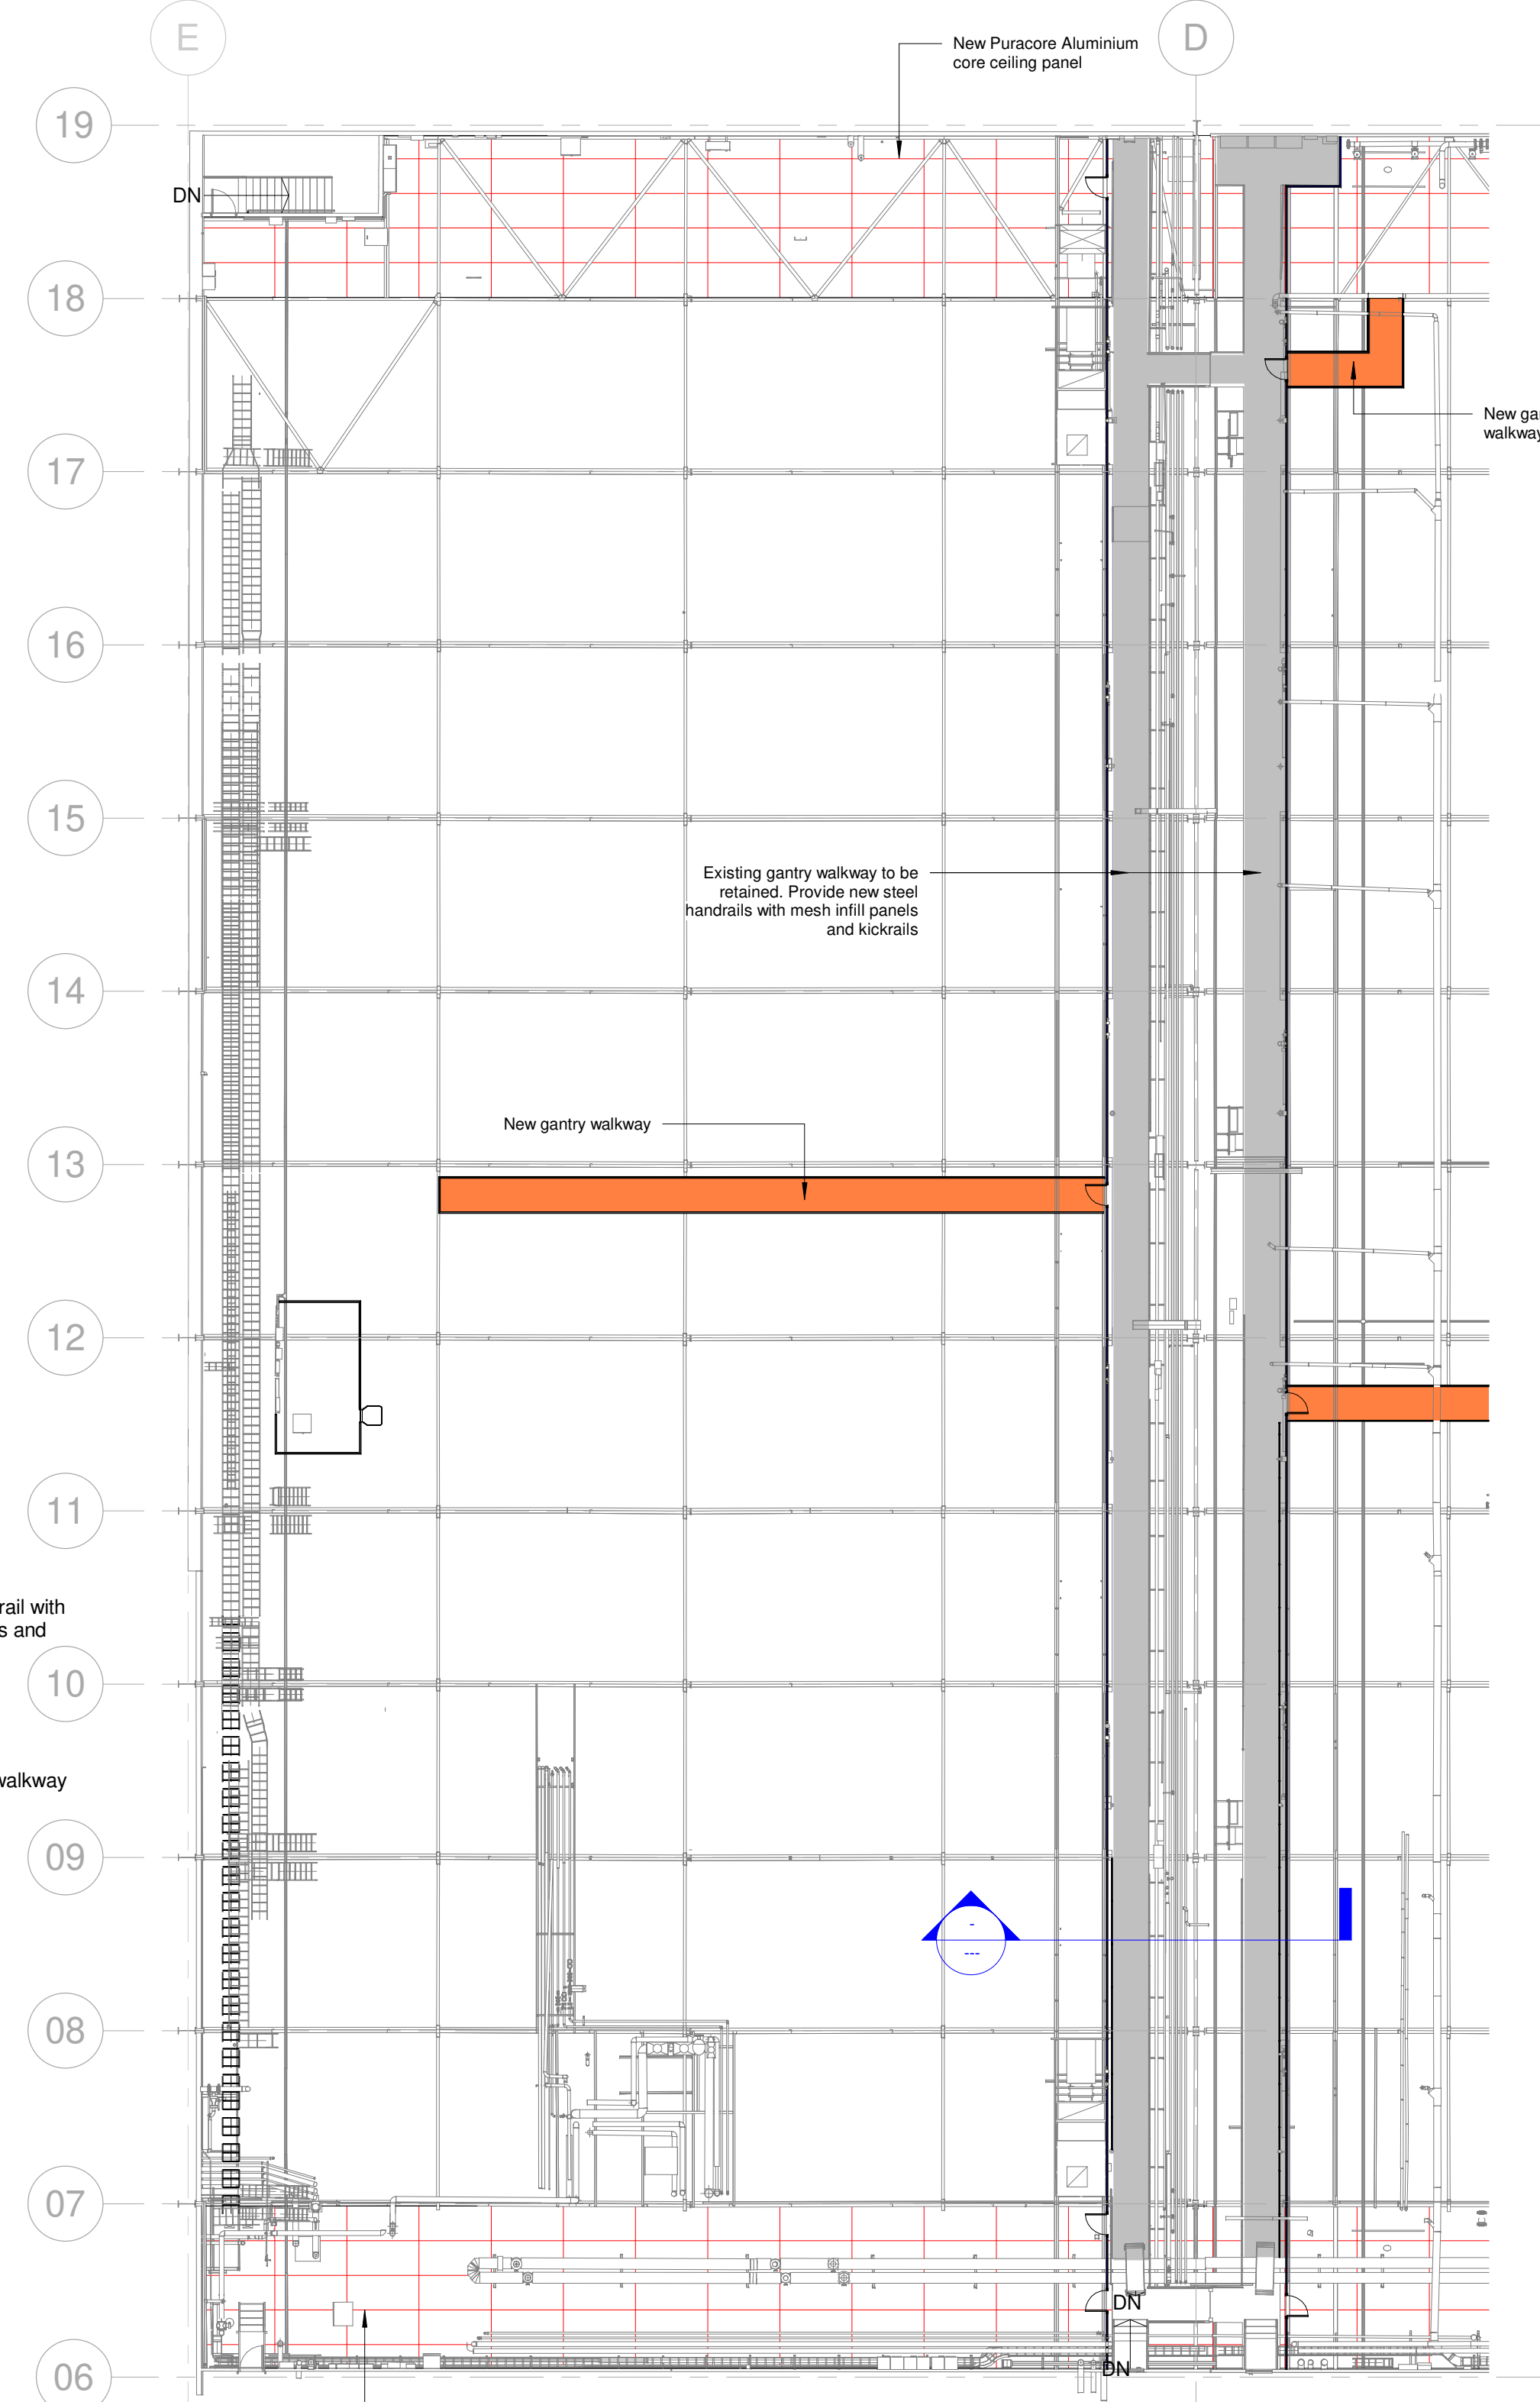

NOTE:

A MEASURED SURVEY HAS NOT YET BEEN UNDERTAKEN ON THIS BUILDING, AND THESE DRAWINGS HAVE BEEN PRODUCED BASED ON EXISTING DRAWING INFORMATION PROVIDED BY CCE.

PLEASE DO NOT SCALE FROM THIS DRAWING.

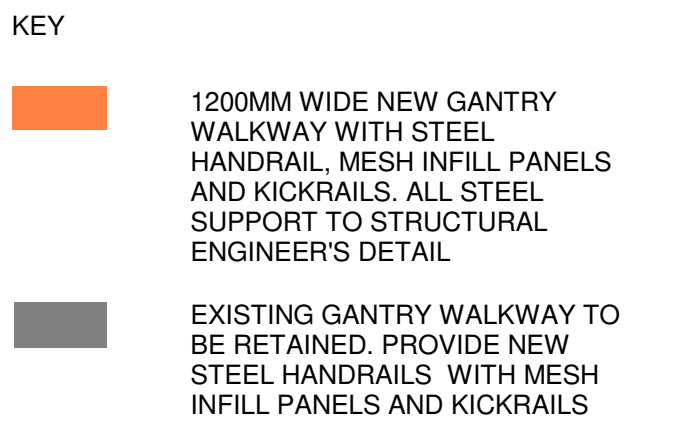

1 : 5

DO NOT SCALE OFF DRAWINGS. USE DISPLAYED DIMENSIONS.

1 : 50

Steelwork support and AHU's to be craned on to the roof, from cranes situated to the front and east-side of the building. Where the crane cannot reach the valleys (between bays 2-3, 3-4, and 4-5), rails are to be installed for rollers to move the plant to the final position.

Should the AHU's be replaced like-for-like in the ceiling void, a mobile crane situated to the east - side of the building on Wrexham Rd can lift the new AHU's through a roof opening to Bay 1. The AHU can be transported on runway beams above the crash deck to the final position to the other bays.

Redundant AHU's and associated plant to be transported on runway beams within ceiling void to external wall to east - side of building (between GL-16 to 17) on Wrexham Rd.



Scaffold tower to be erected to the east - side of the building (between GL - 16 to 17), and new external wall opening formed above ceiling level for egress of redundant AHU's and associated M & E (and access & egress of operatives). MEWP required to lift redundant AHU's from external wall opening to external ground floor level.

Walk-on ceiling panels to be removed from steelwork support, and transported on rails and rollers within ceiling void to external wall (GL-A) to east-side of the building (between GL-16 to 17) on Wrexham Rd.

Scaffold tower to be erected to east - side of the building (between GL-16 to 17) on Wrexham Rd, and new external wall opening formed above ceiling level for removal of existing walk-on ceiling (and access & egress of operatives). MEWP required to lift walk-on ceiling from high - level wall opening to external ground floor level.

New rooflights to all 4 bays to be lifted on to the roof using the cranes situated to the front and east-side of the building, with the aid of rails and rollers. Equally, new AHU platforms, access steps, and handrails to be lifted on to the roof with the cranes. Old roof vents to be removed using the cranes.

Access to Bays 1 to 4 for erecting scaffolding and crash deck to be further advised by specialist contractors.

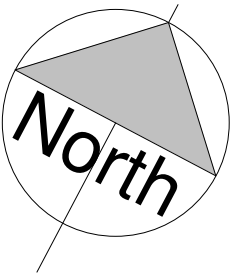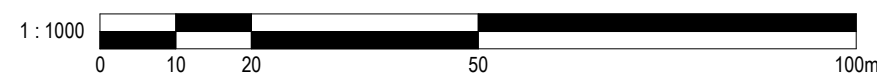

NOTE:

DO NOT SCALE FROM THIS DRAWING
VERIFY ALL DIMENSIONS AND SETTING OUT ON-SITE
NOTIFY ANY DISCREPANCIES TO THE ARCHITECT.
FOR STRUCTURAL INFORMATION, REFER TO
STRUCTURAL ENGINEERS DRAWINGS.
FOR M&E INFORMATION, REFER TO M&E ENGINEER'S
AND SUB-CONTRACTOR'S DRAWINGS.
FOR HEALTH & SAFETY INFORMATION, REFER TO
HEALTH & SAFETY RISK ASSESSMENTS.

NOTE:

A MEASURED SURVEY HAS NOT YET BEEN UNDERTAKEN ON THIS BUILDING, AND THESE DRAWINGS HAVE BEEN PRODUCED BASED ON EXISTING DRAWING INFORMATION PROVIDED BY CCE

PLEASE DO NOT SCALE FROM THIS DRAWING.

WOLFFCRAN 'WOLFF 7534.16 clear'
Crane with 75m reach, to be located
to the front of the building and to the
east-side of the building.

4x4m Crane (Red)
7x7m Crane Base indicative (Blue)

Contractor's compound and skip location

Security/reception building as existing

Lorry/vehicle access

Pedestrian access

Safety barriers

3	29.04.22	Tender Issue	PN	LH
2	25.03.22	Tender issue	CL	CL
1	29.04.20	Preliminary issue for feasibility	DH	CL
Rev	Date	Description	By	Chk

DB3

LEEDS

10 South Parade, Leeds, LS1 5QS
Tel: 0113 244 2931 www.darntonb3.com

CLIENT

COCA-COLA EUROPEAN PARTNERS

PROJEC

ACCEPT WALK-ON CEILING

TITLE

SITE LIFTING ACCESS PLAN


CREATION DATE	SCALE @ A1	DRN	CHK	STATUS
29 APR 2022	As indicated	PN	LH	

13656

PROJECT NO|ORIGINATOR|ZONE|LIFE|TYPE|ROI|NUMBER


THIS DRAWING MUST BE READ IN CONJUNCTION WITH ALL OTHER RELEVANT DRAWINGS AND INFORMATION. ANY DISCREPANCIES MUST BE REPORTED TO DARMCORP IMMEDIATELY.
THE DRAWING OR INFORMATION MUST NOT BE USED FOR CONSTRUCTION UNLESS EXPRESSLY ISSUED FOR CONSTRUCTION.

PLOT DATE 20/04/2022 16:31:58

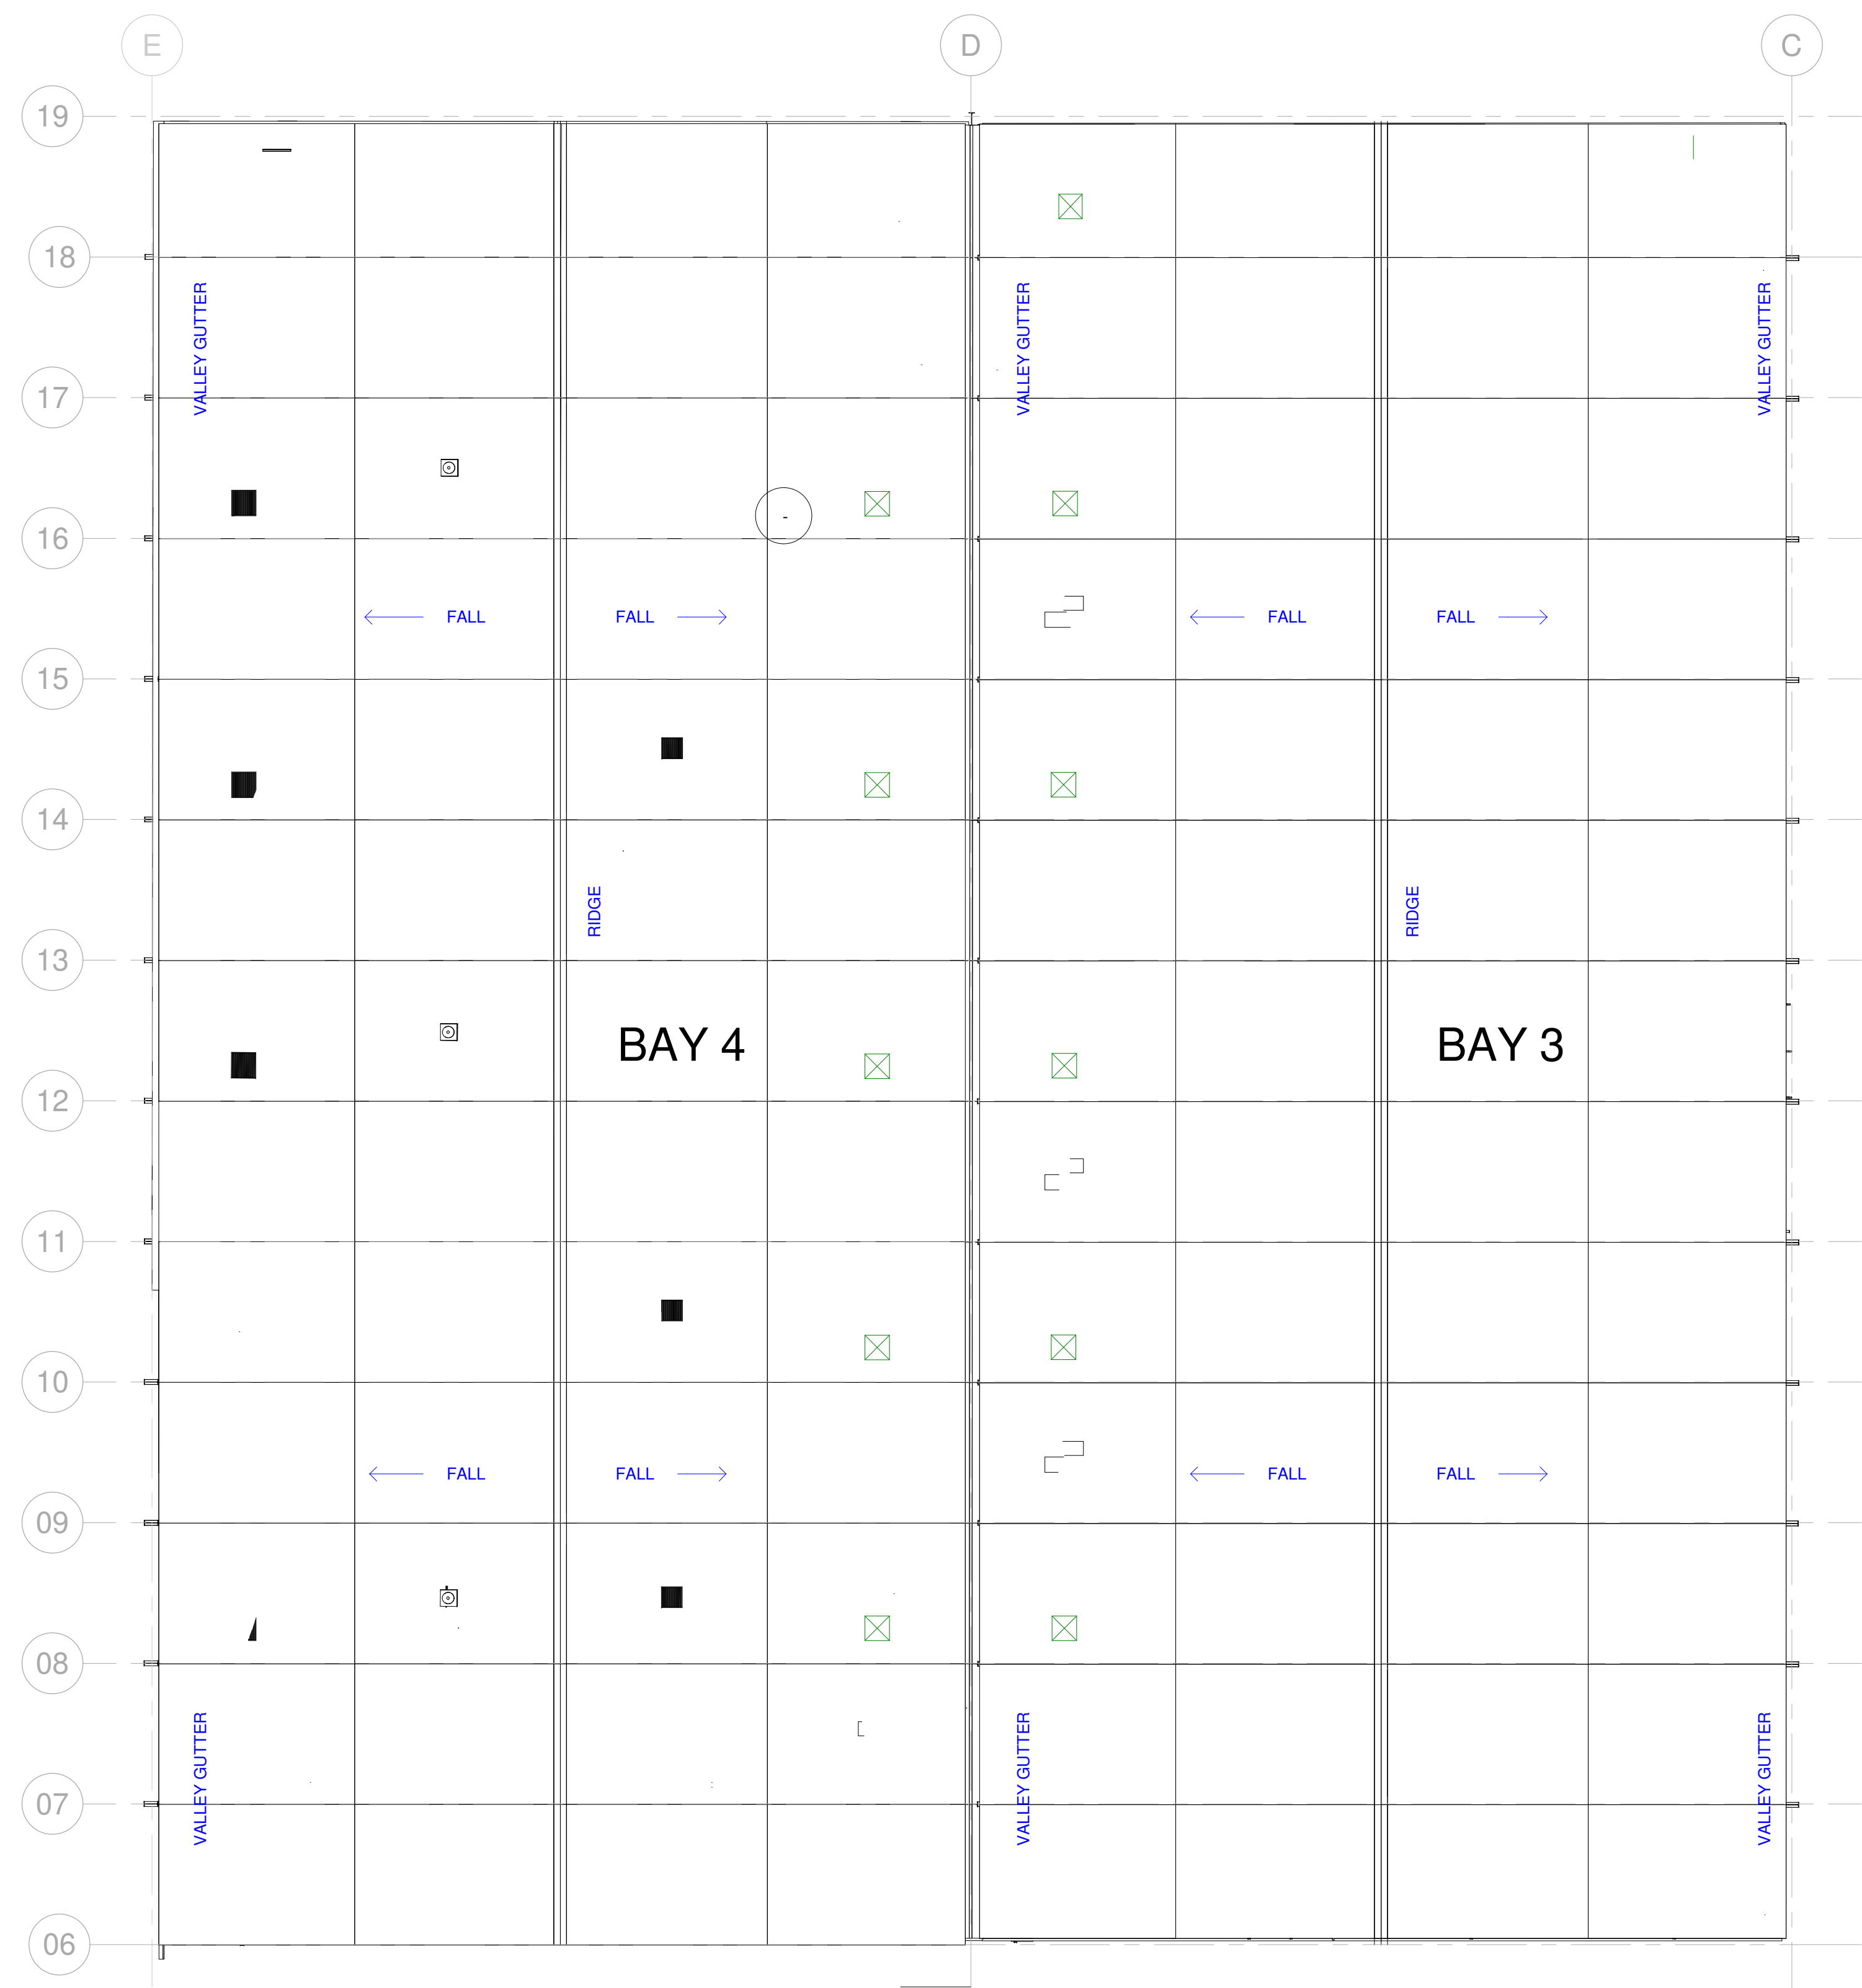

EXISTING ROOF PLAN - BAY 3 & 4

1 : 200

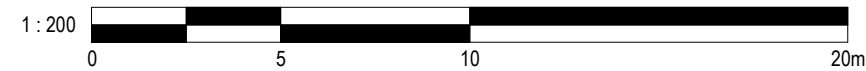

NOTE:

DO NOT SCALE FROM THIS DRAWING.
VERIFY ALL DIMENSIONS AND SETTING OUT ON-SITE.
NOTIFY ANY DISCREPANCIES TO THE ARCHITECT.
FOR STRUCTURAL INFORMATION, REFER TO STRUCTURAL ENGINEERS DRAWINGS.
FOR M&E INFORMATION, REFER TO M&E ENGINEER'S AND SUB-CONTRACTOR'S DRAWINGS.
FOR HEALTH & SAFETY INFORMATION, REFER TO HEALTH & SAFETY RISK ASSESSMENTS.


NOTE:

A MEASURED SURVEY HAS NOT YET BEEN UNDERTAKEN ON THIS BUILDING, AND THESE DRAWINGS HAVE BEEN PRODUCED BASED ON EXISTING DRAWING INFORMATION PROVIDED BY CCE.

PLEASE DO NOT SCALE FROM THIS DRAWING.

1	29.04.22	Tender Issue	PN	LH
Rev	Date	Description	By	Chk


TENDER

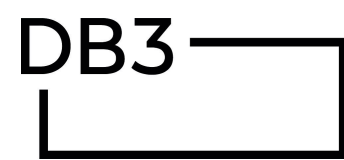

LEEDS

10 South Parade, Leeds, LS1 5QS
Tel: 0113 244 2931 www.darntonb3.com

CLIENT				
COCA-COLA EUROPEAN PARTNERS				
PROJECT				
CCEP WALK-ON CEILING				
TITLE				
BAY 3 & 4 EXISTING ROOF PLAN				
CREATION DATE	SCALE @ A1	DRN	CHK	STATUS
29 APR 2022	As indicated	PN	LH	
SHEET NO.				REVISION
13656 - DB3 - B04 - 03 - DR - A - 27001				1
PROJECT NO ORIGINATOR ZONE LEVEL TYPE ROLE NUMBER				
© COPYRIGHT: ALL RIGHTS RESERVED. AND ORIGINATOR MUST BE REPORTED TO ORIGINATOR IMMEDIATELY. AND ORIGINATOR MUST NOT BE USED FOR CONSTRUCTION UNLESS EXPRESSLY ISSUED FOR CONSTRUCTION. DO NOT SCALE OFF DRAWINGS. USE DISPLAYED DIMENSIONS.				
PLOT DATE: 29/04/2022 12:30:40				

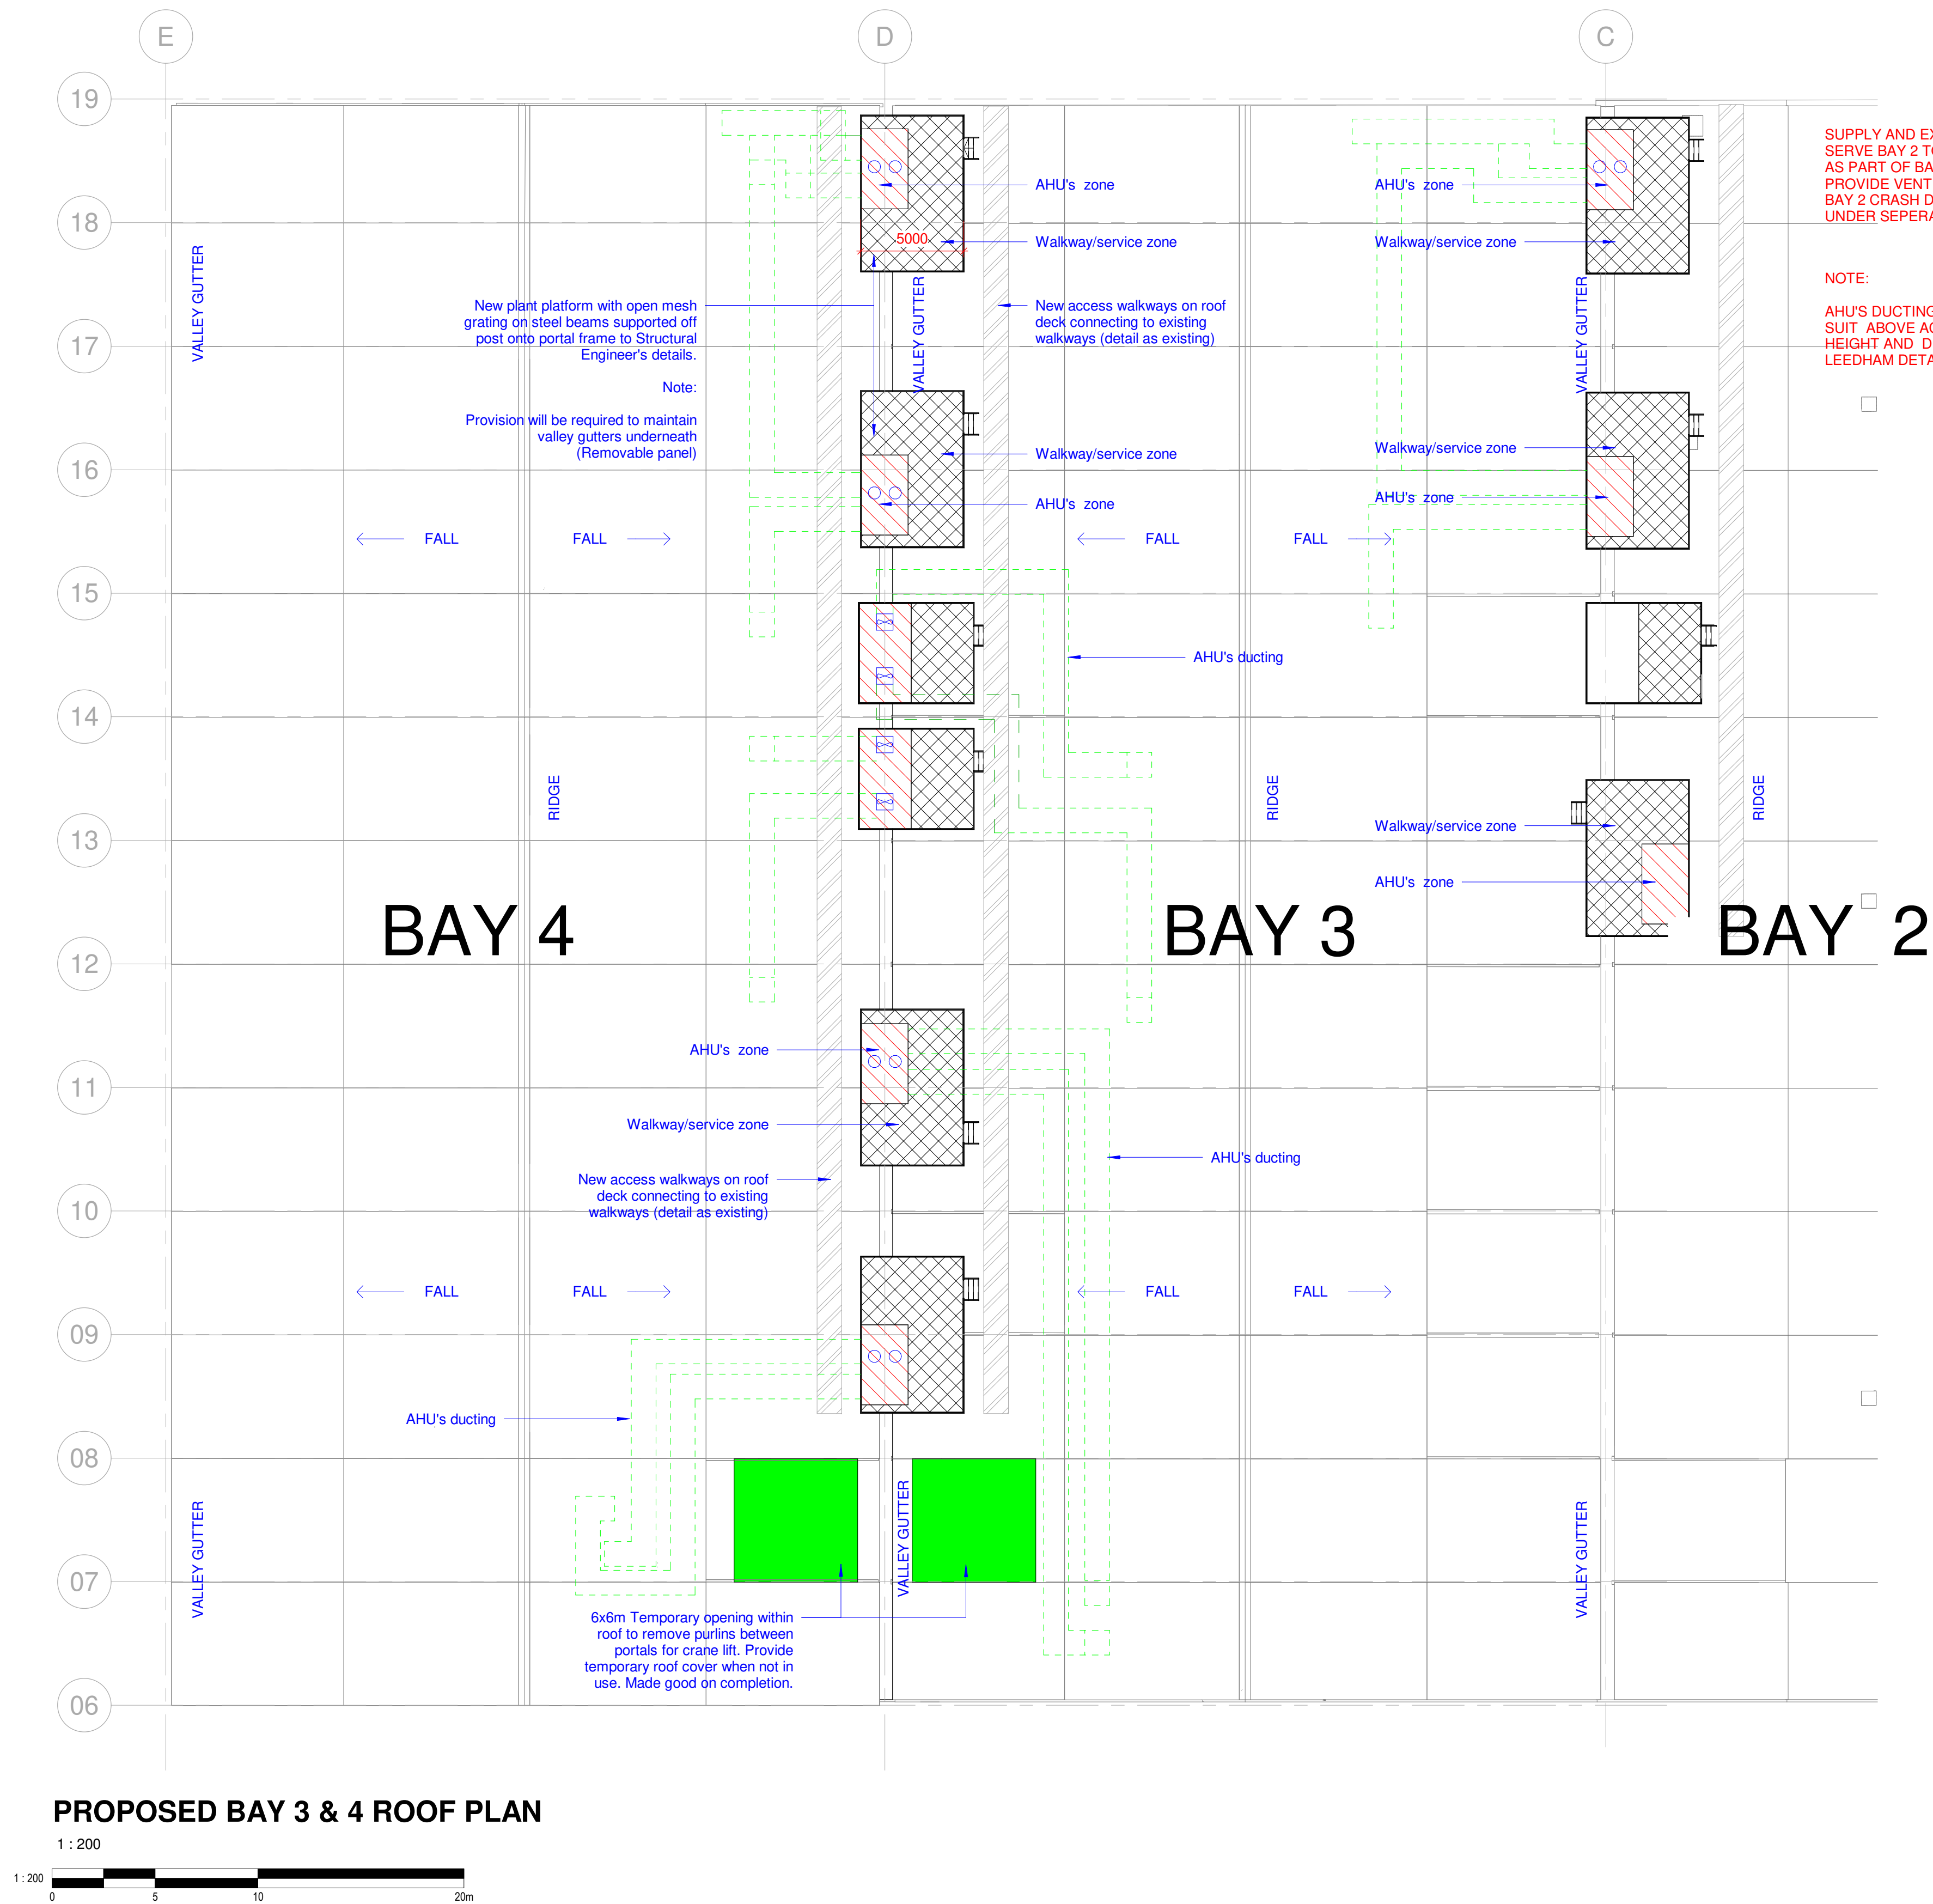

NOTE:
DO NOT SCALE FROM THIS DRAWING
VERIFY ALL DIMENSIONS AND SETTING OUT ON-SITE
NOTIFY ANY DISCREPANCIES TO THE ARCHITECT.
FOR STRUCTURAL INFORMATION, REFER TO
STRUCTURAL ENGINEERS DRAWINGS.
FOR M&E INFORMATION, REFER TO M&E ENGINEER'S
AND SUB-CONTRACTOR'S DRAWINGS.
FOR HEALTH & SAFETY INFORMATION, REFER TO
HEALTH & SAFETY RISK ASSESSMENTS.

NOTE:
A MEASURED SURVEY HAS NOT YET BEEN
UNDERTAKEN ON THIS BUILDING, AND THESE
DRAWINGS HAVE BEEN PRODUCED BASED ON
EXISTING DRAWING INFORMATION PROVIDED BY CCE.
PLEASE DO NOT SCALE FROM THIS DRAWING.

NOTE
ALL REDUNDANT VENT, ETC THAT
PENETRATE THE ROOF TO BE
REMOVED AND MAKE GOOD
GUTTER TO BE REPLACED AND
CLADDING IN THE LOCATION OF THE
PROPOSED ROOF MOUNTED PLANT
RE-ROOFING WOULD NEED TO BE IN
SECTIONS AND SUITABLE PROTECTION
PROVIDED TO PREVENT WATER
INGRESS.

1	29.04.22	Tender Issue	PN	LH
Rev	Date	Description	By	Chk

TENDER

DB3

LEEDS

10 South Parade, Leeds, LS1 5QS
Tel: 0113 244 2931 www.darntonb3.com

CLIENT
COCA-COLA EUROPEAN PARTNERS


PROJECT
CCEP WALK-ON CEILING

TITLE
BAY 3 & 4 PROPOSED ROOF PLAN

CREATION DATE	SCALE @ A1	DRN	CHK	STATUS
29 APR 2022	As indicated	PN	LH	
SHEET NO.				REVISION


13656 - DB3 - B04 - 03 - DR - A - 27002 1

PROJECT NO (ORIGINATOR/ZONE/LEVEL/TYPE/ROLE/NUMBER)
© COPYRIGHT: ALL RIGHTS RESERVED.
THIS DOCUMENT MUST BE KEPT IN CONFIDENTIALITY WITH ALL OTHER RELEVANT DRAWINGS AND INFORMATION
AND NO INFORMATION MUST BE RELEASED TO ANY OTHER PARTY WITHOUT THE WRITTEN PERMISSION OF DB3
DO NOT SCALE OFF DRAWINGS. USE DISPLAYED DIMENSIONS.
PLOT DATE: 04/04/2022 15:15:56

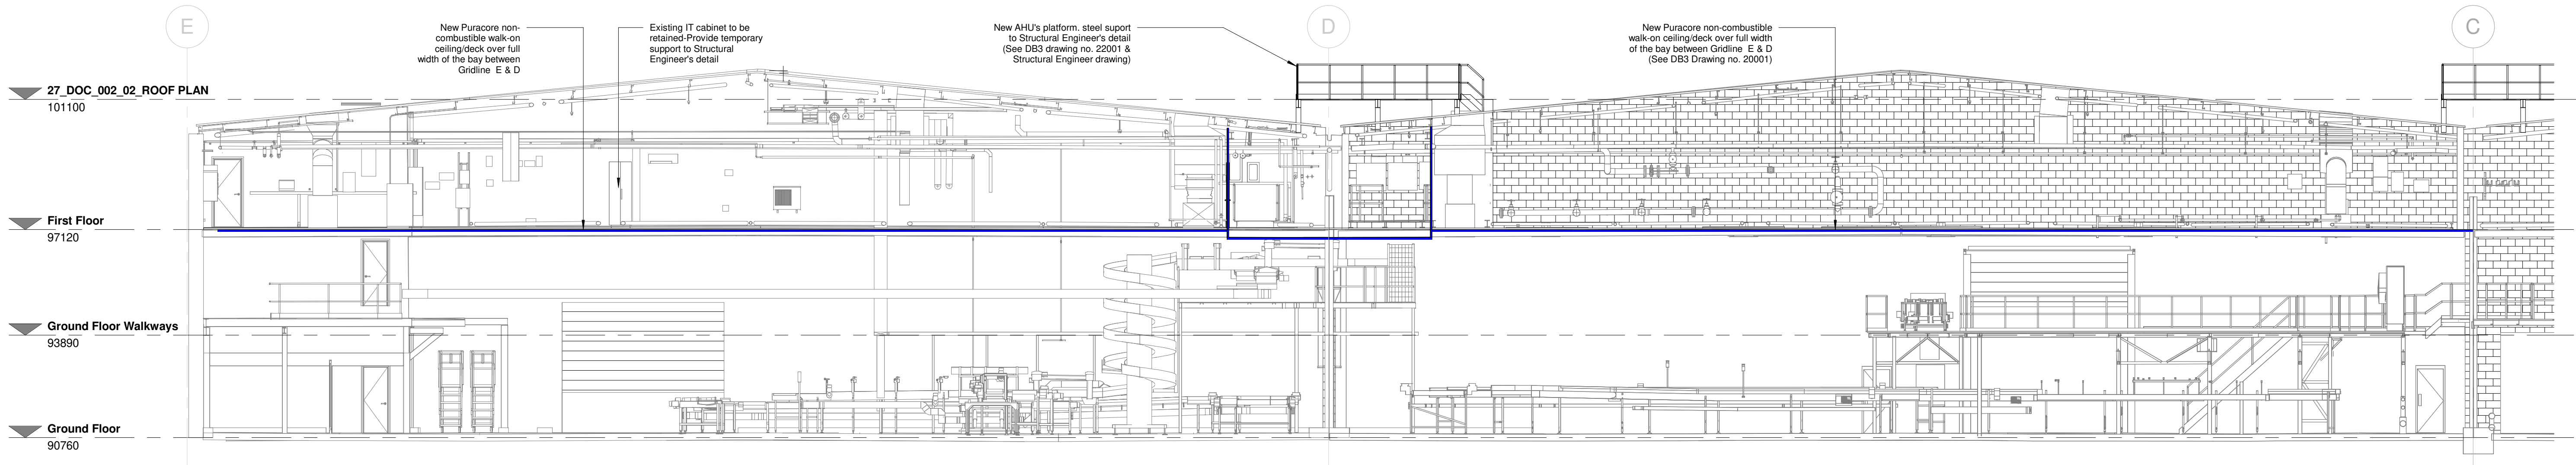



BAY 3 & 4 PROPOSED GA SECTION 3

1 : 100

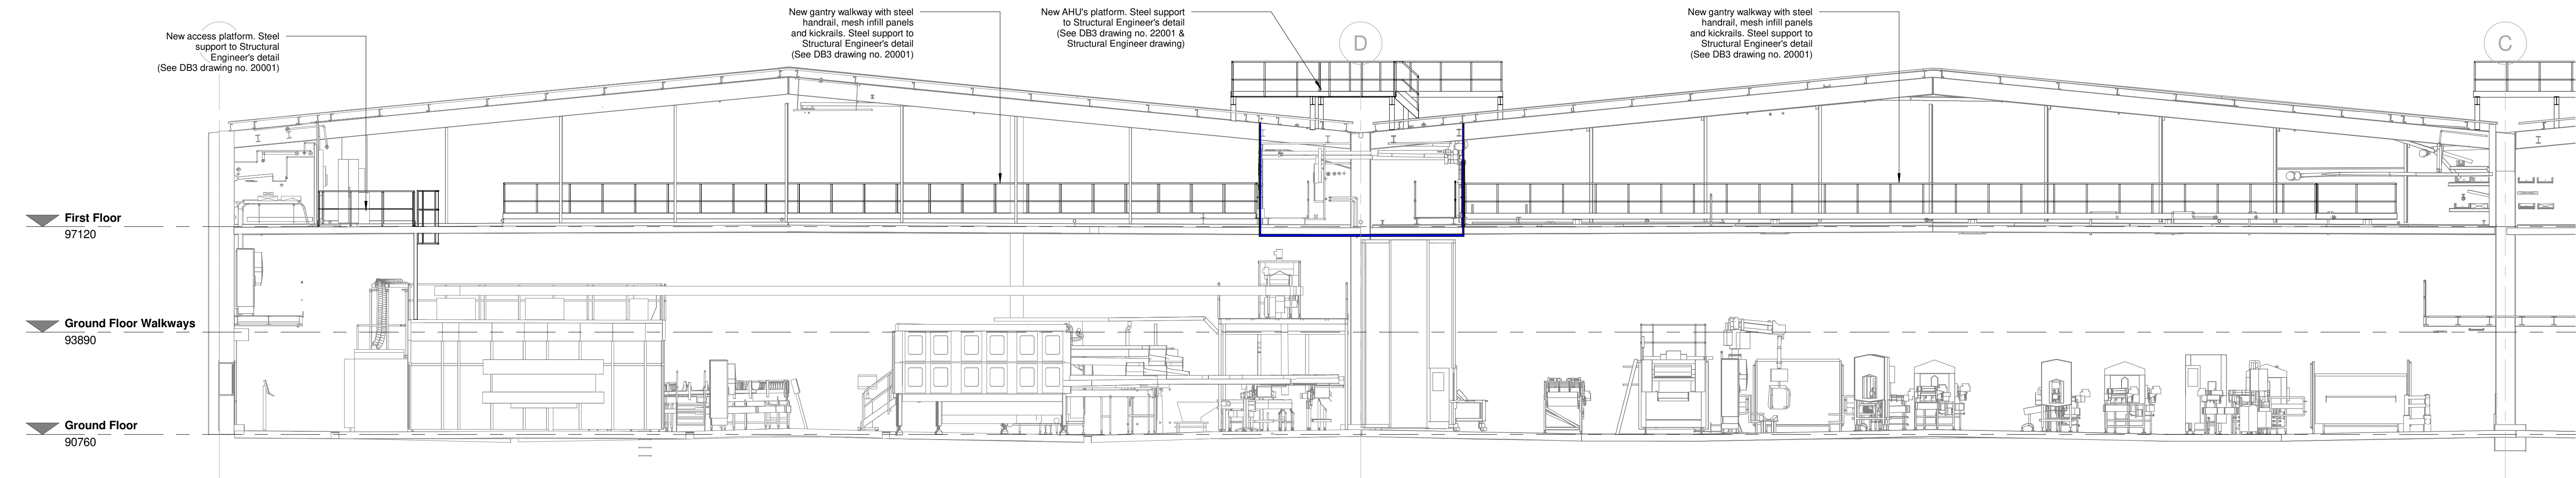

BAY 3 & 4 PROPOSED GA SECTION 4

1 : 100

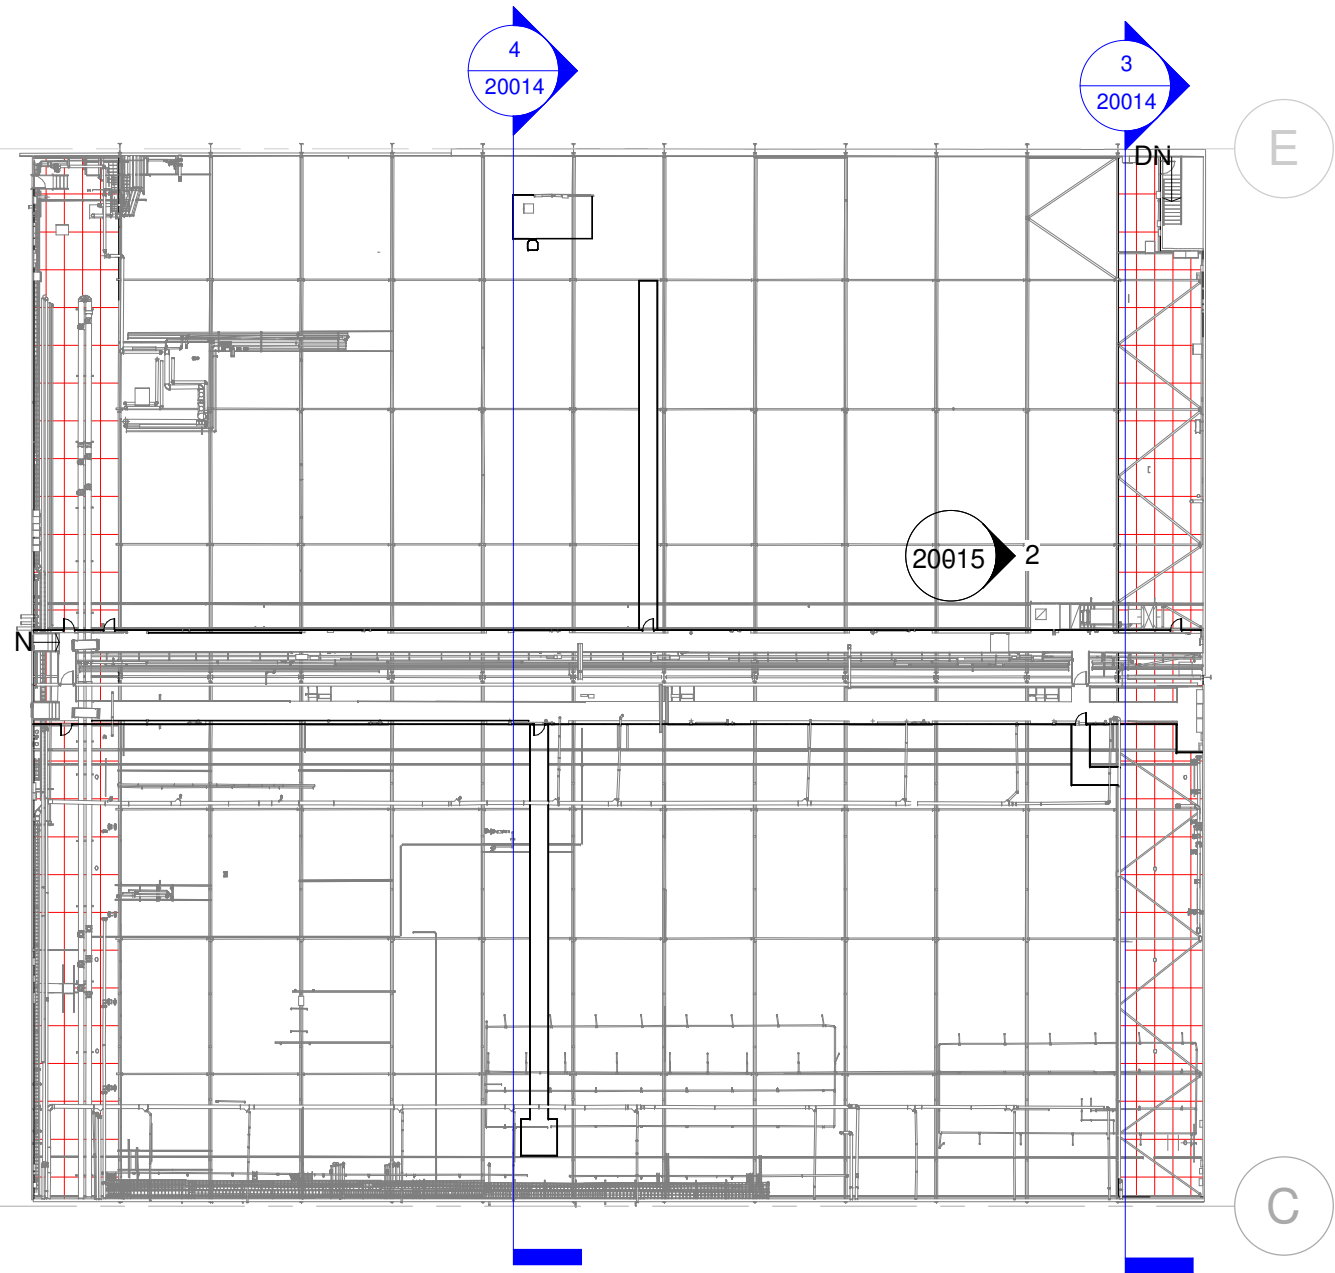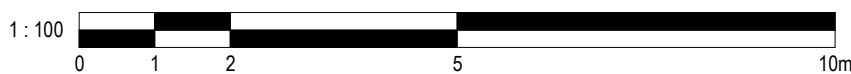

BAY 3 & 4 KEY PLAN

1 : 500

1	29.04.22	Tender Issue	PN	LH
Rev	Date	Description	By	Chk

TENDER

DB3

LEEDS

10 South Parade, Leeds, LS1 5QS
Tel: 0113 244 2931 www.darntonb3.com

CLIENT
COCA-COLA EUROPEAN PARTNERS

PROJECT
CCEP WALK-ON CEILING

TITLE
BAY 3 & 4 PROPOSED BUILDING SECTIONS
SHEET 2

CREATION DATE	SCALE @ A1	DRN	CHK	STATUS
29 APR 2022	As indicated	PN	LH	

SHEET NO.	REVISION
13656 - DB3 - B04 - ZZ - DR - A - 20014	1

PROJECT NO (ORIGINATOR) DATE (LEVEL) TYPE (ROLE) NUMBER
© COPYRIGHT: ALL RIGHTS RESERVED.
THIS DOCUMENT MUST BE KEPT IN CONFIDENTIALITY WITH ALL OTHERS RELEVANT DRAWINGS AND INFORMATION
AND NO PARTS OF IT MAY BE REPRODUCED OR TRANSMITTED IN ANY FORM OR BY ANY MEANS WITHOUT THE WRITTEN
PERMISSION OF THE ORIGINATOR. THE ORIGINATOR SHALL BE RESPONSIBLE FOR THE ACCURACY OF THE INFORMATION
CONTAINED HEREIN. THE ORIGINATOR SHALL NOT BE RESPONSIBLE FOR THE CONSTRUCTION OF THE PROJECT.
DO NOT SCALE OFF DIMENSIONS. USE DISPLAYED DIMENSIONS.
PLOT DATE: 04/04/2022 14:02:31