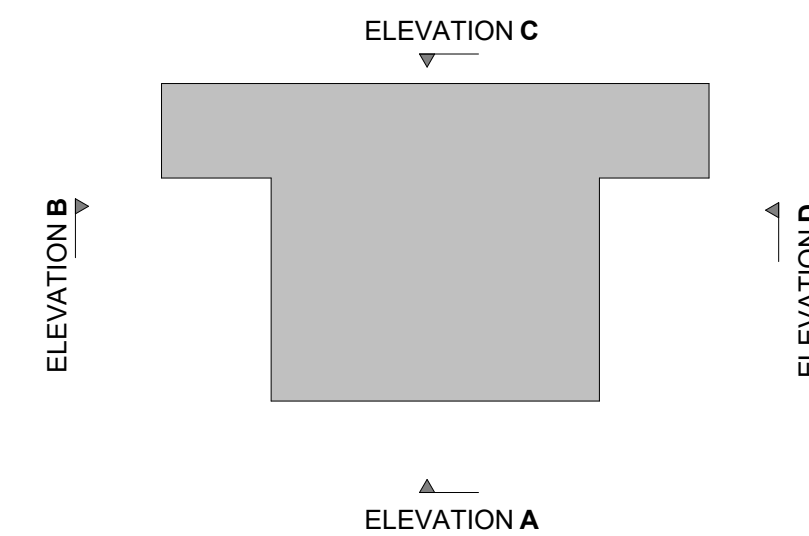
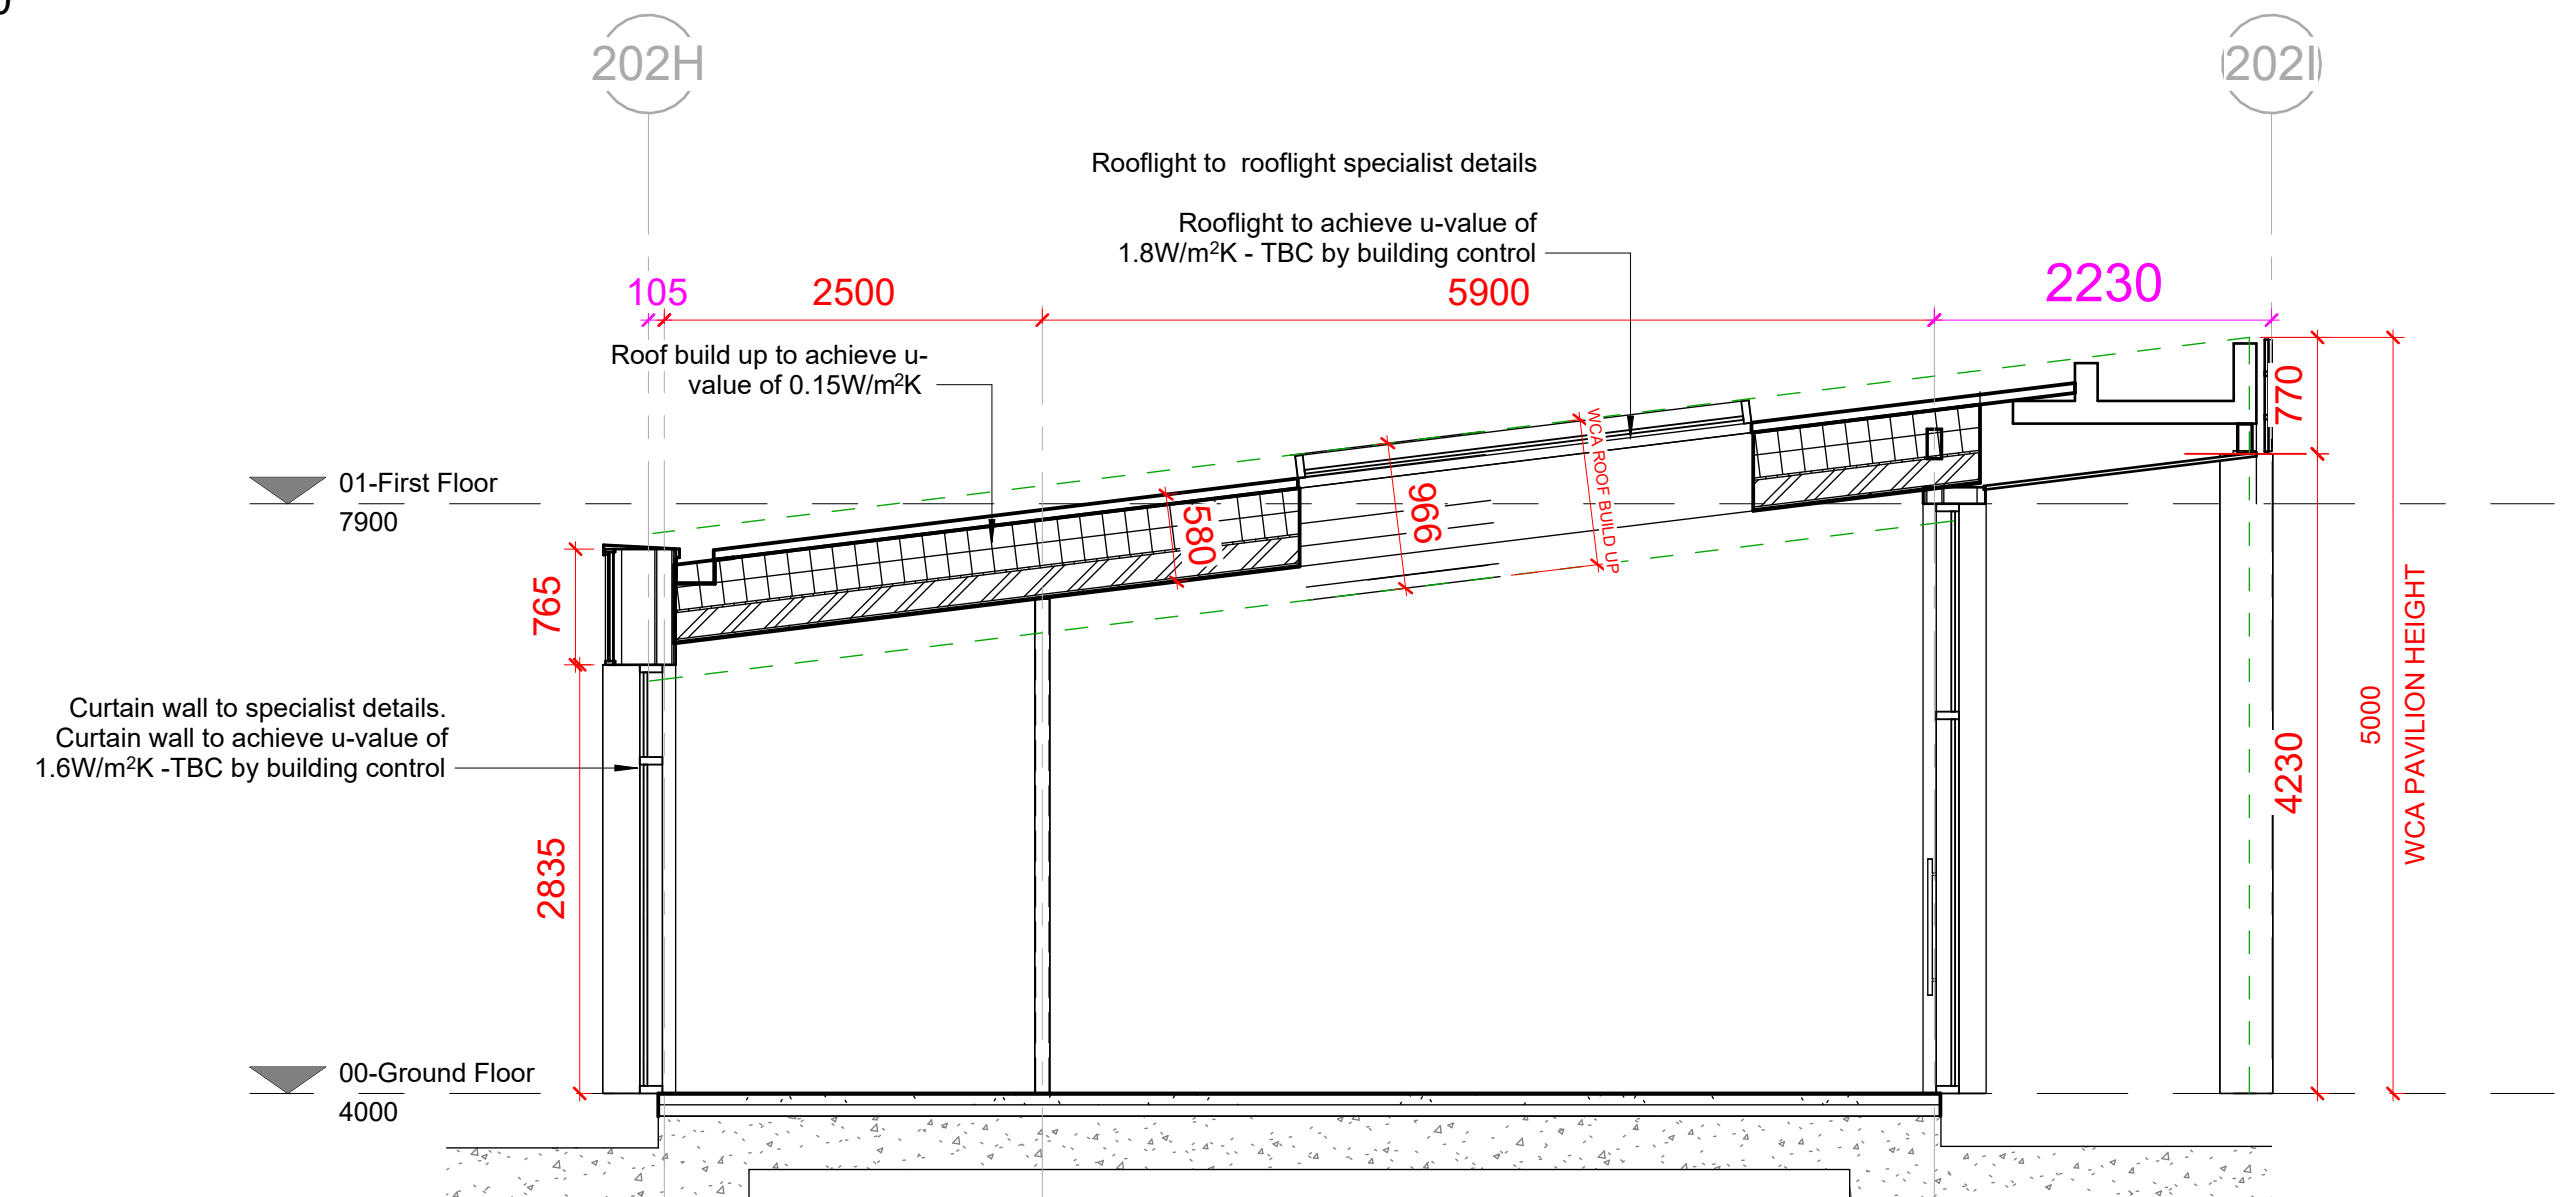
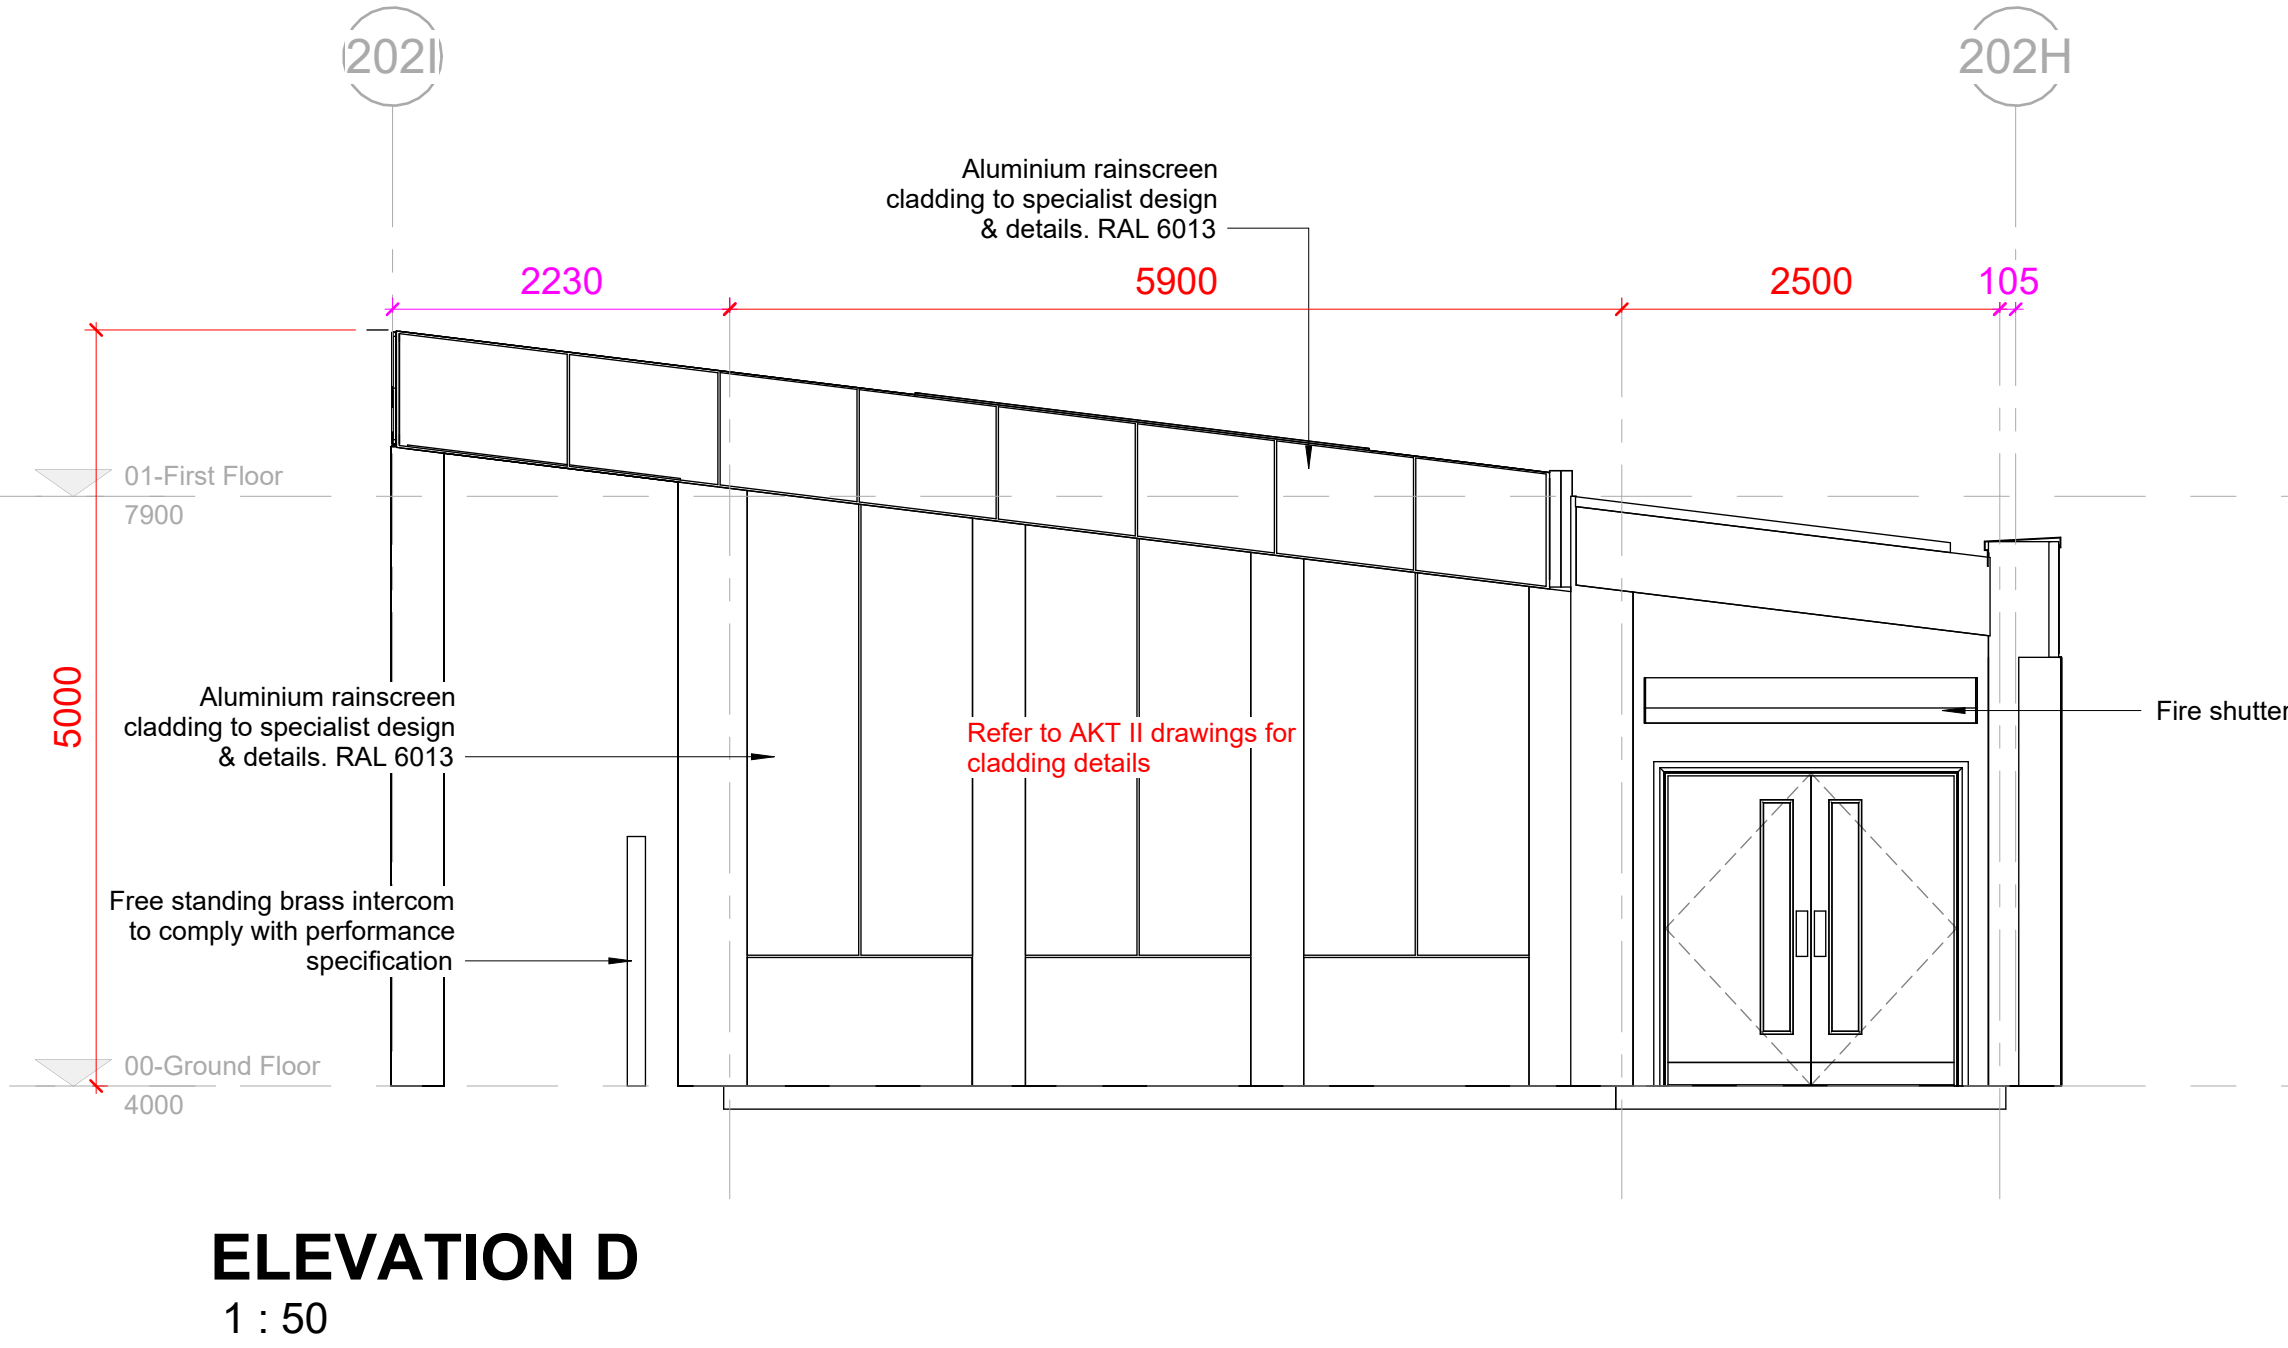
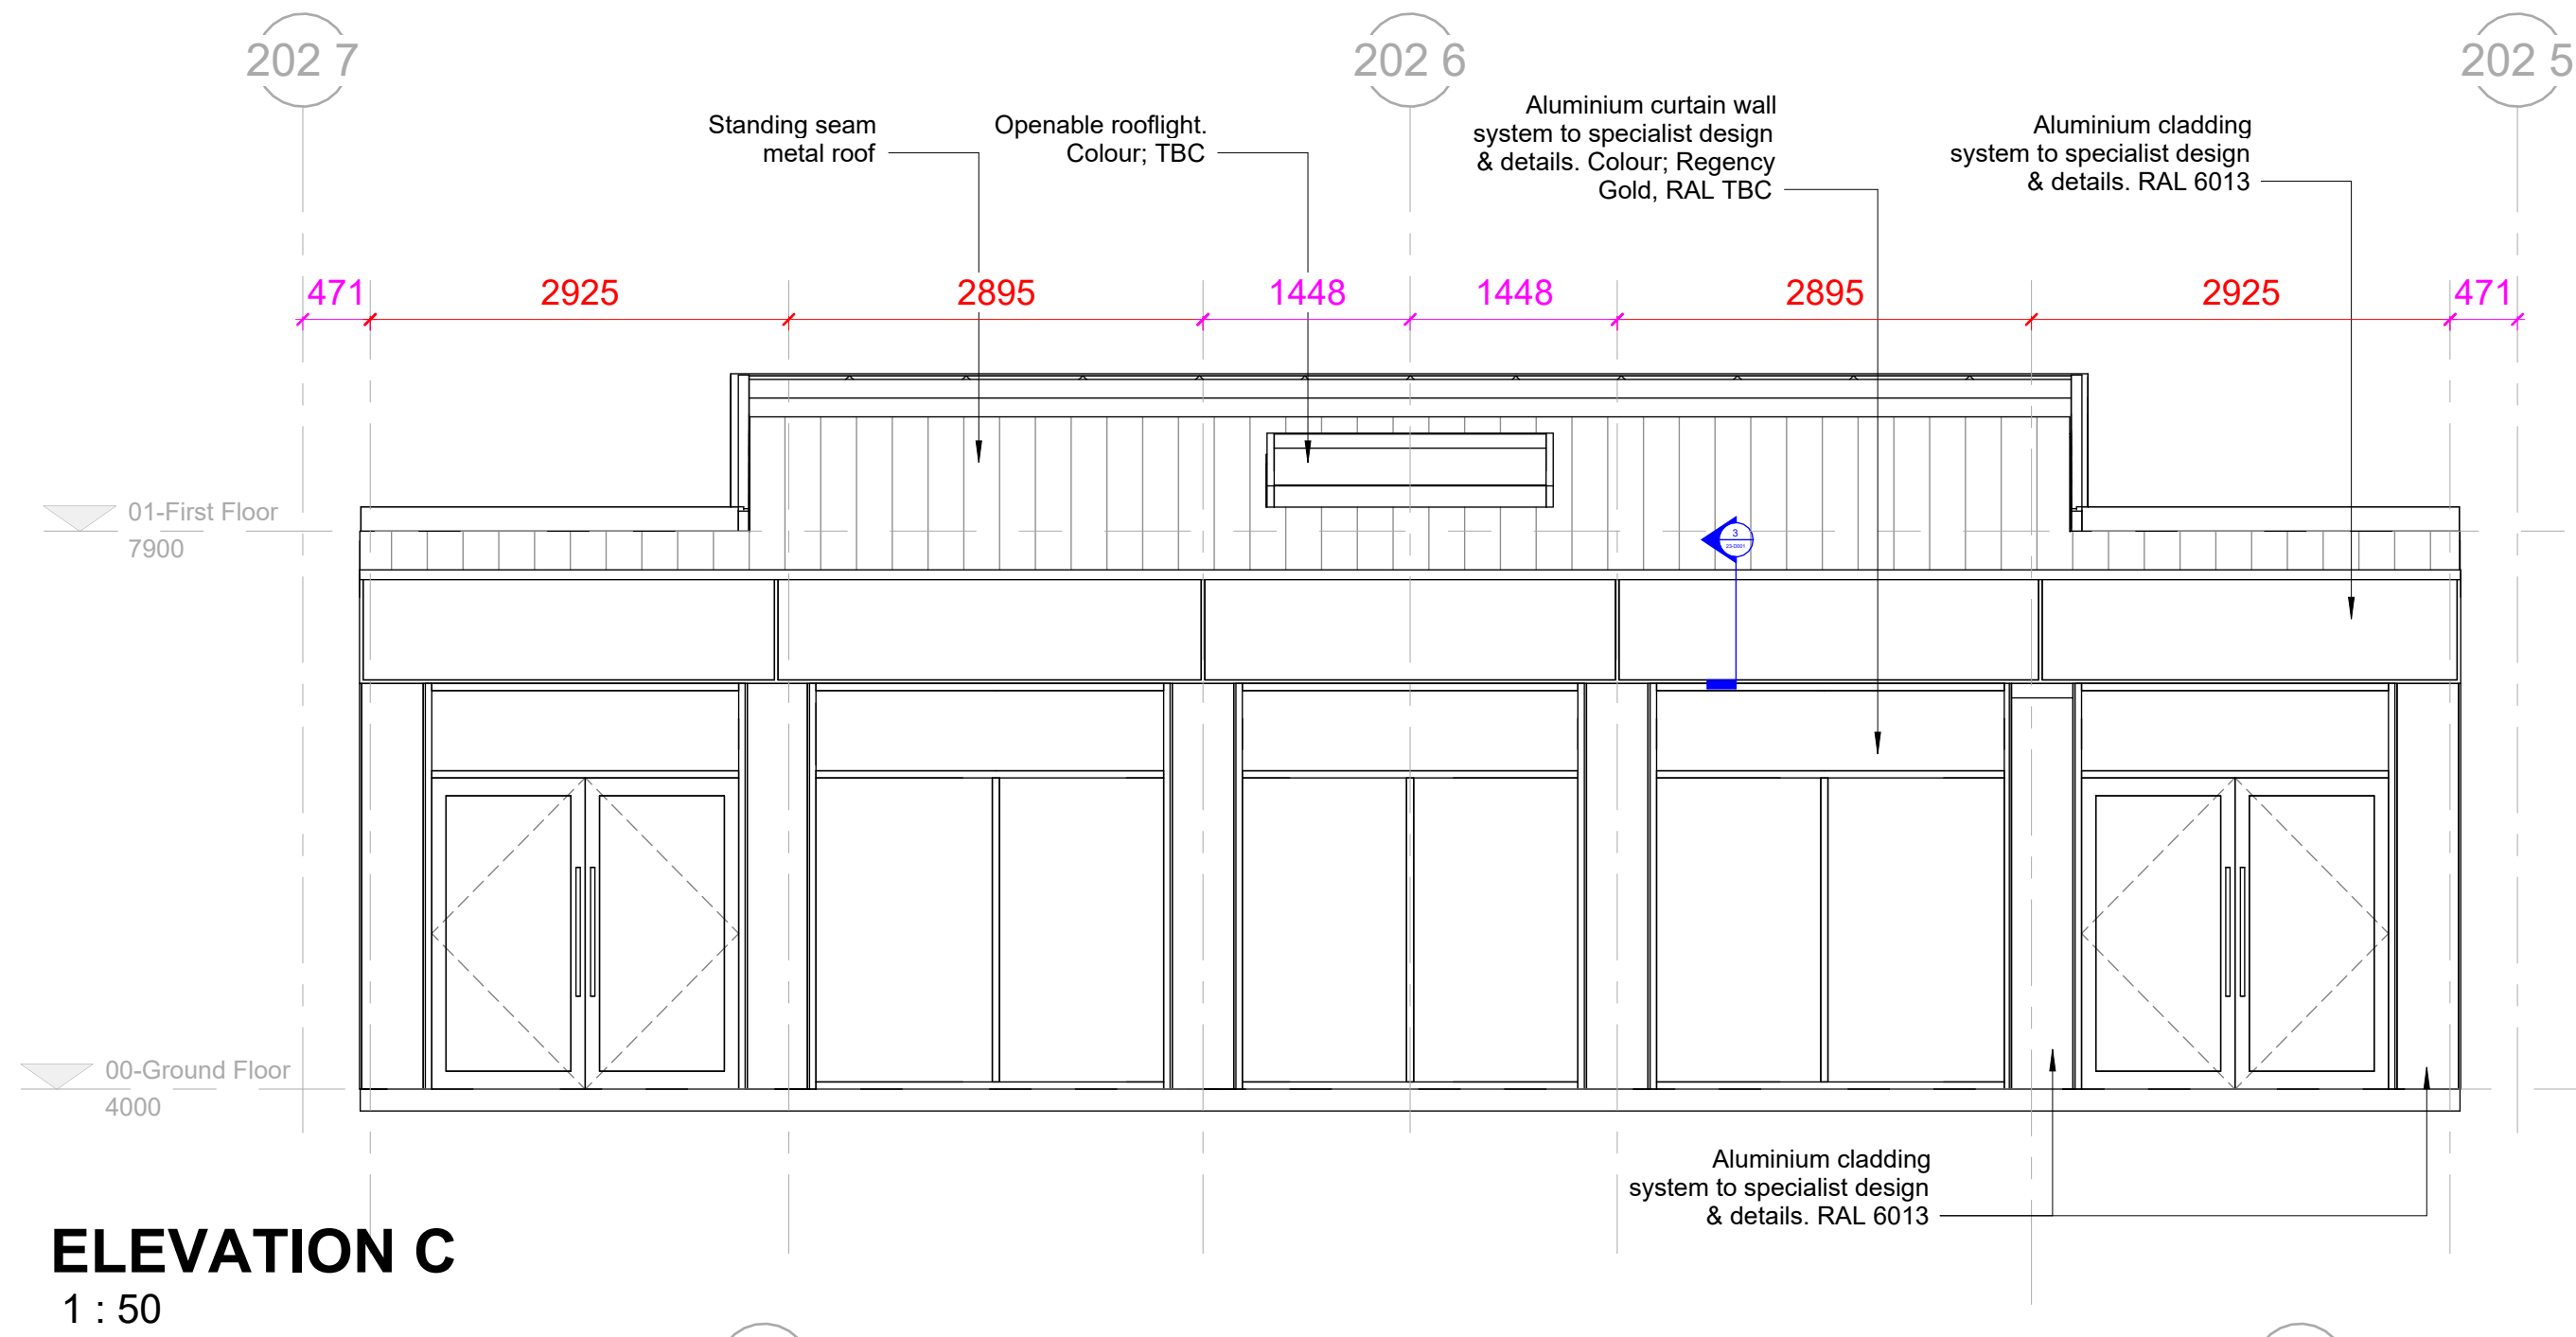
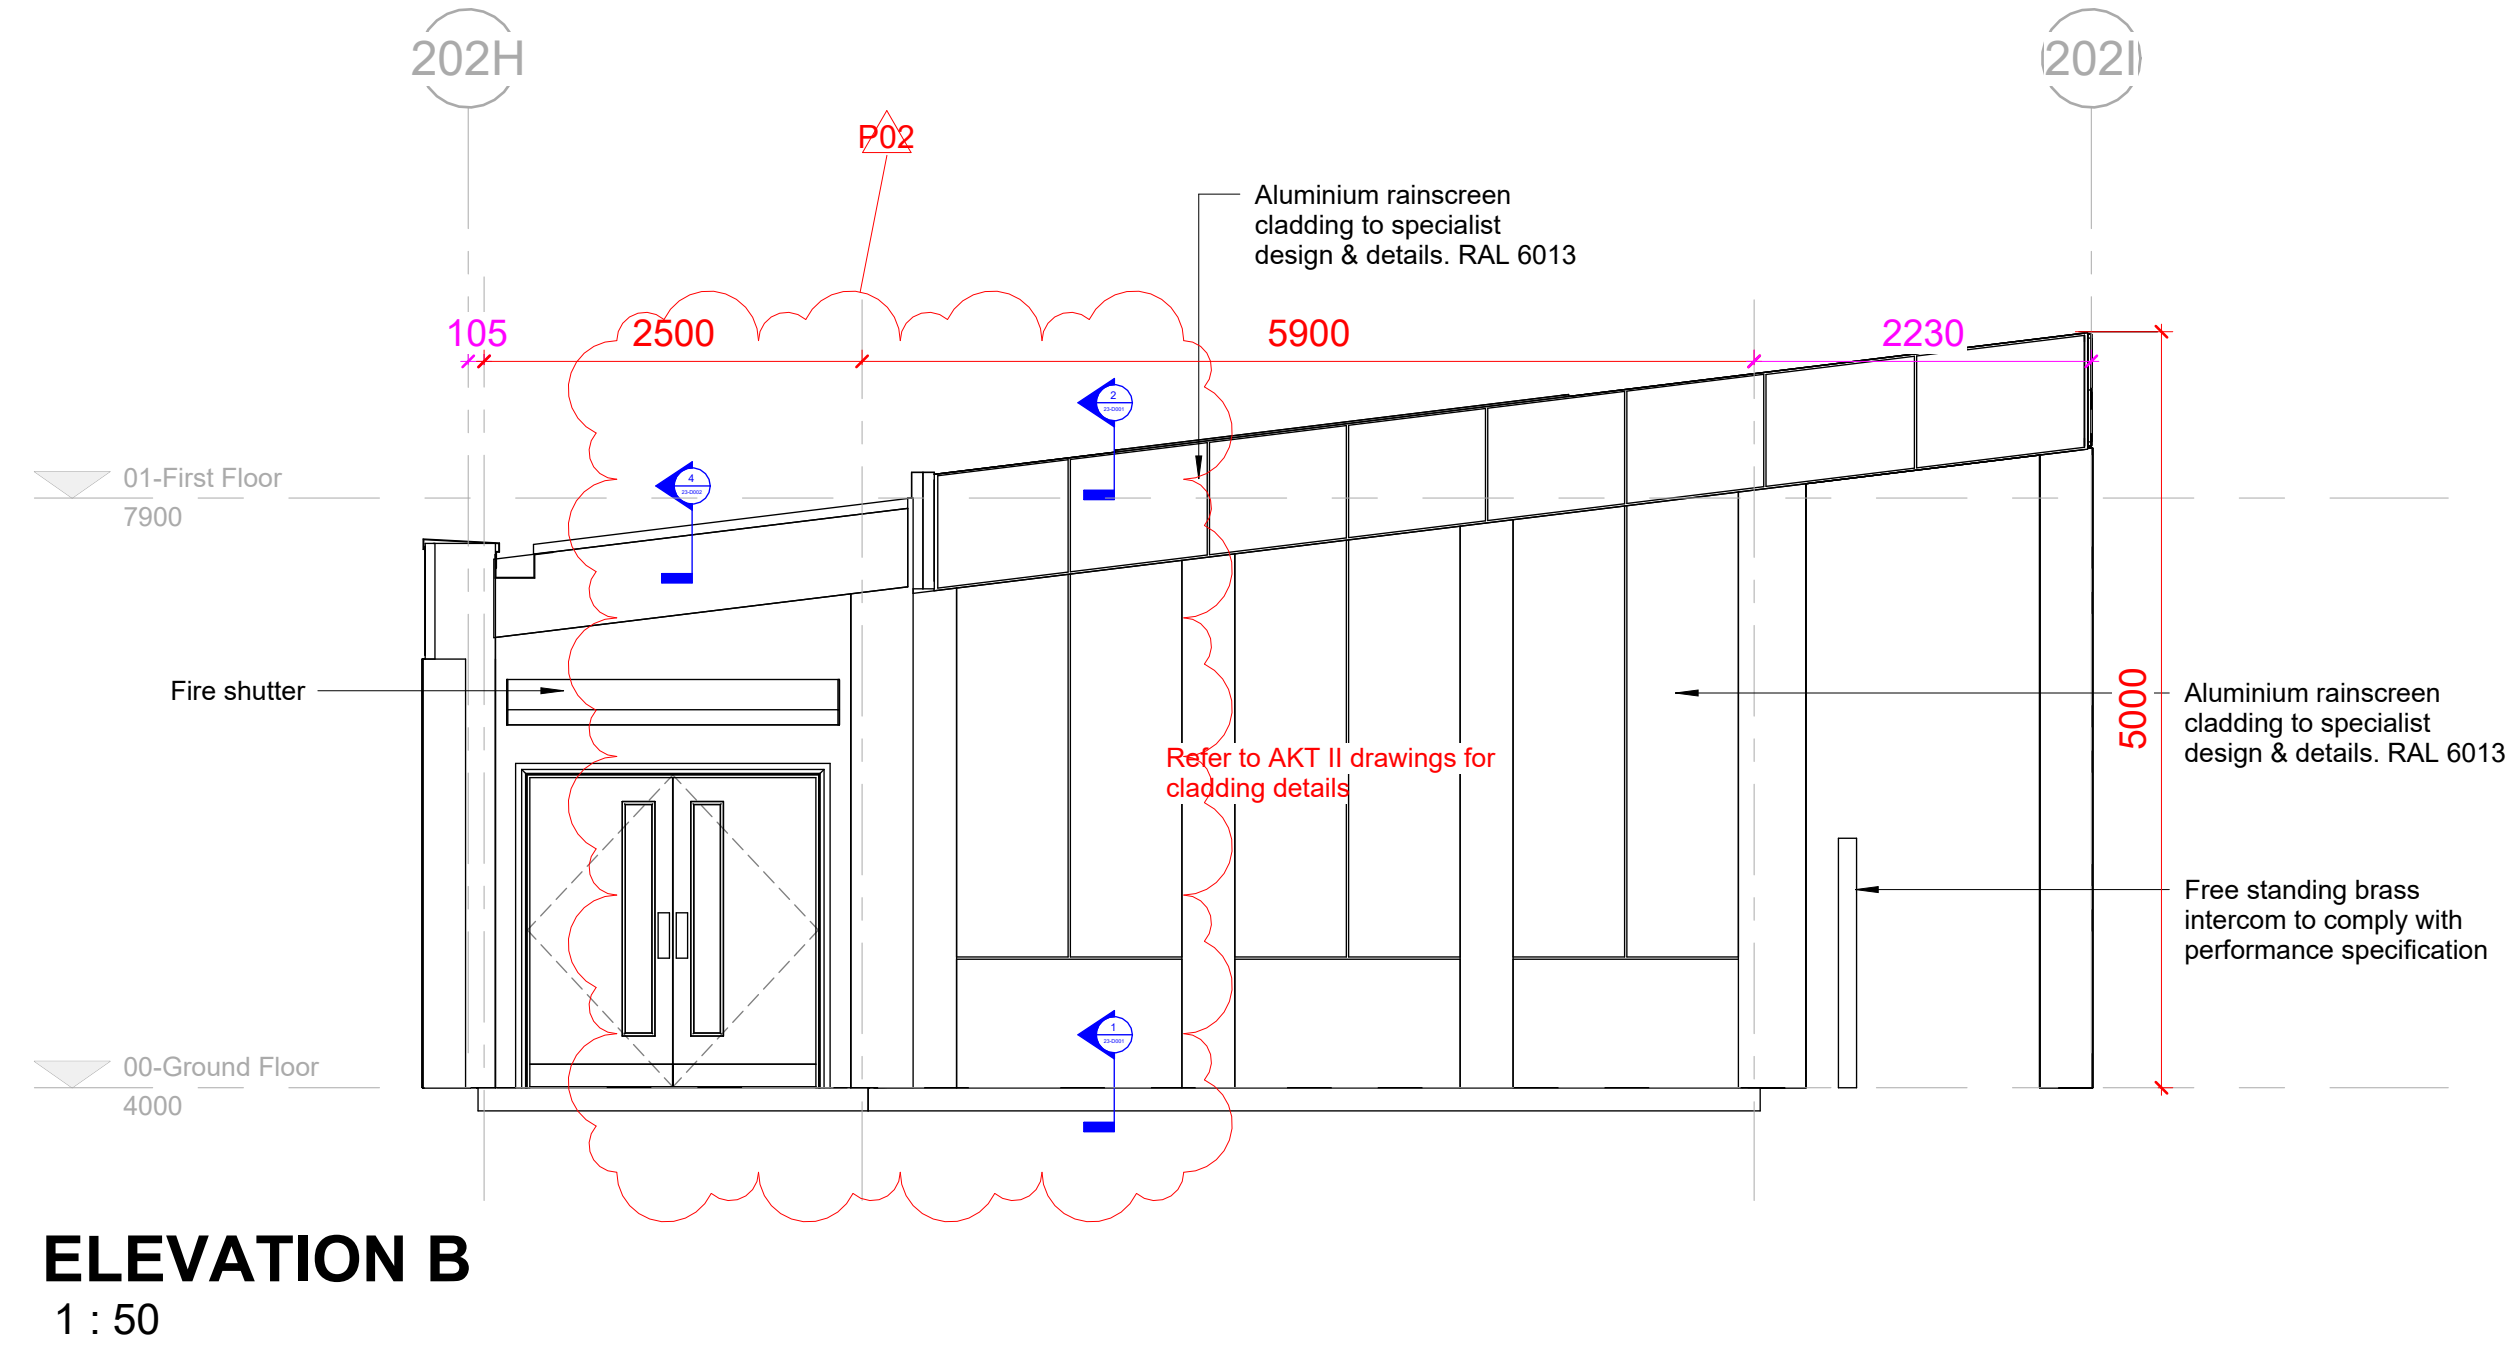
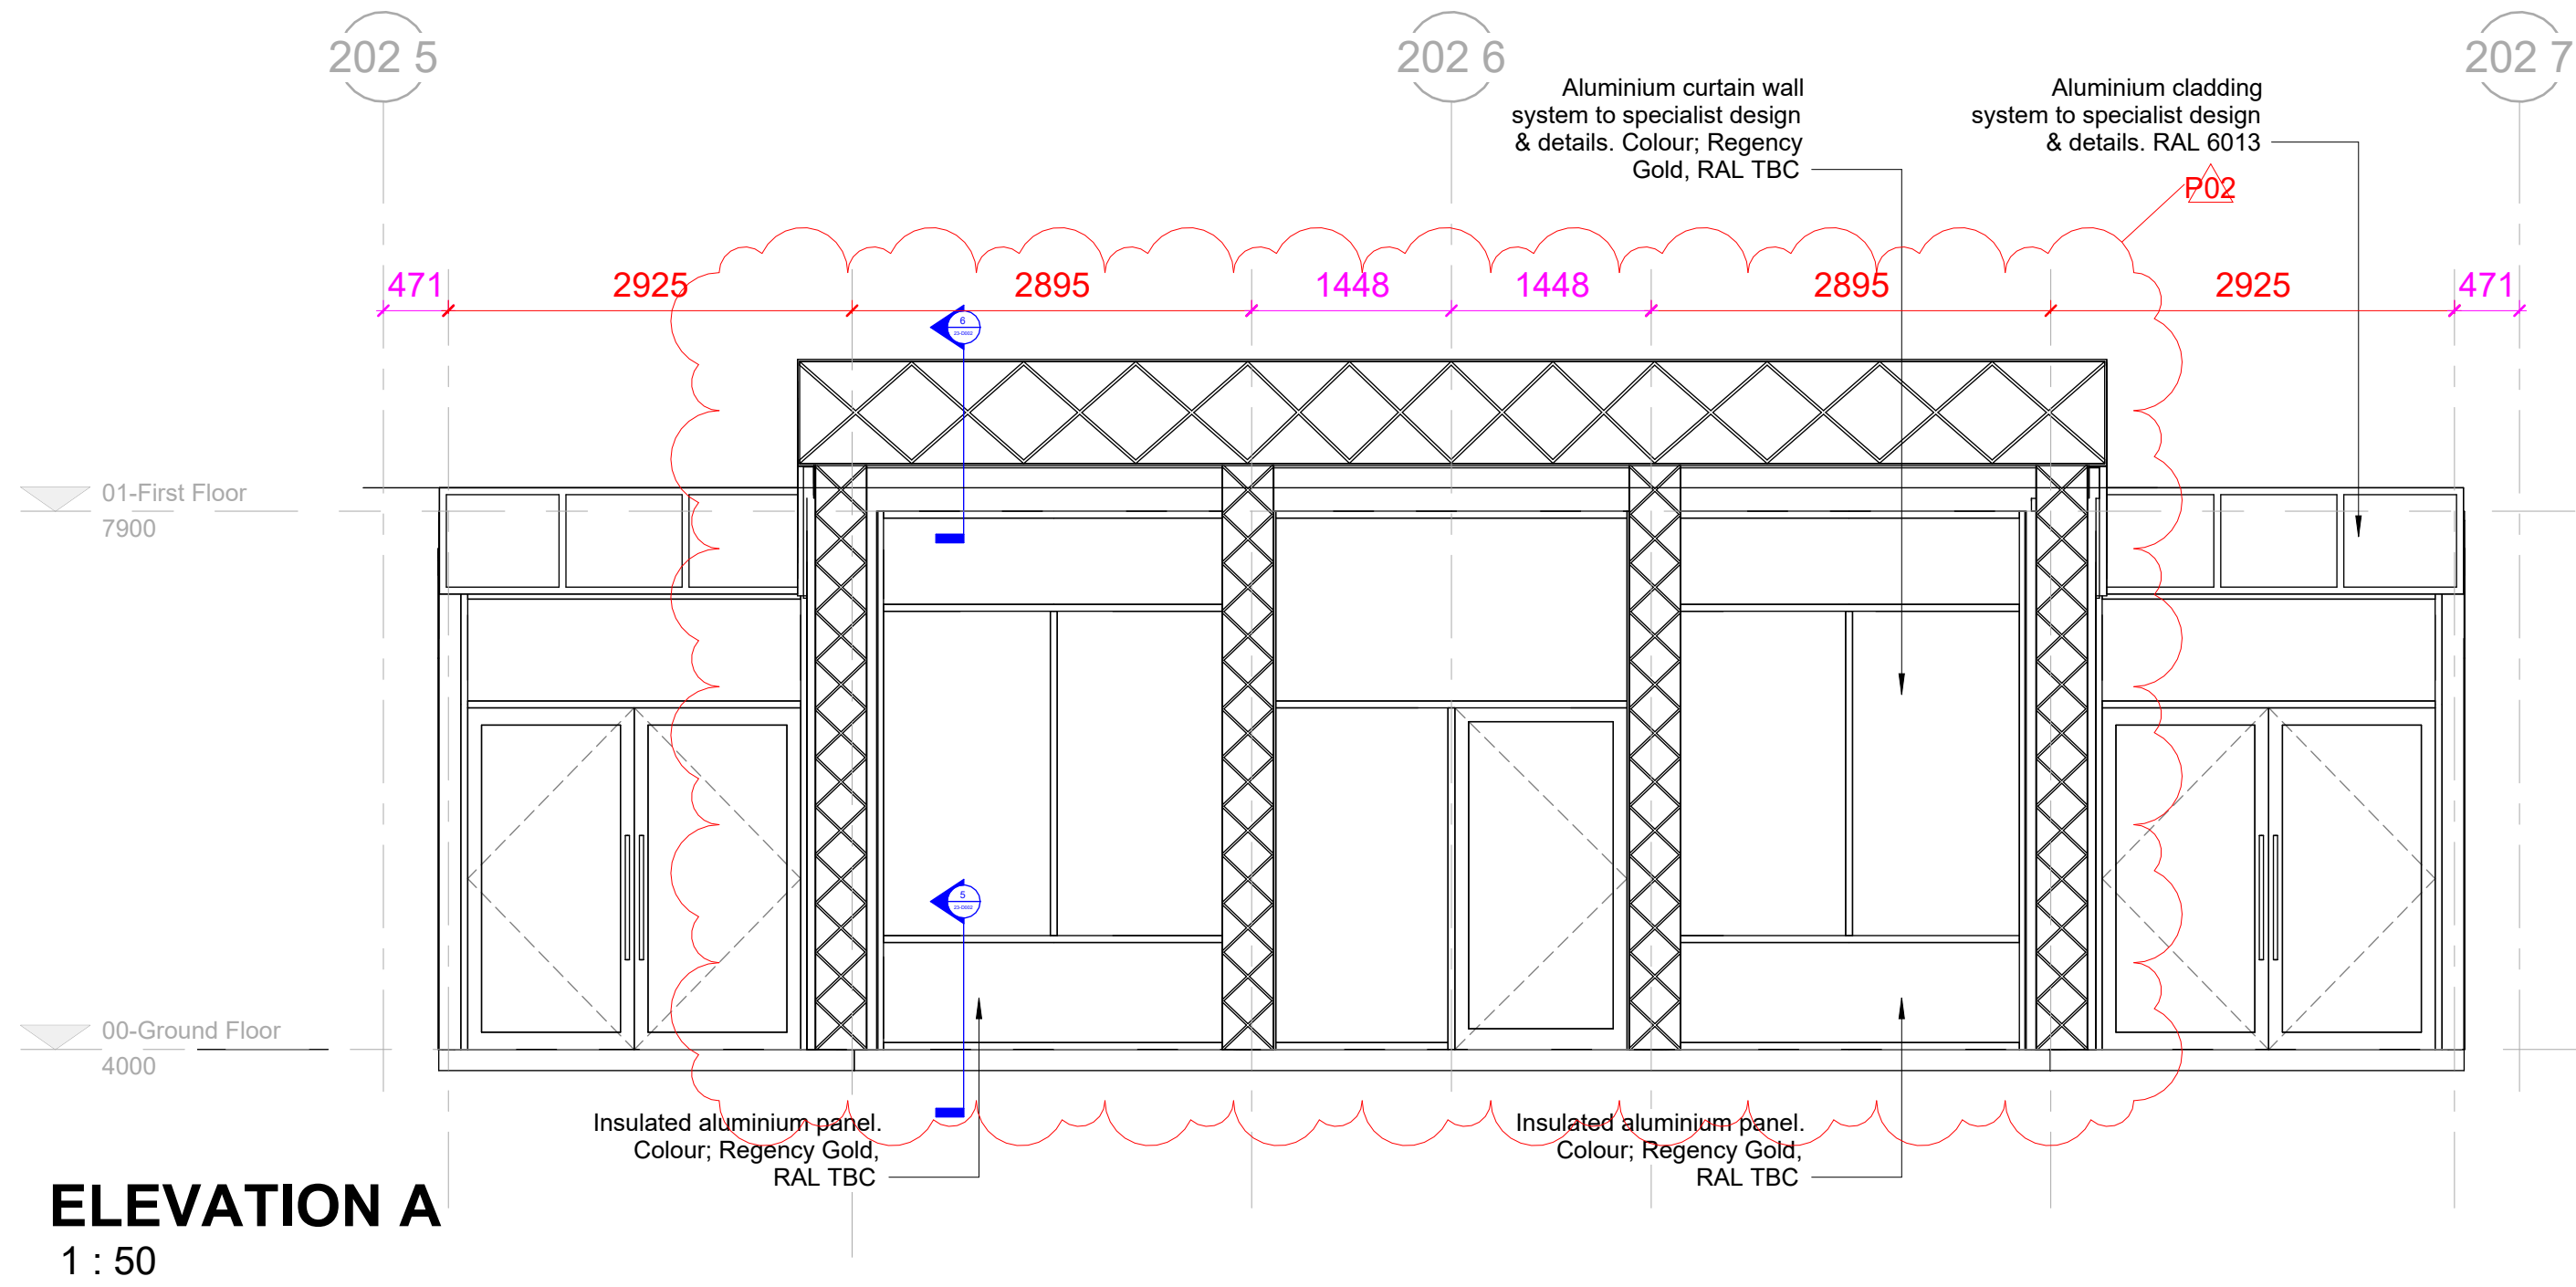


P02	02.06.23	PRELIMINARY: section location, free standing intercom and overwing added.	PN	SC
P01	30.03.23	PRELIMINARY	PN	SC
Rev	Date	Description	By	Chk

FOR APPROVAL

JRL MODULAR LIMITED

NEWARK

CARLTON WORKS COSSINGTON ROAD, NEWARK, NG23 8HT
TEL: 01636 821645 www.jrlgroup.co.uk

CLIENT

MIDGARD

PROJECT

BRENT CROSS TOWN - PAVILION
PLOT 202 - PAVILION, BRENT CROSS, NW 1AJ

TYPE

PLOT 202 - PAVILION
PROPOSED ELEVATIONS & SECTION

CREATION

07 JAN 2023

SCALE

As indicated

OR

PN

OR

CH

OR

SC

STATUS

S3

DRAWING NO.

BXS- M2012- PRJ002- Y- MOD- DR- 20-E001- ZZ

Rev (Plot) (Project) (Rev) (Date) (Author) (Type) (Content) (Type) (Date) (Number) (Level)

DATE

02

REVISION

P02

REVISION

REVISION

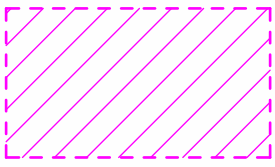


12mm Plywood

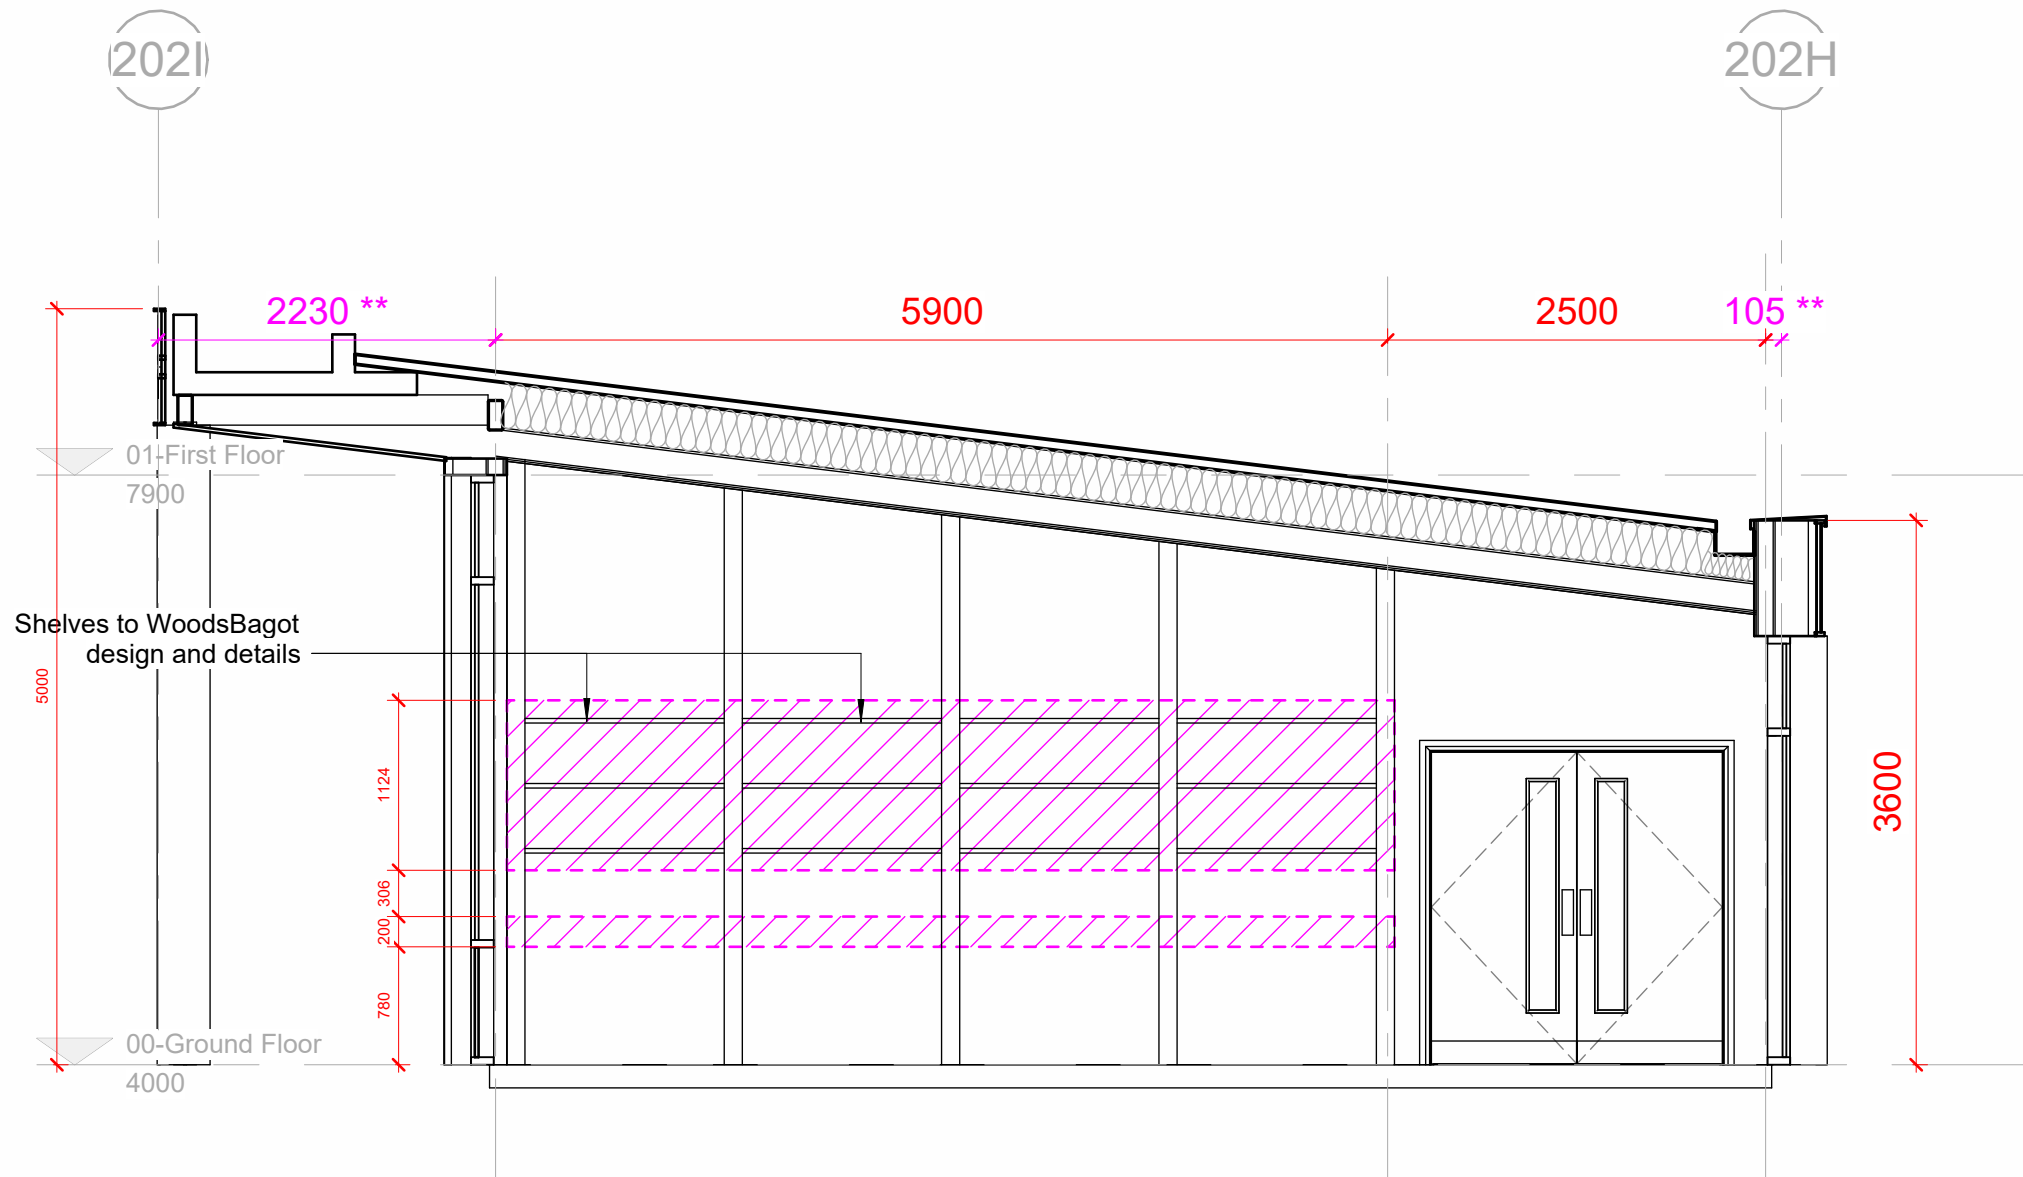


ELEVATION A
1 : 50

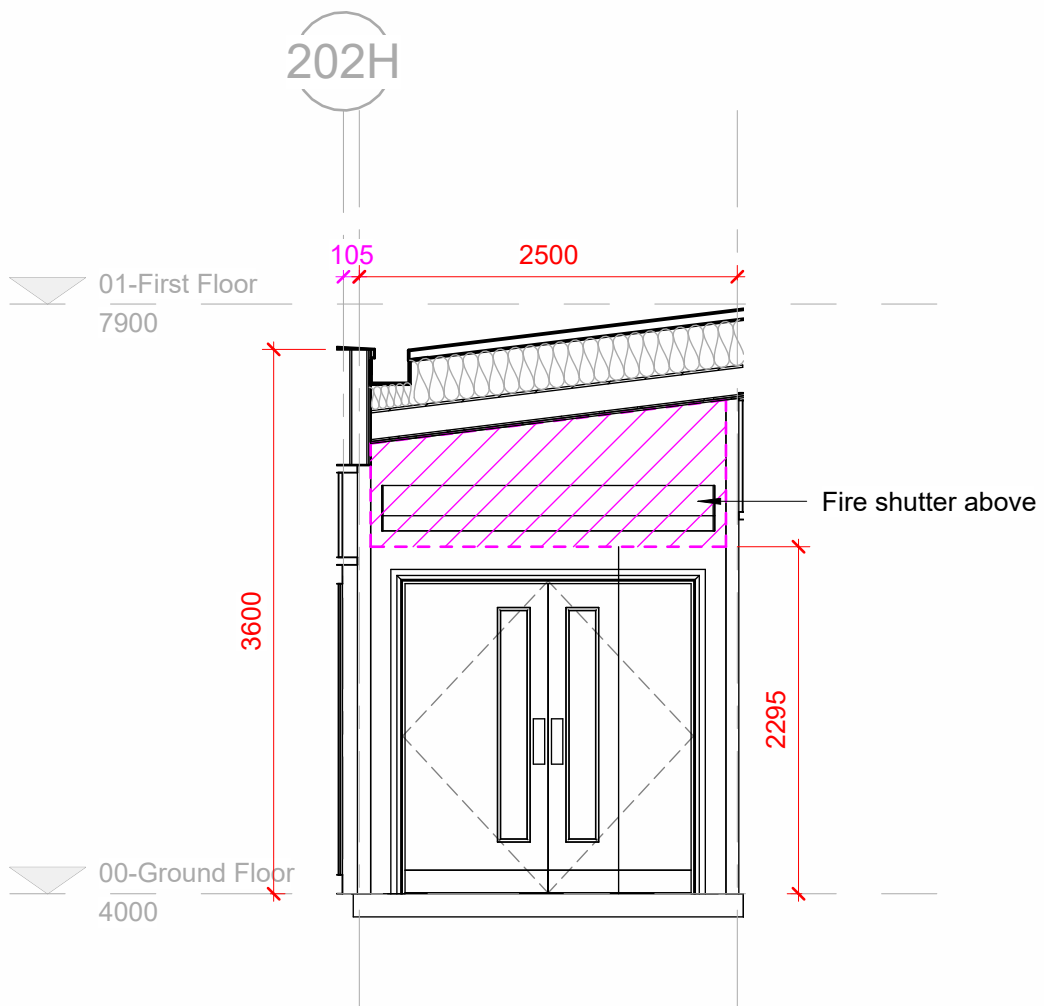


ELEVATION B
1 : 50

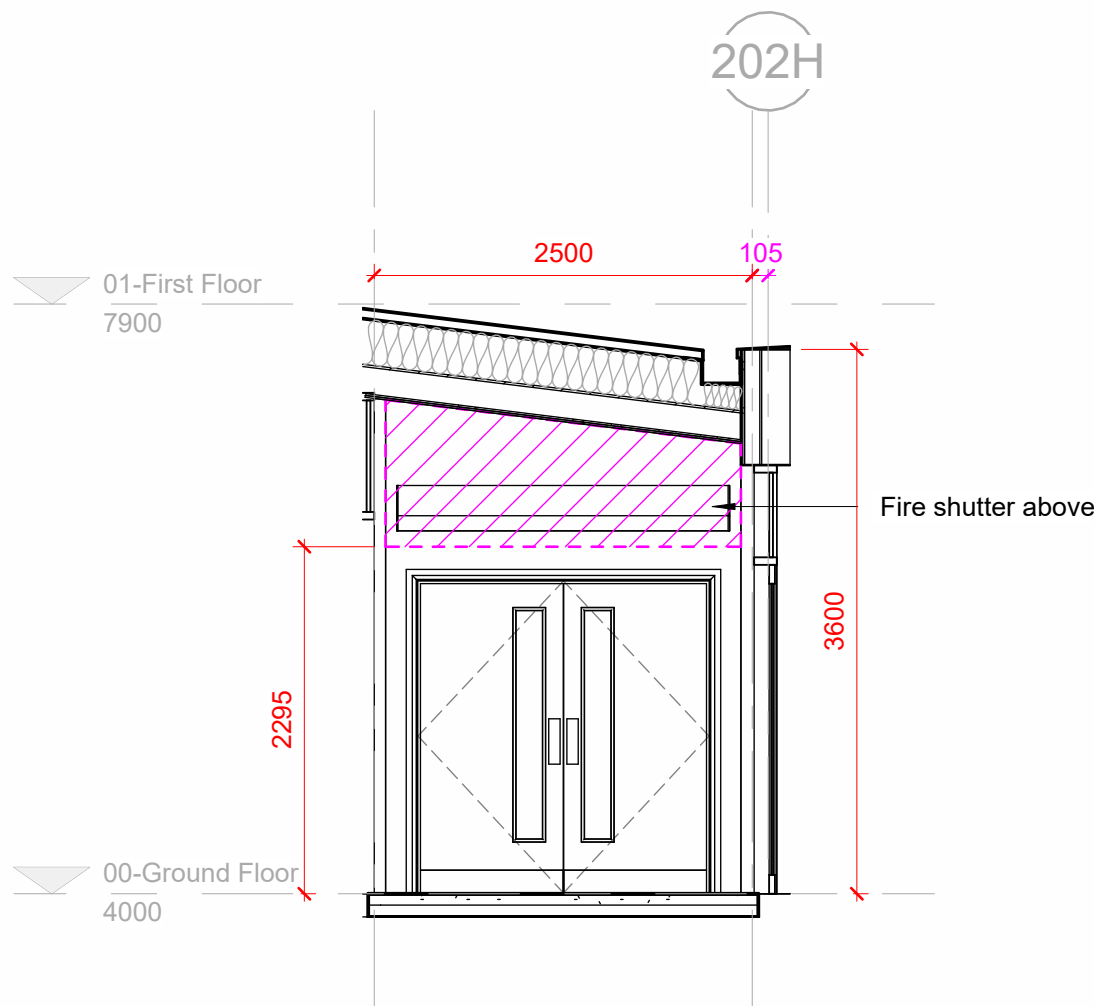

ELEVATION C
1 : 50

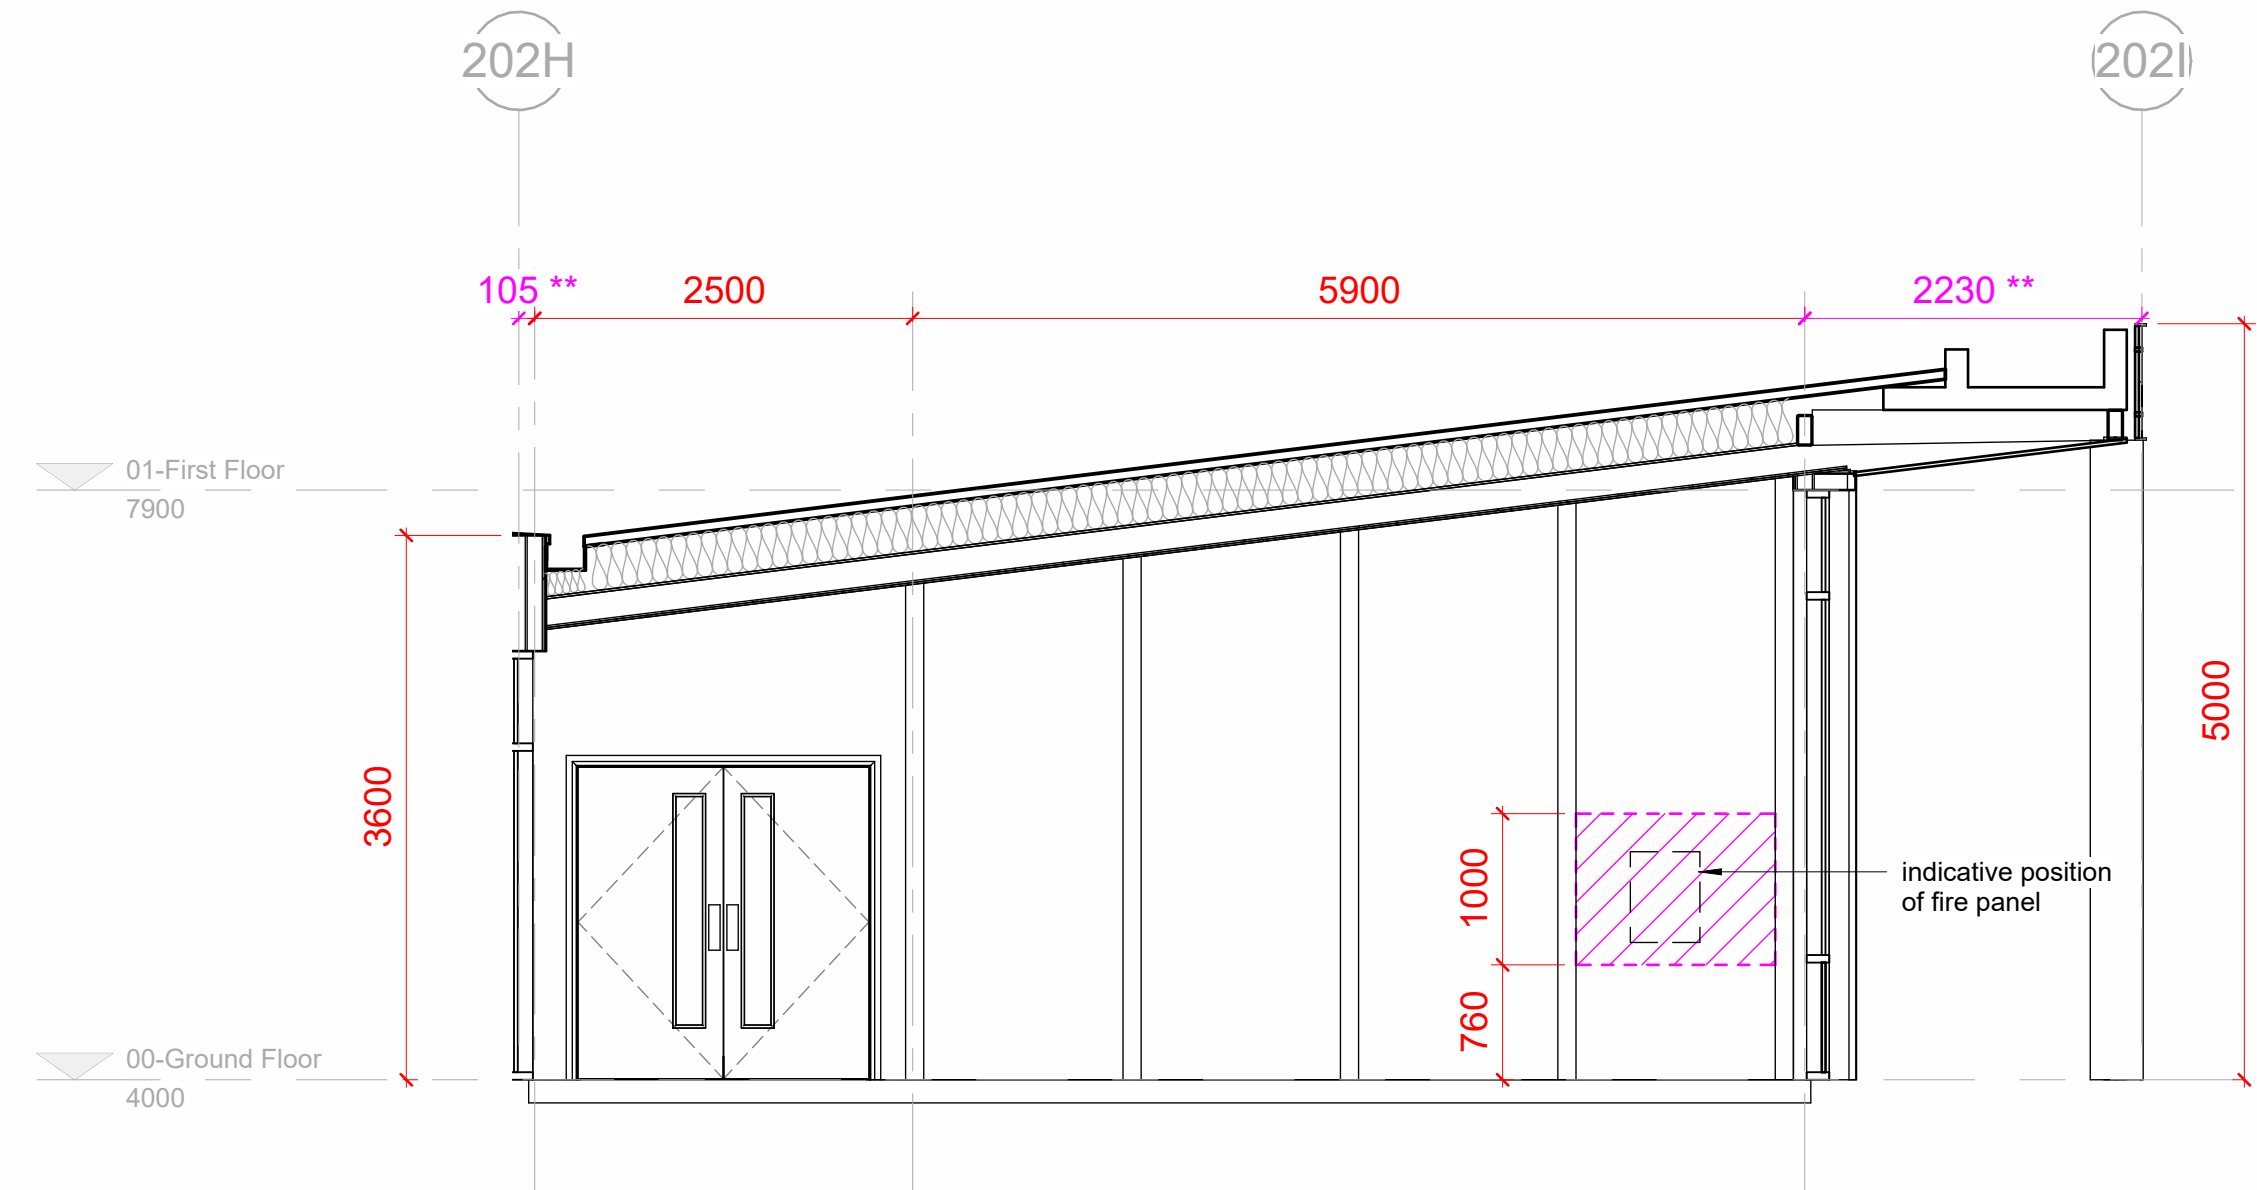


ELEVATION D
1 : 50


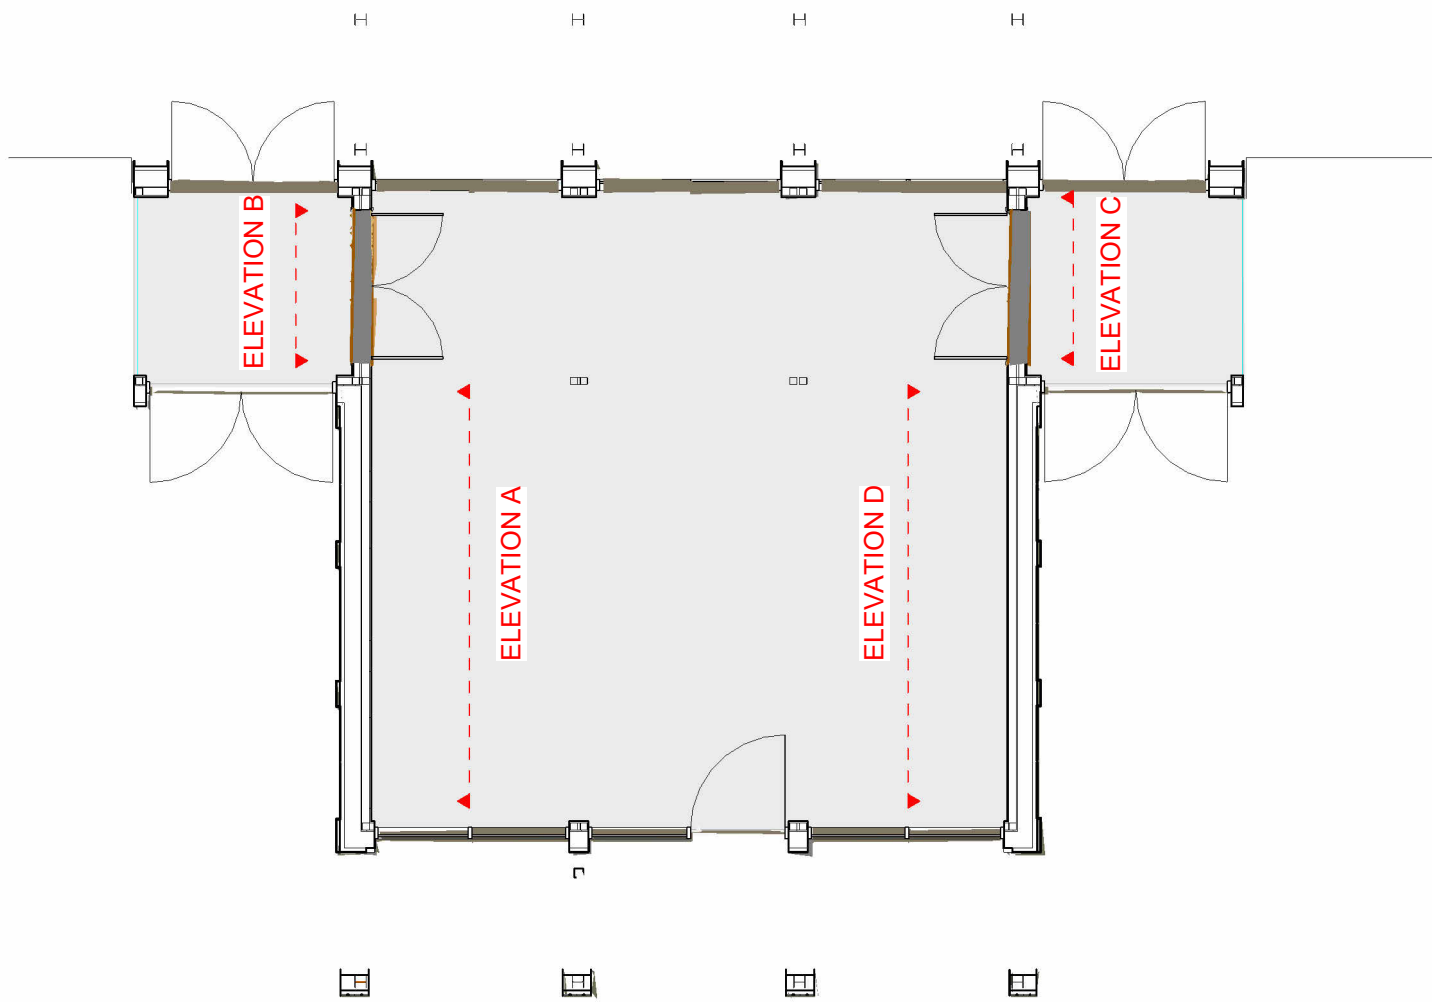


KEY PLAN
1 : 100

P01	02.06.23	PRELIMINARY	PN	SC
Rev	Date	Description	By	Chk
FOR APPROVAL				
JRL MODULAR LIMITED				
NEWARK				
CARLTON WORKS COSSINGTON ROAD, NEWARK, NG23 8HT TEL: 01636 821645 www.jrlgroup.co.uk				
CLIENT MIDGARD				
PROJECT BRENT CROSS TOWN - PAVILION PLOT 202 - PAVILION, BRENT CROSS, NW 1AJ				
TYPE PLOT 202 - PAVILION INTERNAL ELEVATIONS-PATTESSING				
CREATION	SCALE 1:1	OR	CH	STATUS
28 APR 2023	As indicated	PN	PN	S3
DRAWING NO. BX5-M2012-PRJ002-Y-MOD-DR-20-E002-ZZ				
SHE (Plot) (Project) (Rev) (Date) (Author) (Type) (Content) (Spec) (Drawing) (Level)				
COPED TO:				
P01				
REVISION				
© COPYRIGHT. ALL RIGHTS RESERVED. THIS DRAWING MUST BE READ IN CONJUNCTION WITH ALL OTHER RELEVANT DRAWINGS AND INFORMATION. ANY DISCREPANCIES MUST BE REPORTED TO JRL MODULAR LTD IMMEDIATELY. THIS DRAWING OR INFORMATION MUST NOT BE USED FOR CONSTRUCTION UNLESS EXPRESSLY ISSUED FOR CONSTRUCTION. DO NOT SCALE OFF DRAWINGS. USE DISPLAYED DIMENSIONS.				

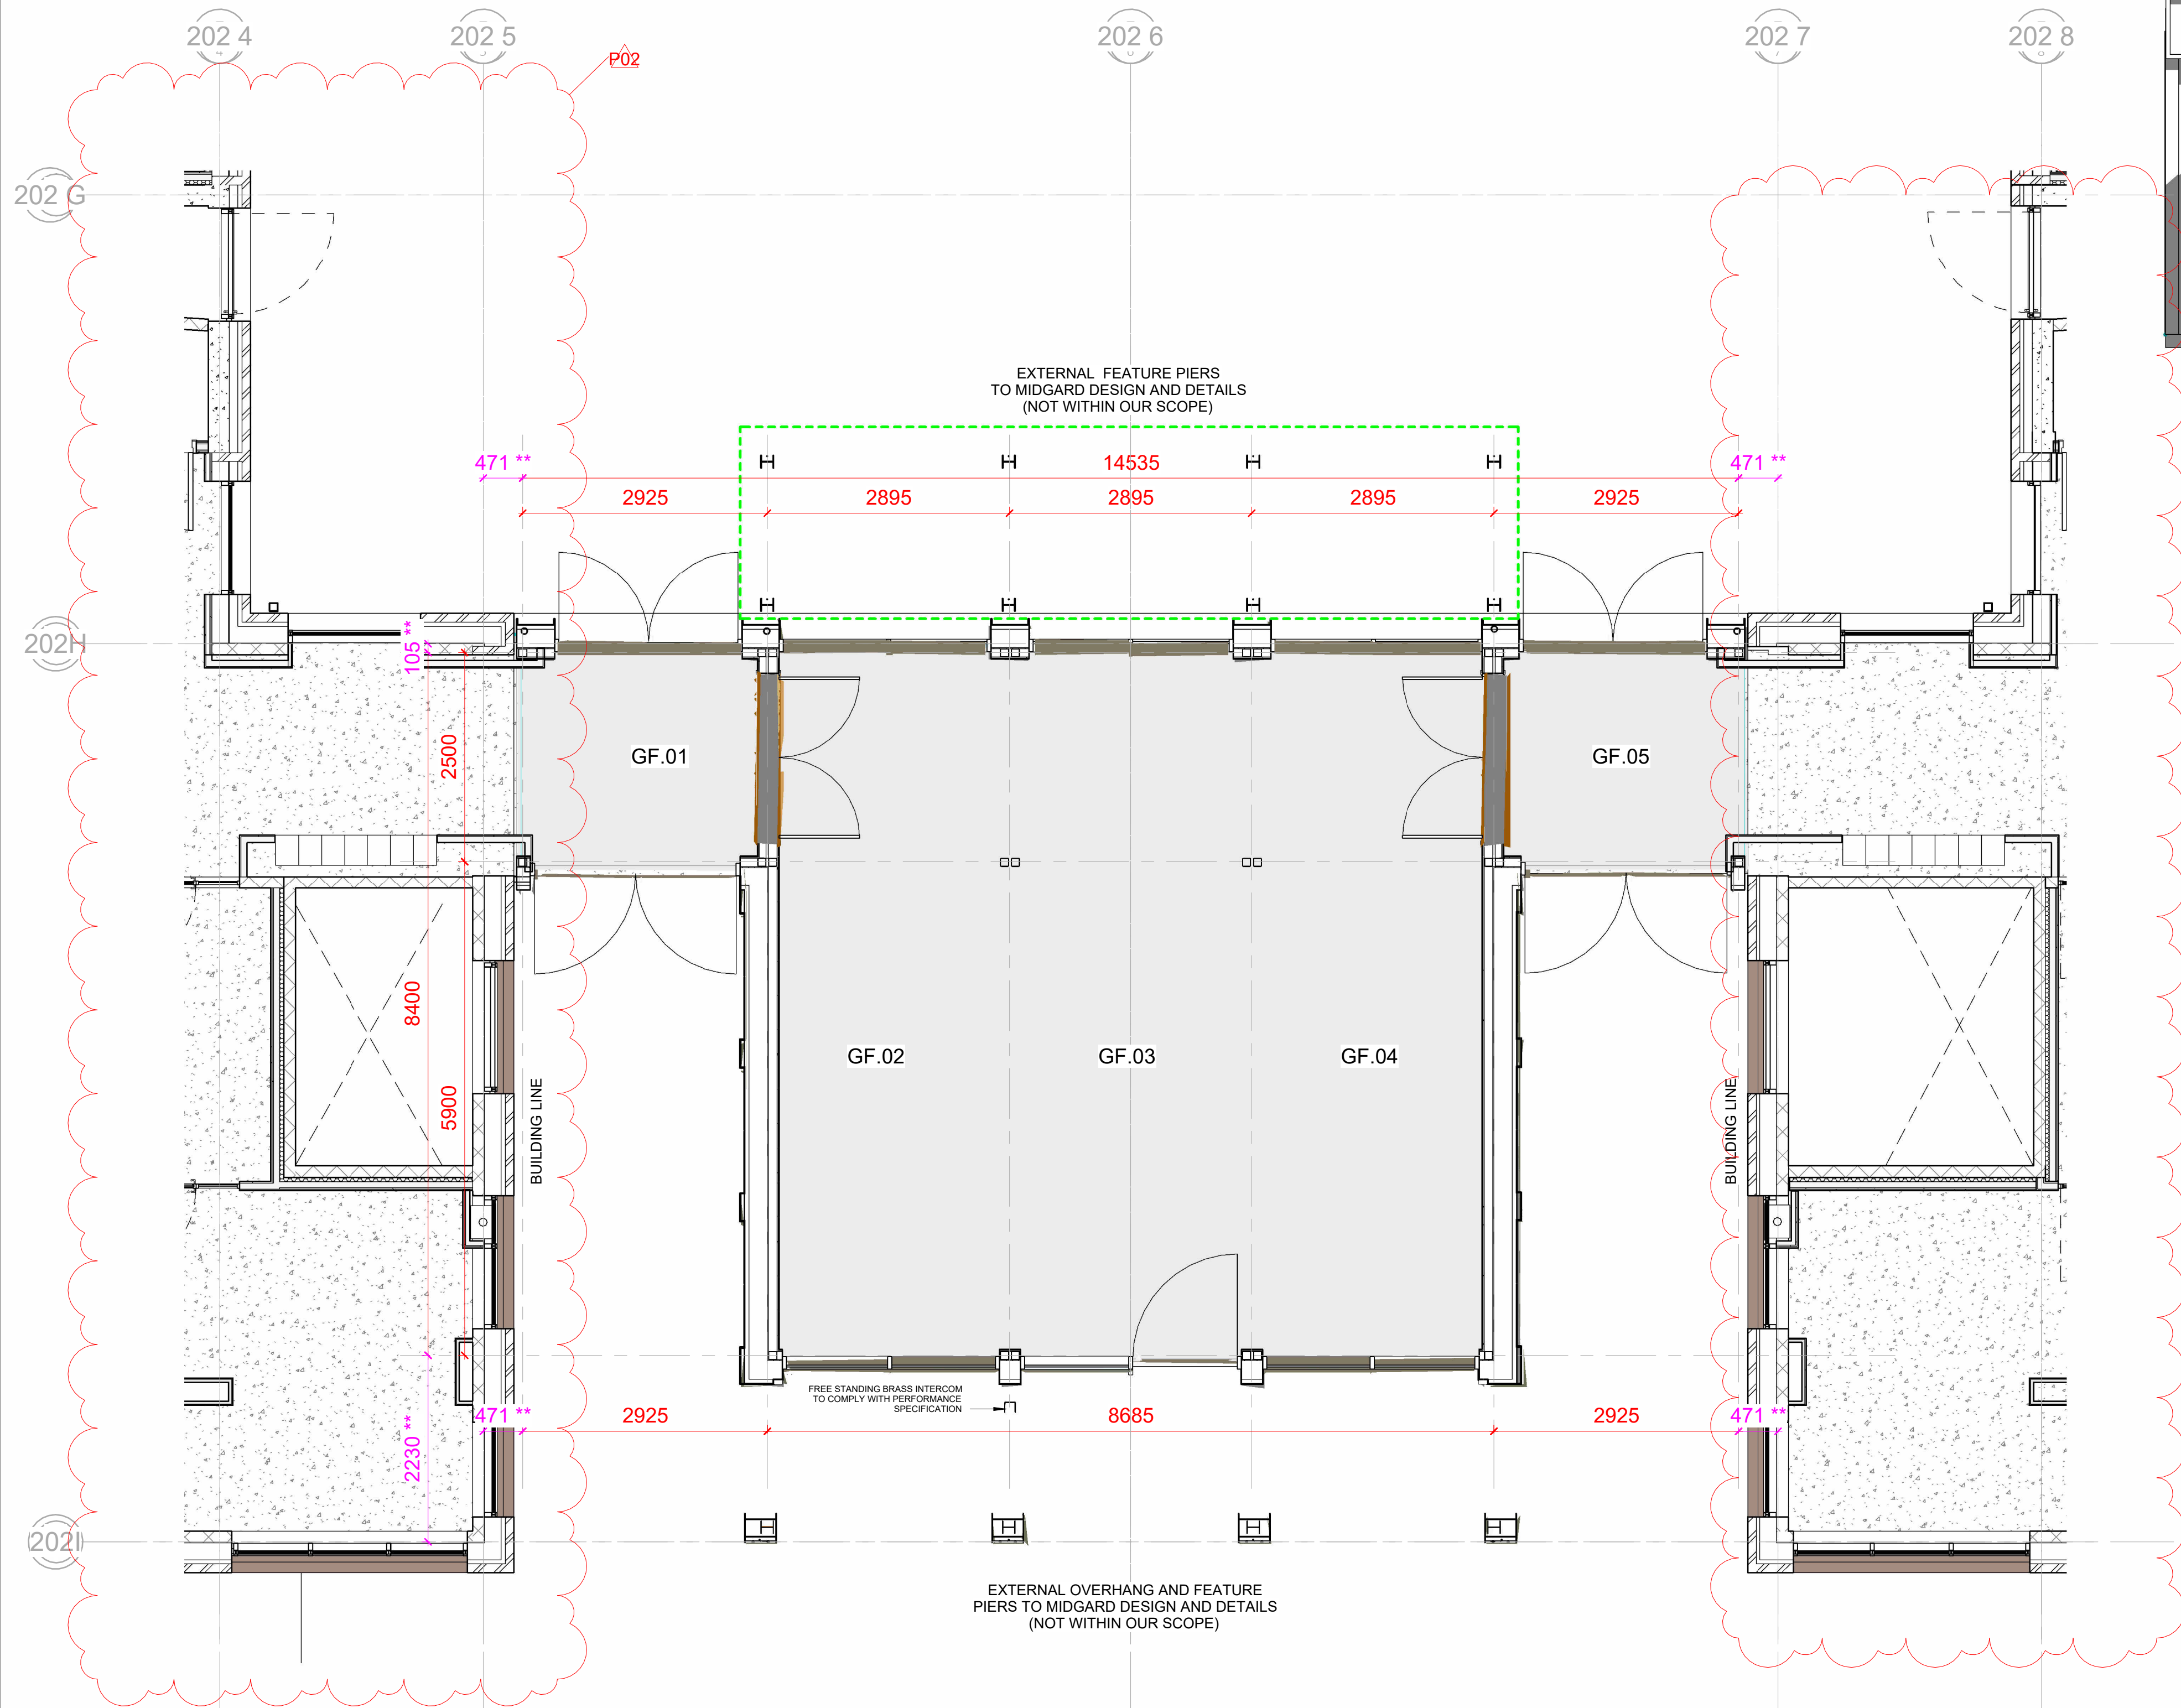

PROPOSED FLOOR PLAN
1 : 50

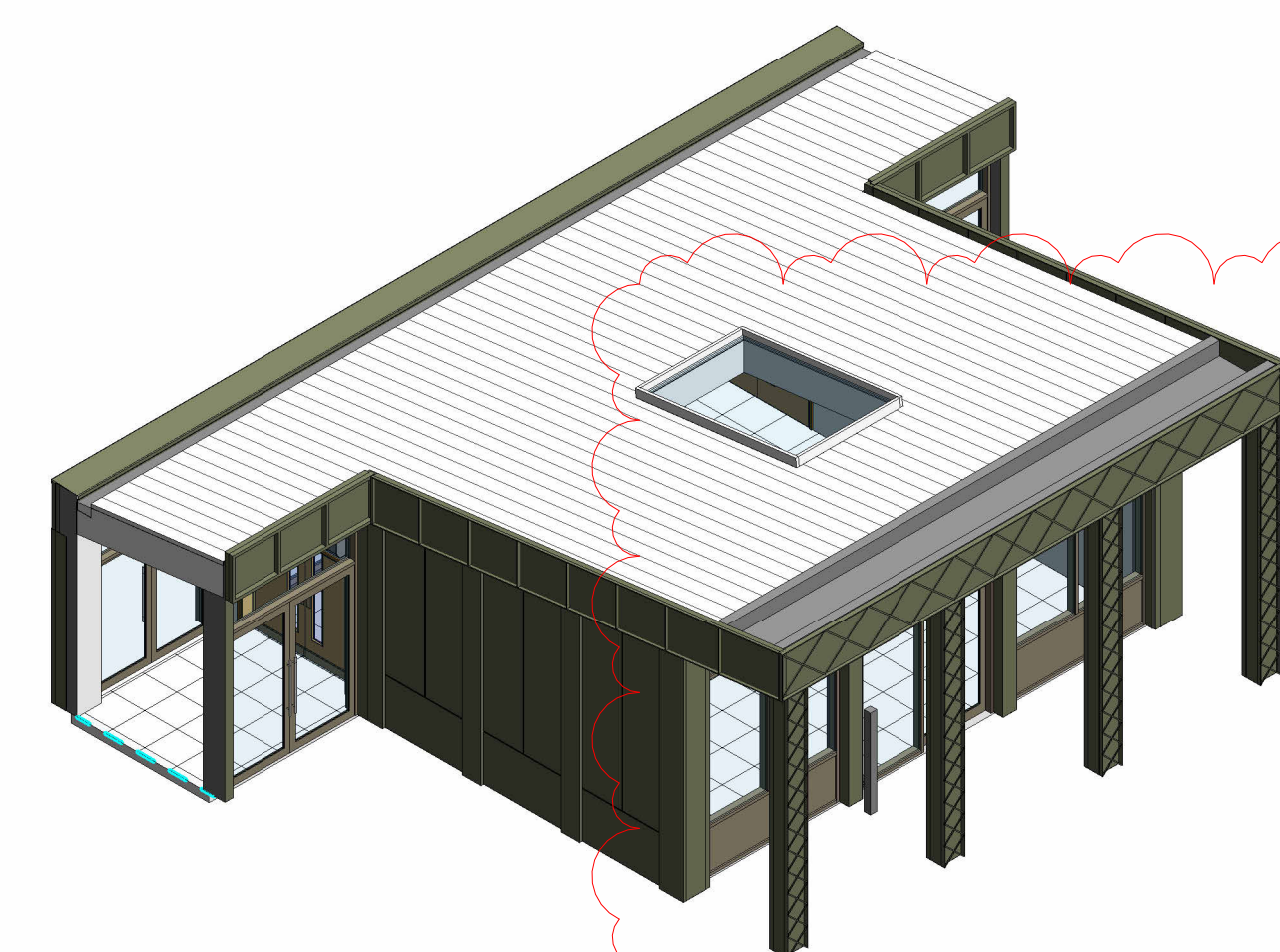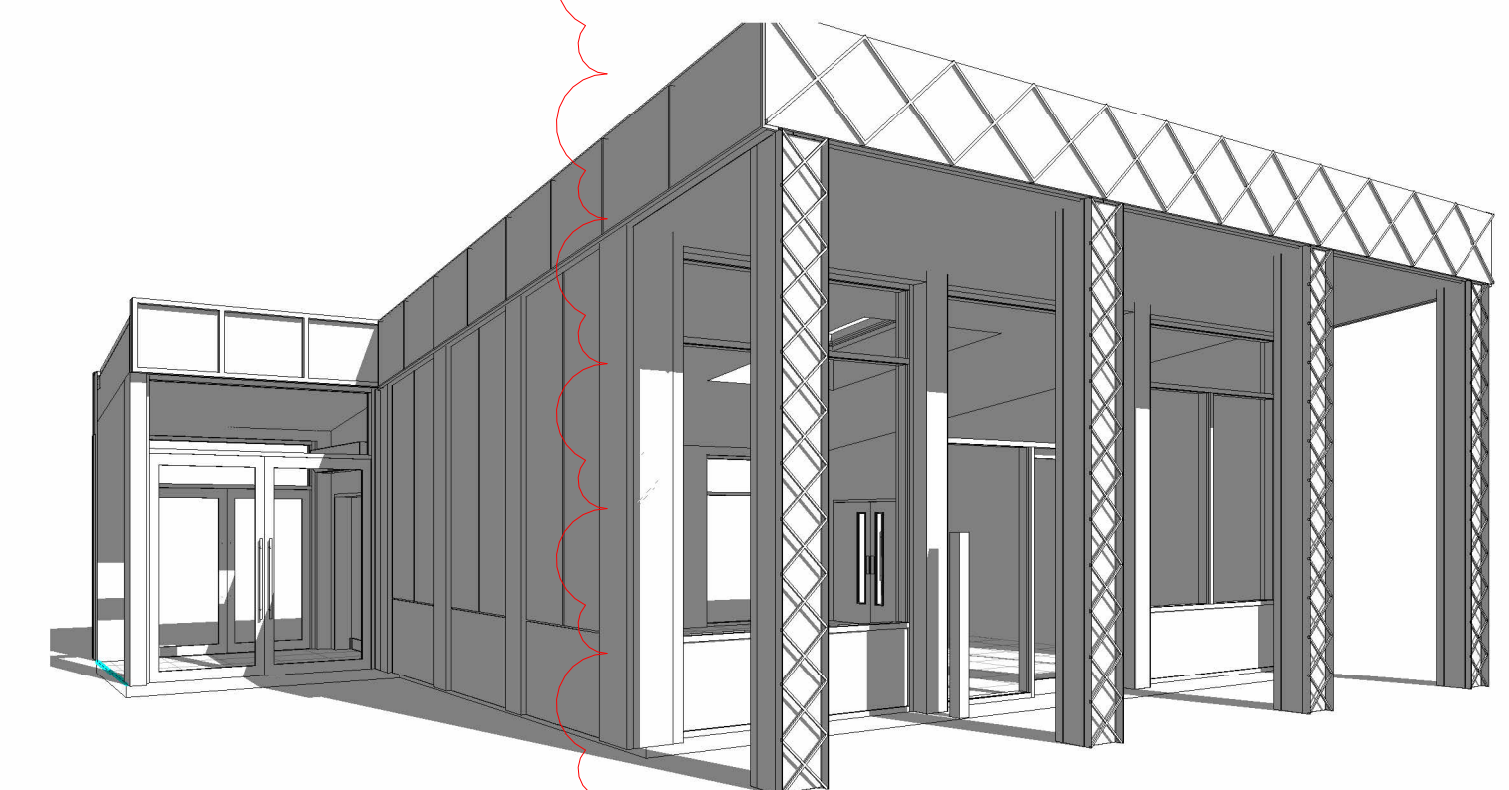

P02	02.06.23	PRELIMINARY: Drawing updated as per WCA comment	PN	SC
P01	30.03.23	PRELIMINARY	PN	SC
Rev	Date	Description	By	Chk

FOR APPROVAL

JRL
MODULAR
LIMITED

NEWARK

CARLTON WORKS COSSINGTON ROAD, NEWARK, NG23 8HT
TEL: 01636 821645 www.jrlgroup.co.uk

CLIENT
MIDGARD


PROJECT
BRENT CROSS TOWN - PAVILION
PLOT 202 - PAVILION, BRENT CROSS, NW 1AJ

TITLE
PLOT 202 - PAVILION
PROPOSED GENERAL ARRANGEMENT PLAN

CREATION	SCALE 1:50	OR	CH	STATUS
07 JAN 2023	1:50	PN	SC	S3

DRAWING NO.
BXS-M2012-PRJ002-Y-MOD-DR-20-P001-GF
Rev (Plot) (Project) (Rev) (Date) (Author) (Type) (Content) (Type) (Drawing) (Level)
C:\BXS\02\2012\PRJ002\Y\MOD\DR\20\BXS-M2012-PRJ002-Y-MOD-DR-20-P001-GF.dwg


© COPYRIGHT ALL RIGHTS RESERVED.
THIS DRAWING MUST BE READ IN CONJUNCTION WITH ALL OTHER RELEVANT DRAWINGS AND INFORMATION.
ANY DIMENSIONS MUST BE REPORTED TO AS SHOWN ON THE DRAWING.
THE DRAWING OR INFORMATION MUST NOT BE USED FOR CONSTRUCTION UNLESS EXPRESSLY ISSUED FOR CONSTRUCTION.
DO NOT SCALE OFF DRAWINGS. USE DISPLAYED DIMENSIONS.

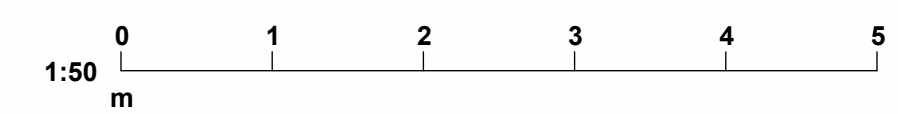

Over all roof build up to achieve u-value of 0.15W/m²K

- 220mm Rockwool Duo Rainscreen slab
- Aluminium rainscreen system to manufacturer design and details
- 12.5mm weatherboard
- Breather membrane (Blue dash)


DETAIL 2
1 : 5

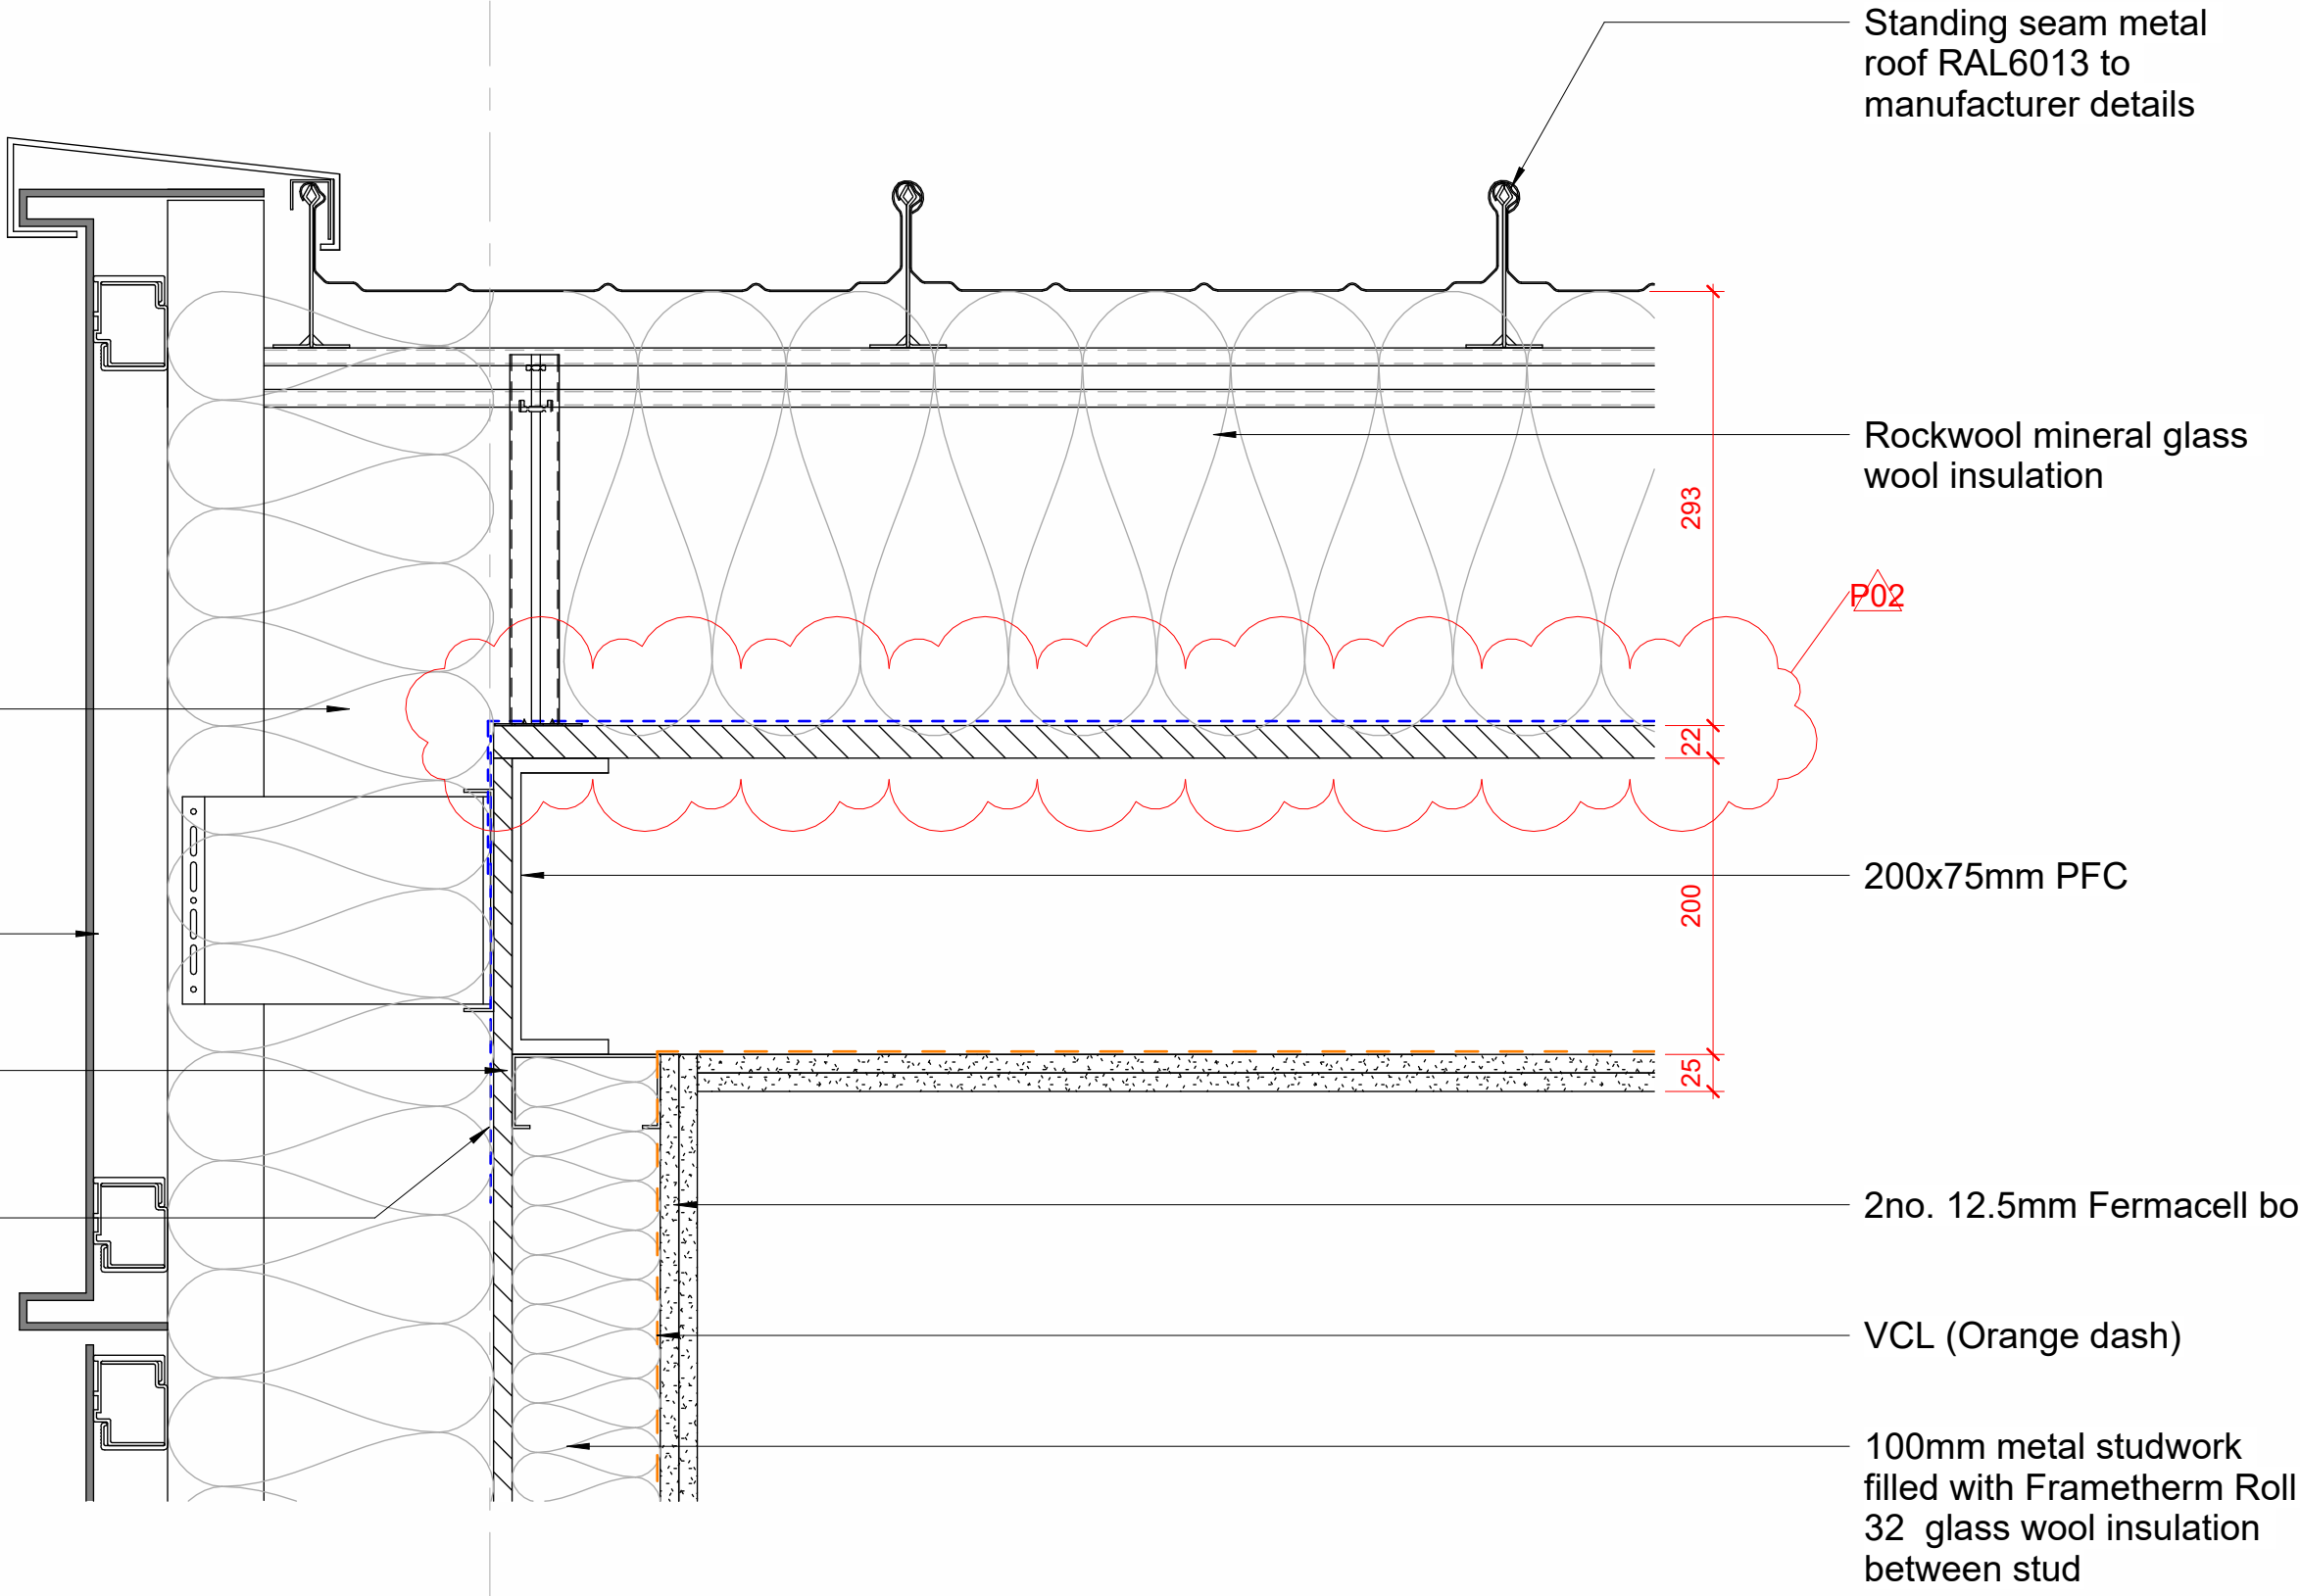

PPC metal box gutter sloping to outlet points. Size, capacity to roofing specialist details. Outlets to have debris guards fitted & gutter to incorporate an overflow as visible indicator of blockage.

- 220mm Rockwool Duo Rainscreen slab
- Aluminium rainscreen system to manufacturer design and details
- Breather membrane (Blue dash)
- Metal RWP running behind removable cladding panels
- 12.5mm weatherboard
- EPDM to finish into curtain wall frame and lapped up module face to minimum 150mm
- Steel shroud
- Reynaers CW50 curtain walling system or similar approved



DETAIL 3
1 : 5

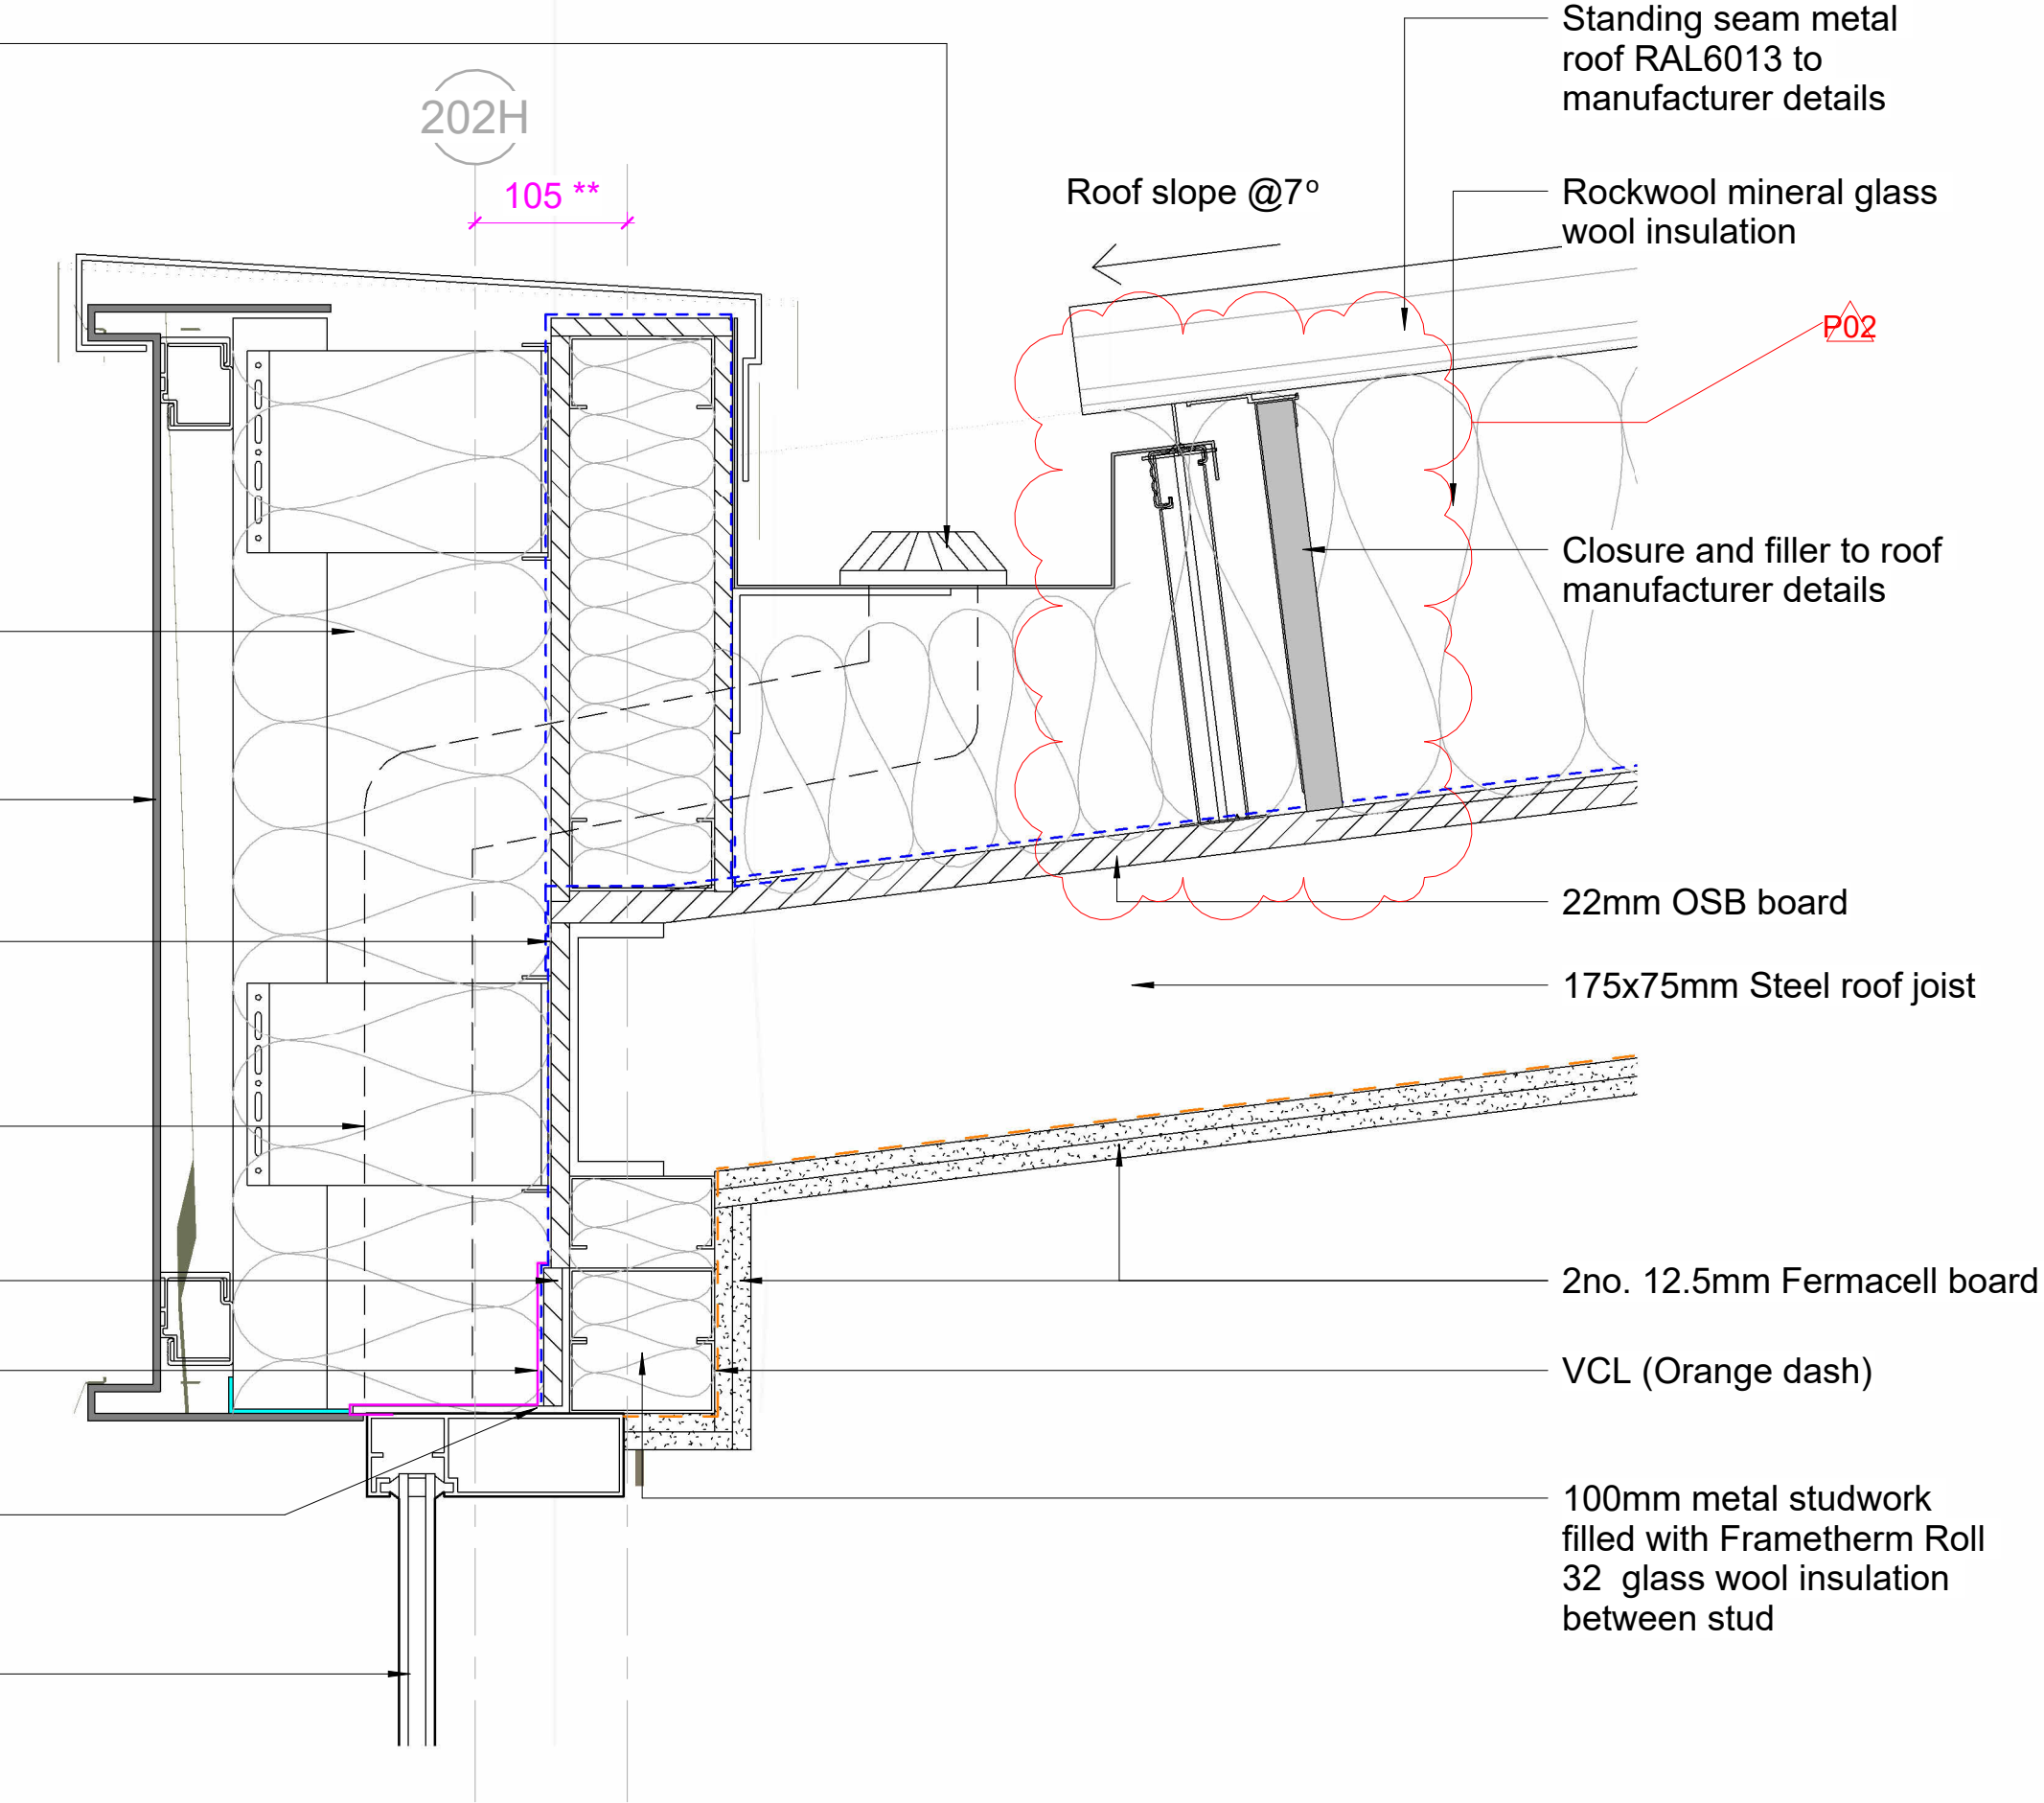

Over all wall build up to achieve u-value of 0.13Wm²K

- Breather membrane (Blue dash)
- 12.5mm weatherboard
- 220mm Rockwool Duo Rainscreen slab
- Aluminium rainscreen system to manufacturer design and details
- 00-Ground Floor 4000
- Galvanised metal angle at edge of slab
- Insulated perimeter board by others
- Waterproof membrane by others

DETAIL 1
1 : 5

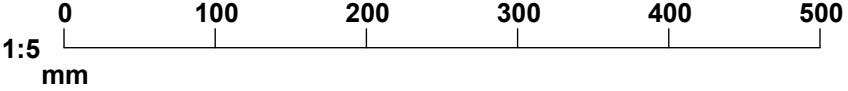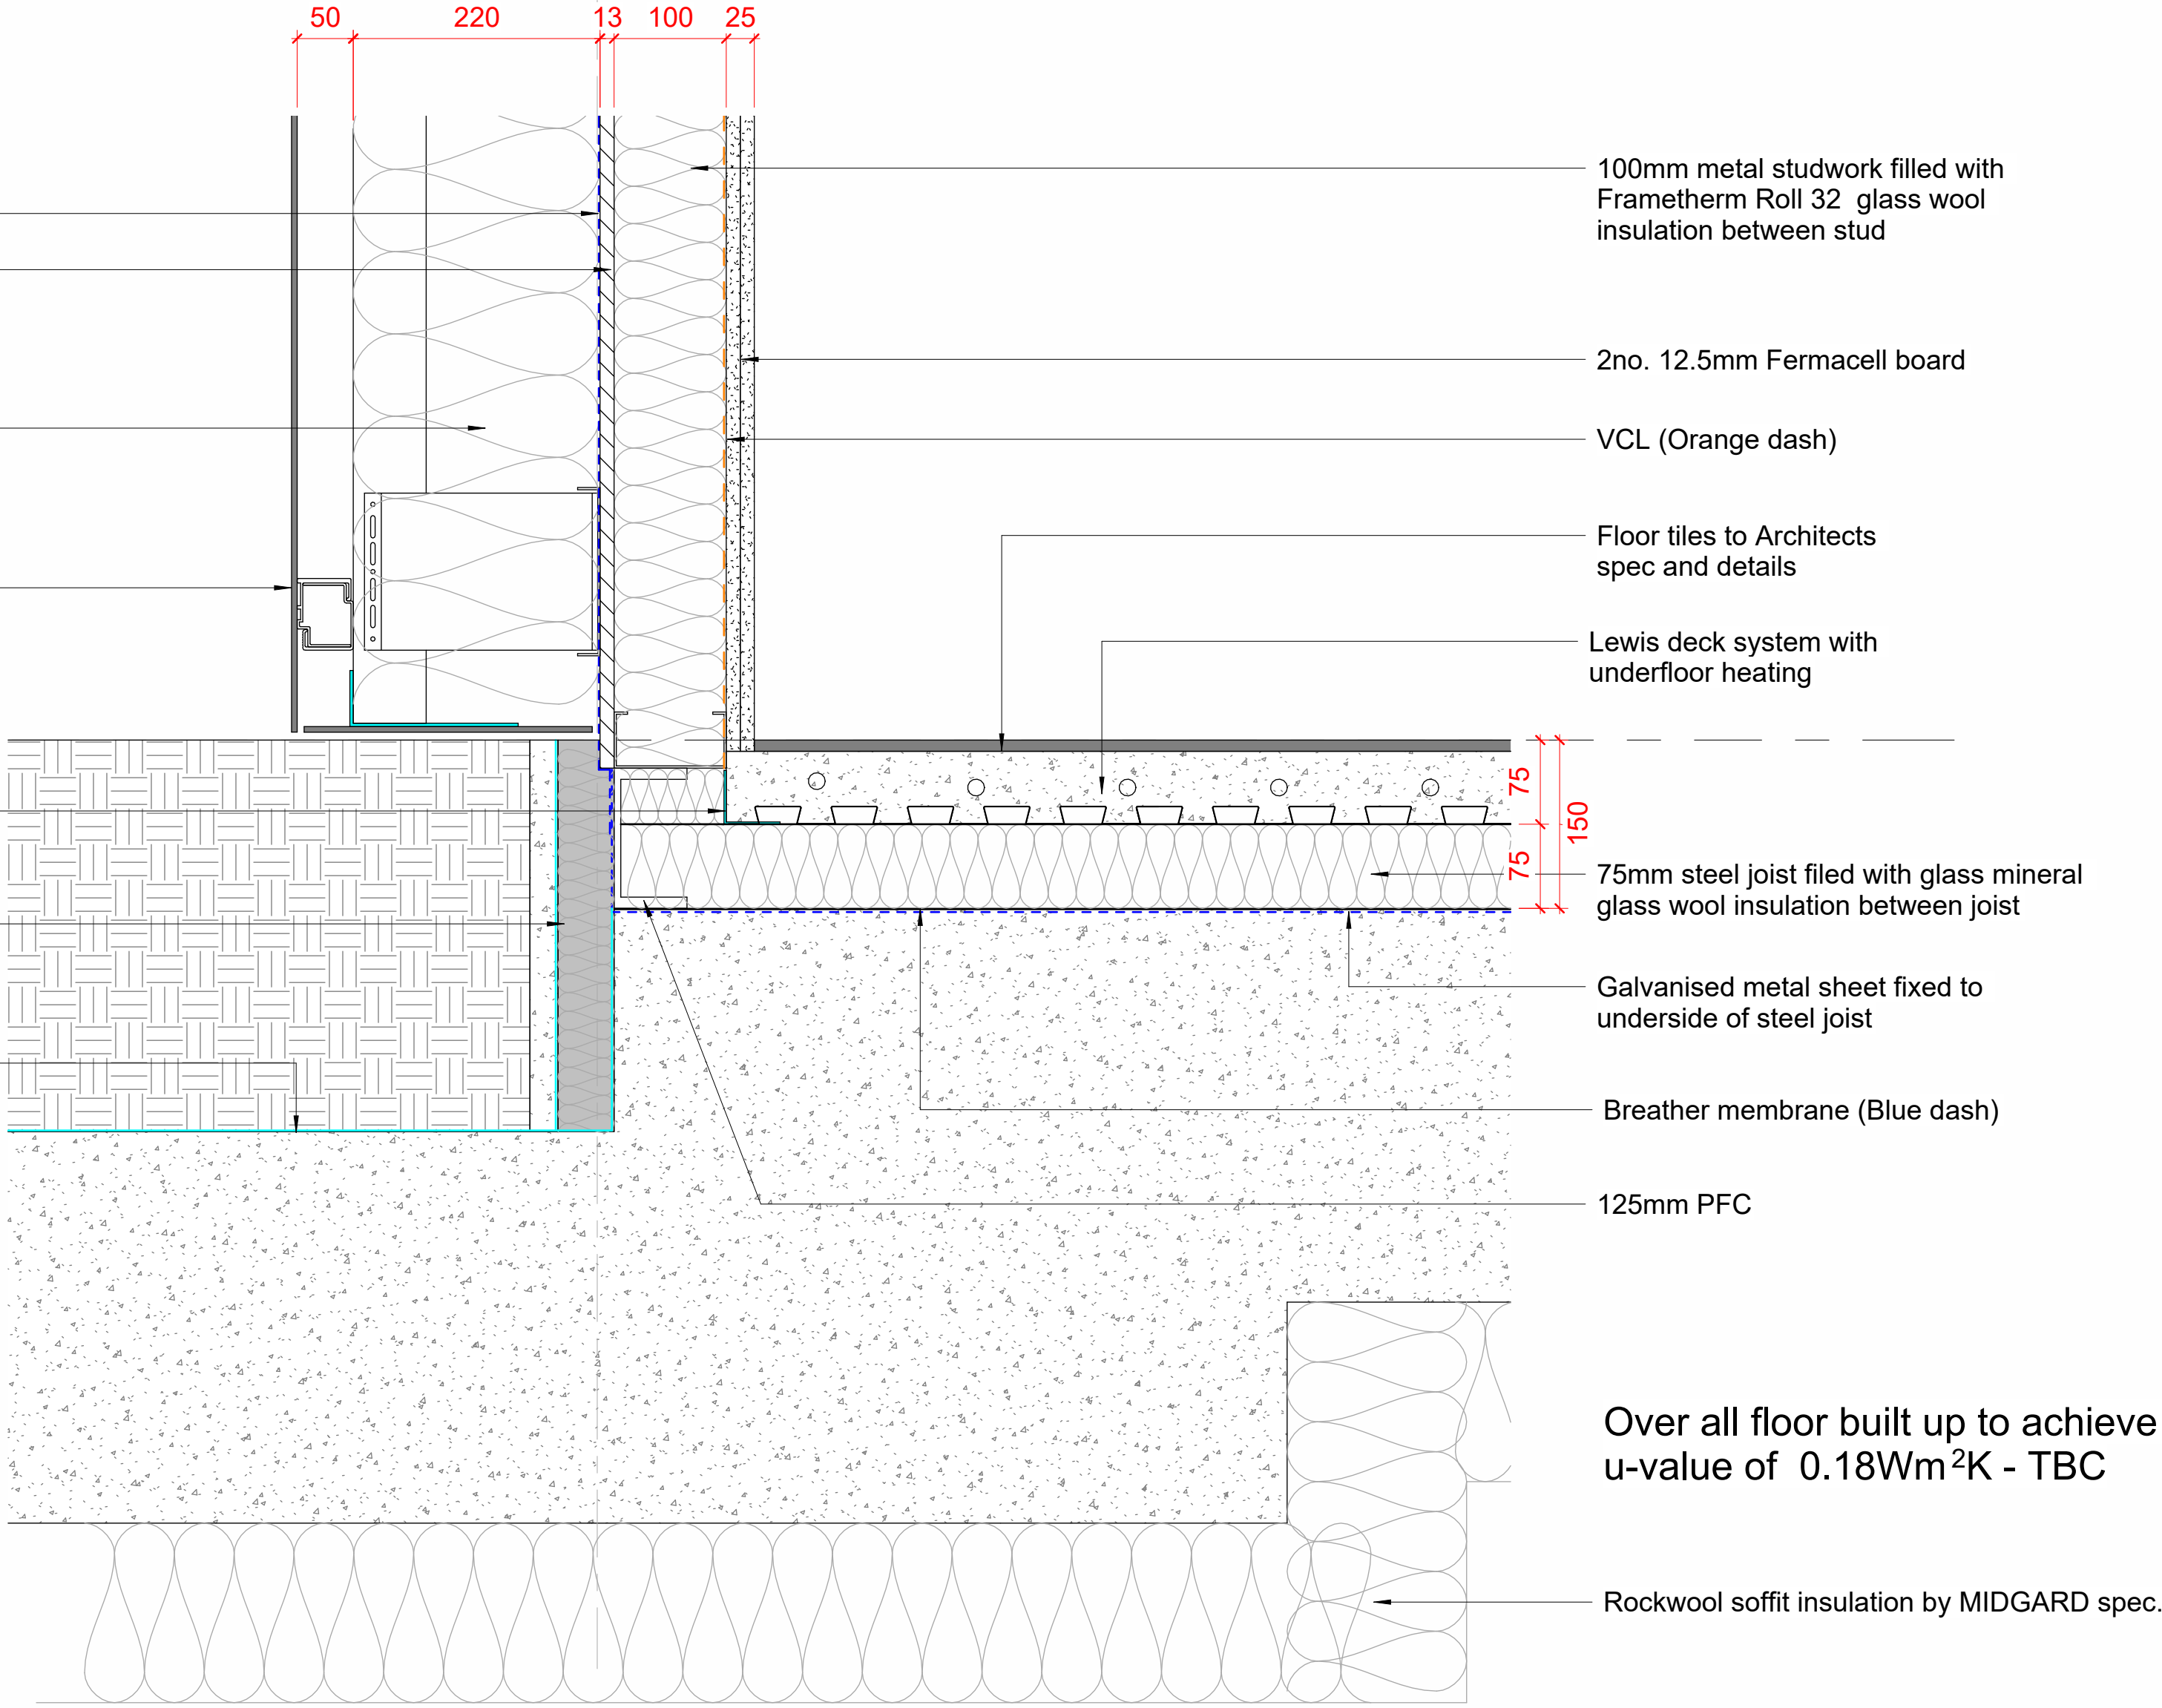

P02	02.06.23	PRELIMINARY - Roof OSB board updated	PN	SC
P01	30.03.23	PRELIMINARY	PN	SC
Rev	Date	Description	By	Chk

FOR APPROVAL

JRL

MODULAR

LIMITED

NEWARK

CARLTON WORKS COSSINGTON ROAD, NEWARK, NG23 8HT
TEL: 01636 821645
www.jrlgroup.co.uk

CLIENT

MIDGARD

PROJECT

BRENT CROSS TOWN - PAVILION
PLOT 202 - PAVILION, BRENT CROSS, NW 1AJ

TYPE

PLOT 202 - PAVILION
PROPOSED SECTION DETAILS SHEET 1

CREATION	SCALE @ A1	OR	CH	STATUS
07 JAN 2023	1 : 5	PN	SC	S3

DRAWING NO.

BXS- M2012- PRJ002- Y- MOD- DR- 23-0001- ZZ

Rev (Plot) (Project) (Rev) (Date) (Author) (Type) (Content) (Spec) (Drawn) (Check) (Level)

CHECK NO.

P02

REVISION


© COPYRIGHT ALL RIGHTS RESERVED.

THIS DRAWING MUST BE READ IN CONJUNCTION WITH ALL OTHER RELEVANT DRAWINGS AND INFORMATION.


ANY DISCREPANCIES MUST BE REPORTED TO JR MODULAR LTD IMMEDIATELY.

THIS DRAWING OR INFORMATION MUST NOT BE USED FOR CONSTRUCTION UNLESS EXPRESSLY ISSUED FOR CONSTRUCTION.


DO NOT SCALE OFF DRAWINGS. USE DISPLAYED DIMENSIONS.

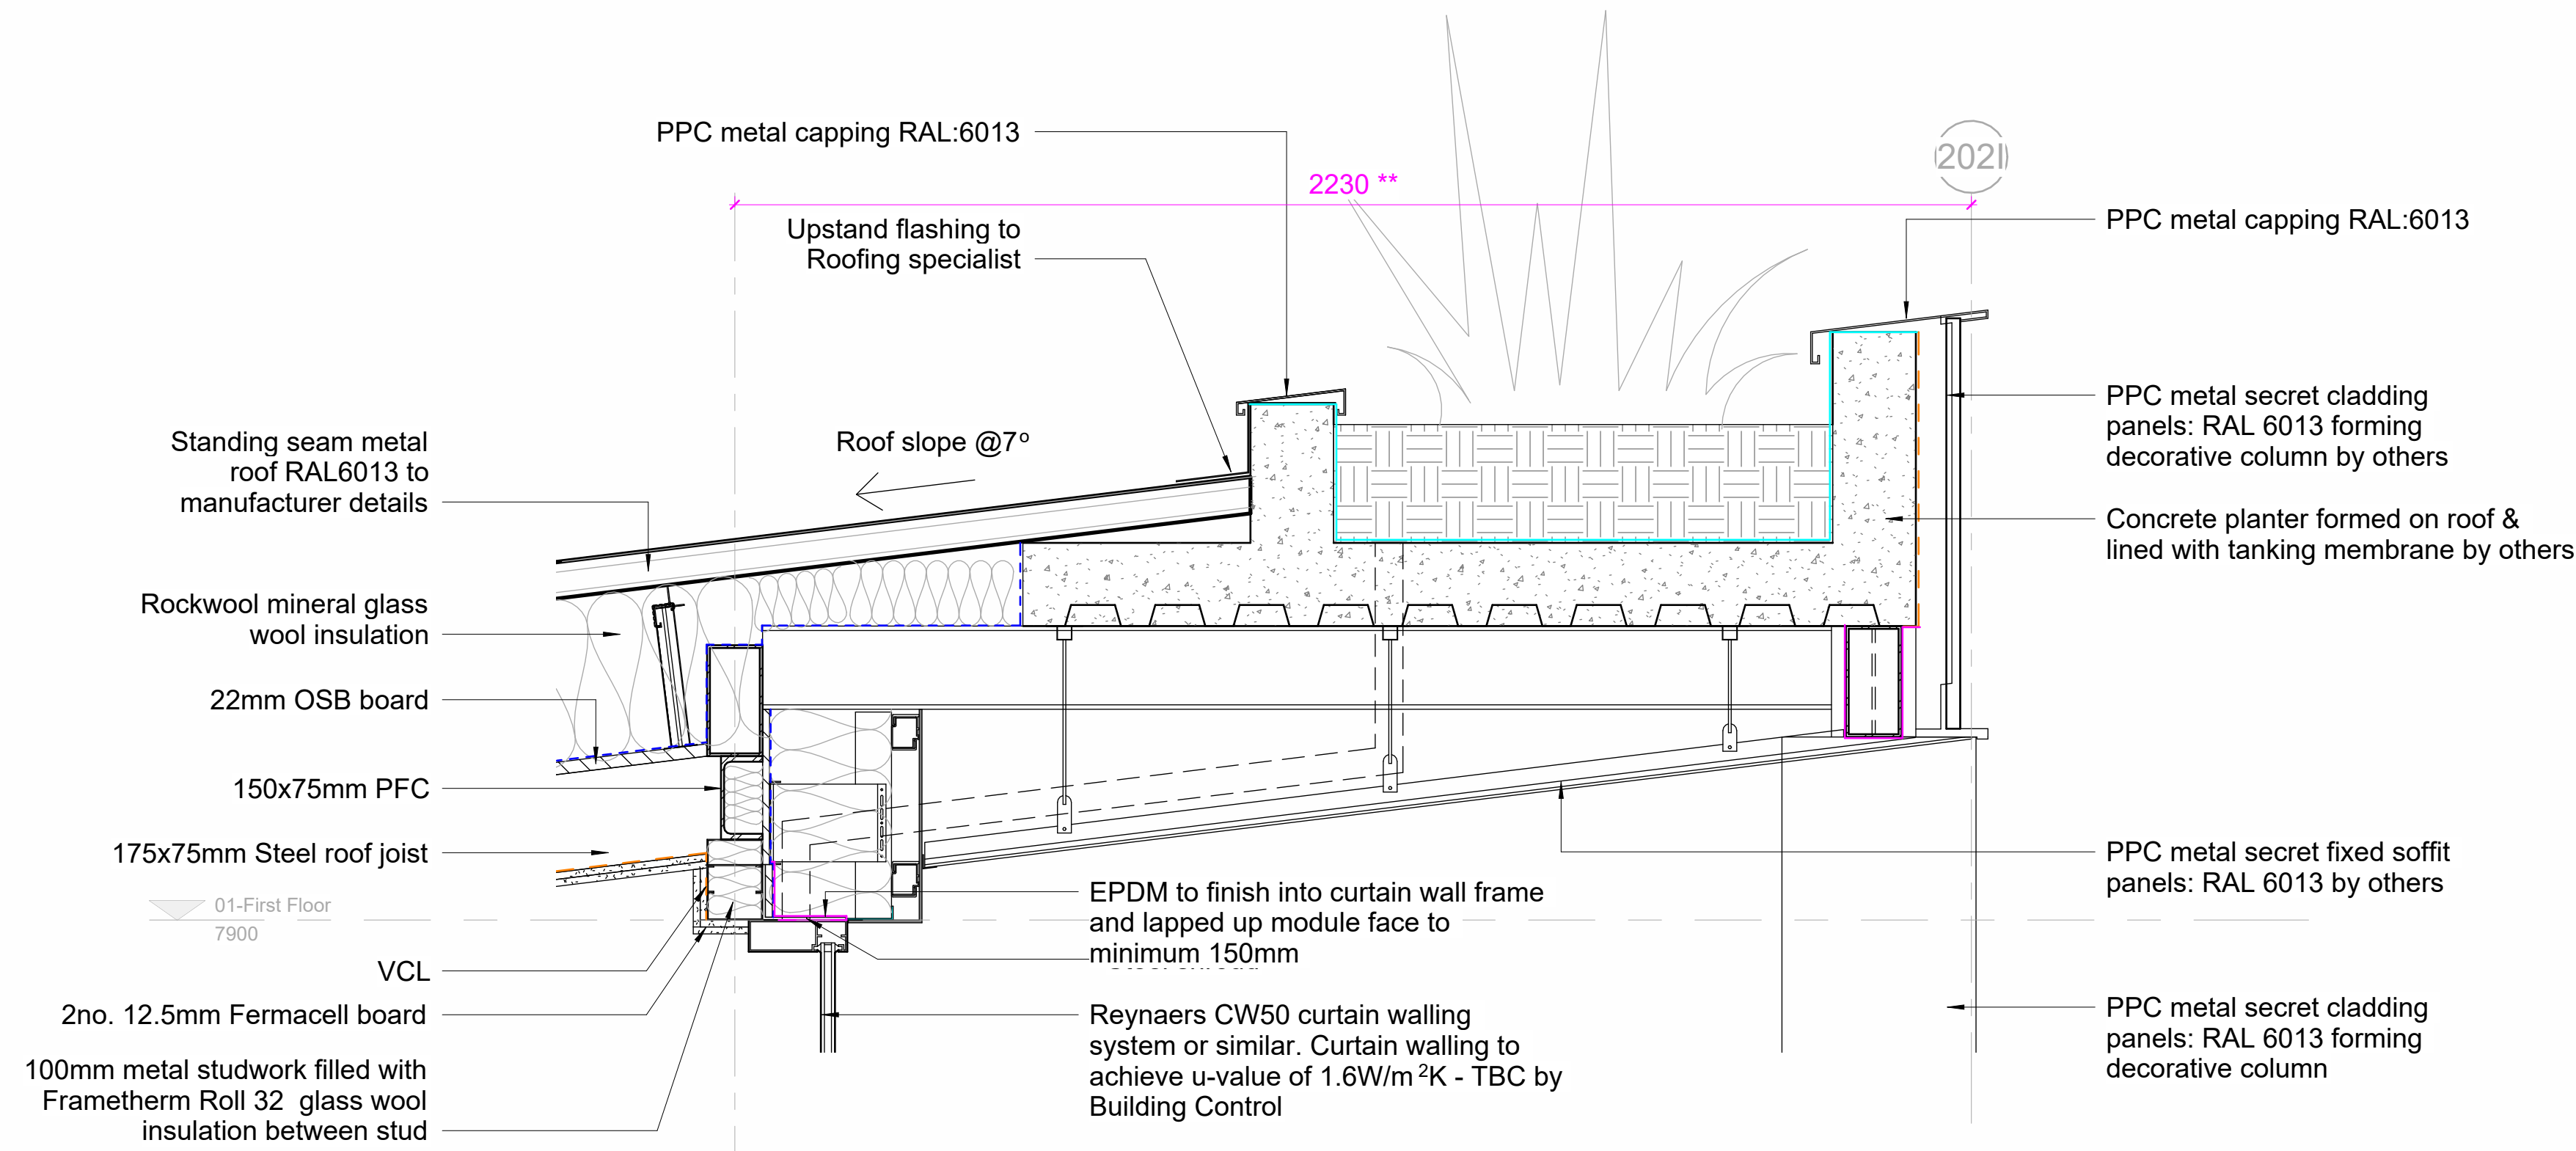

DETAIL 6
1 : 10

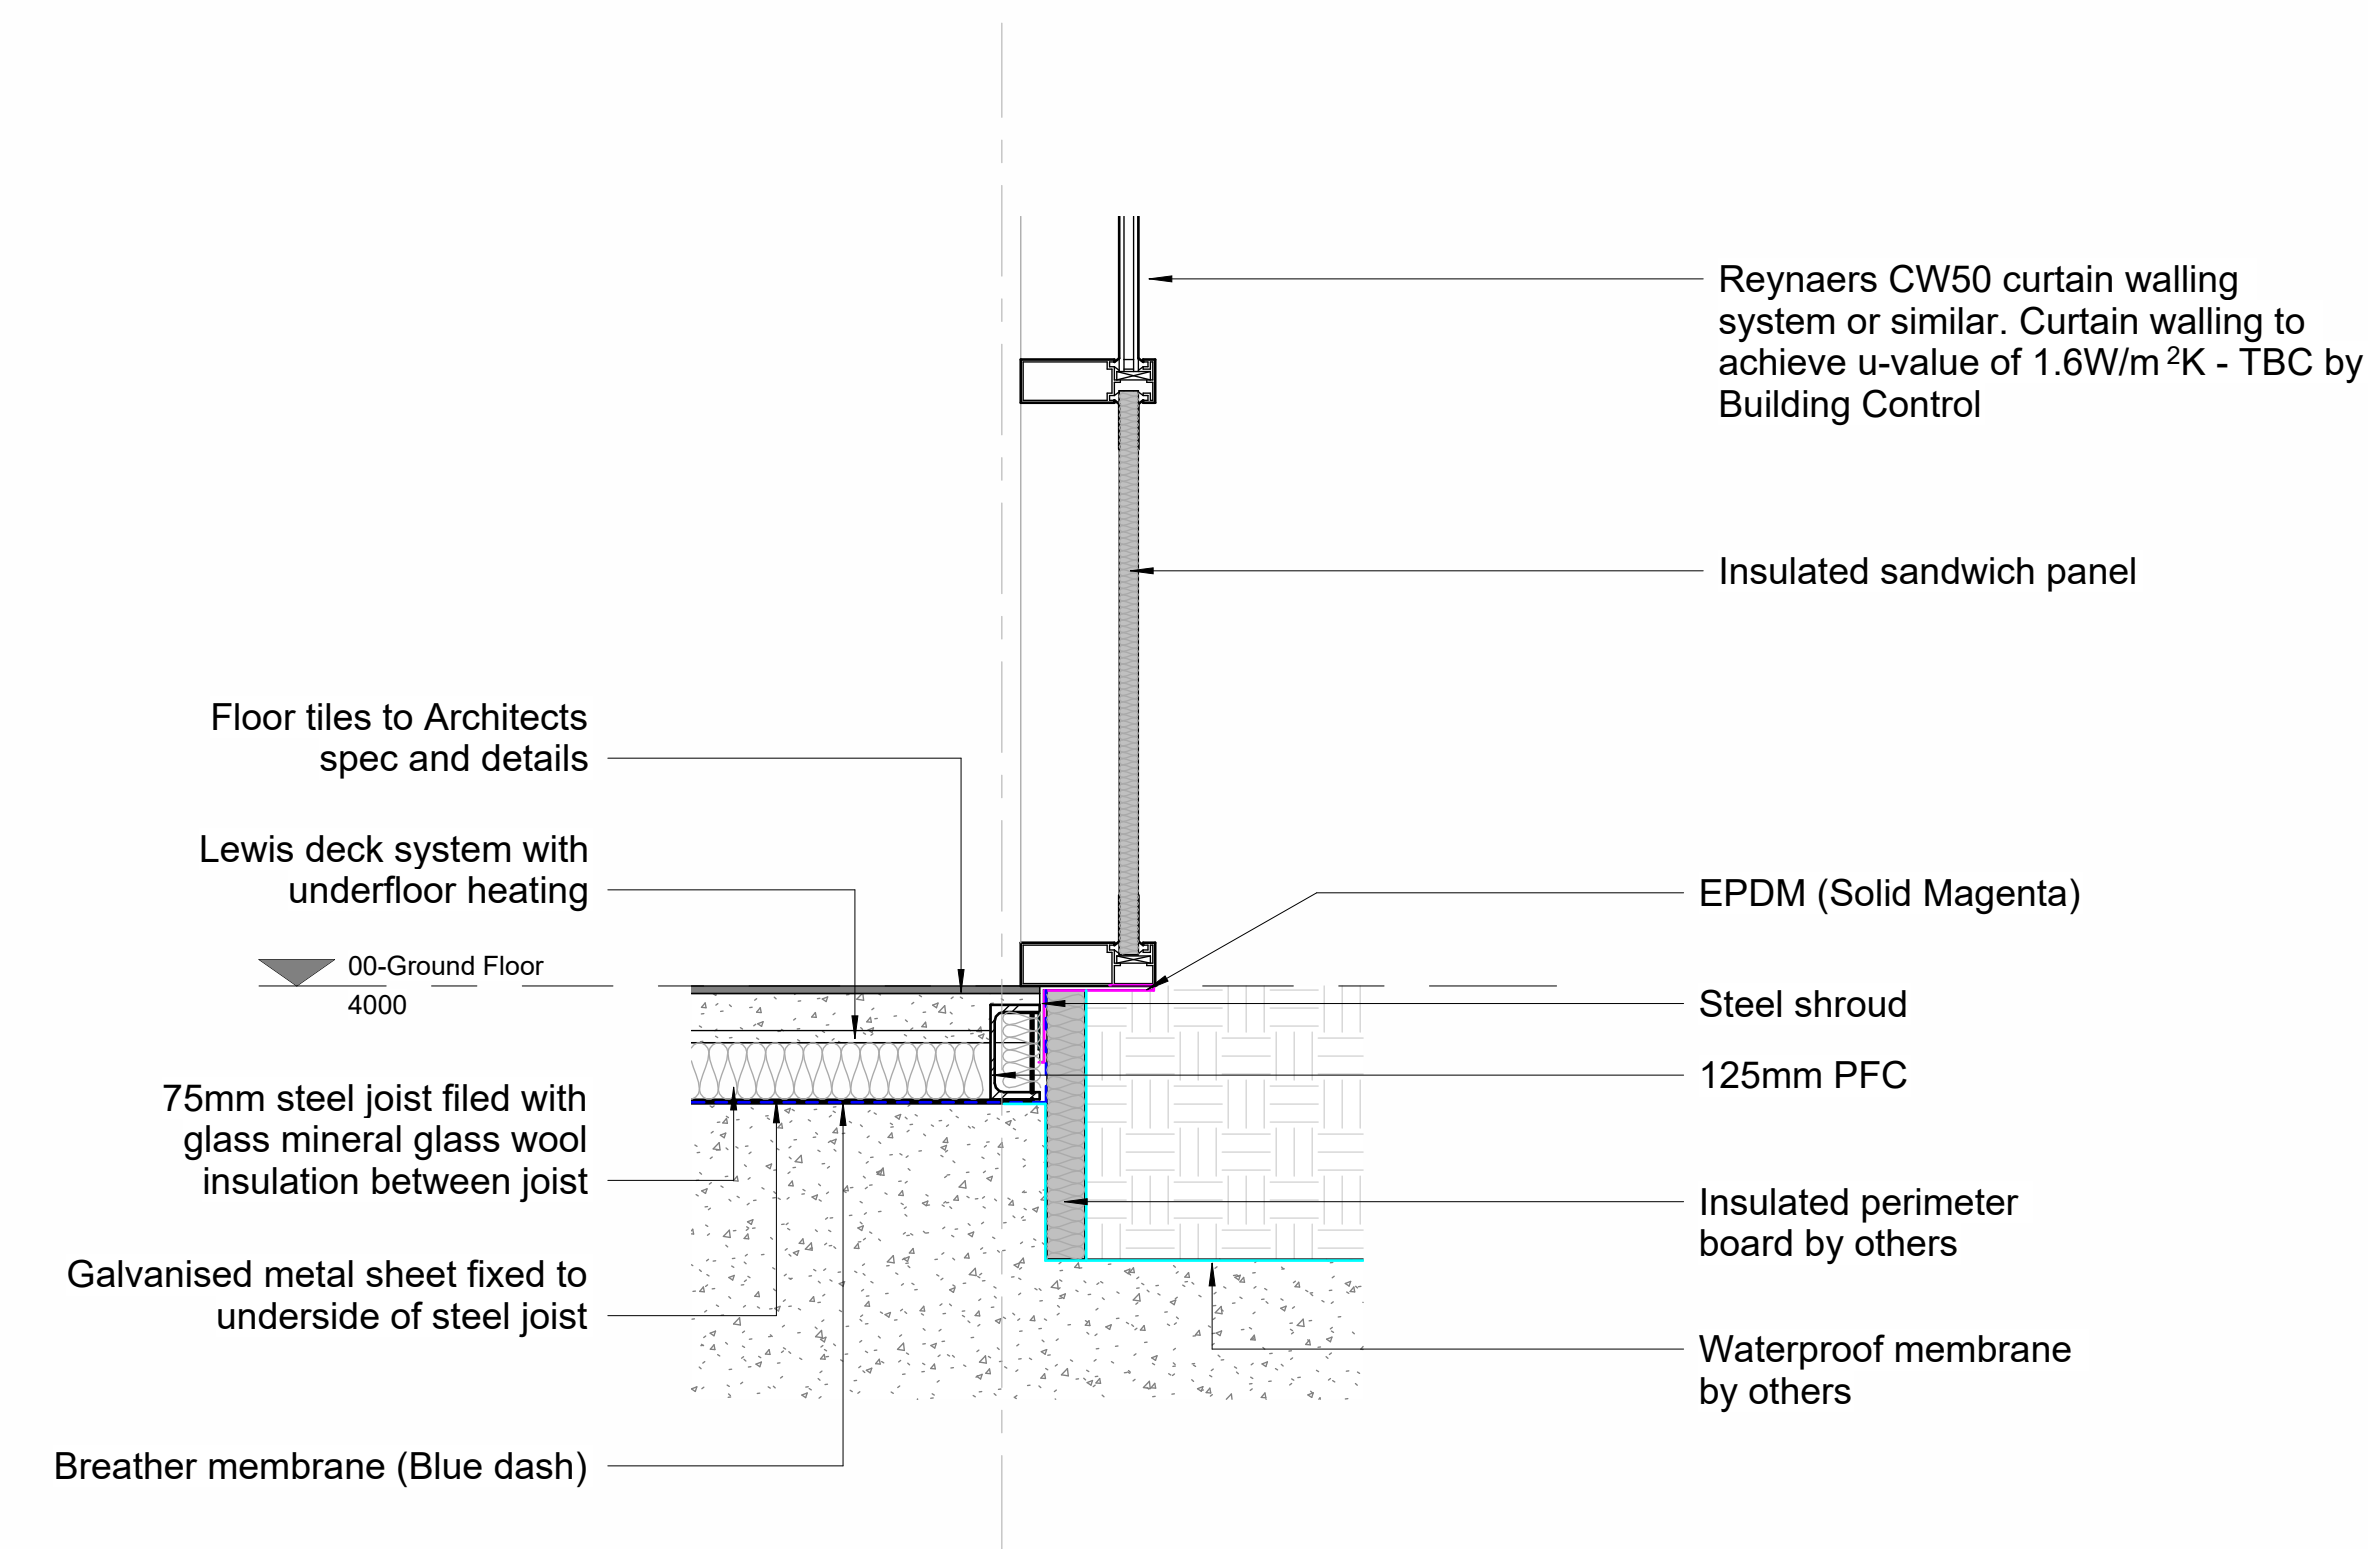

DETAIL 5
1 : 10

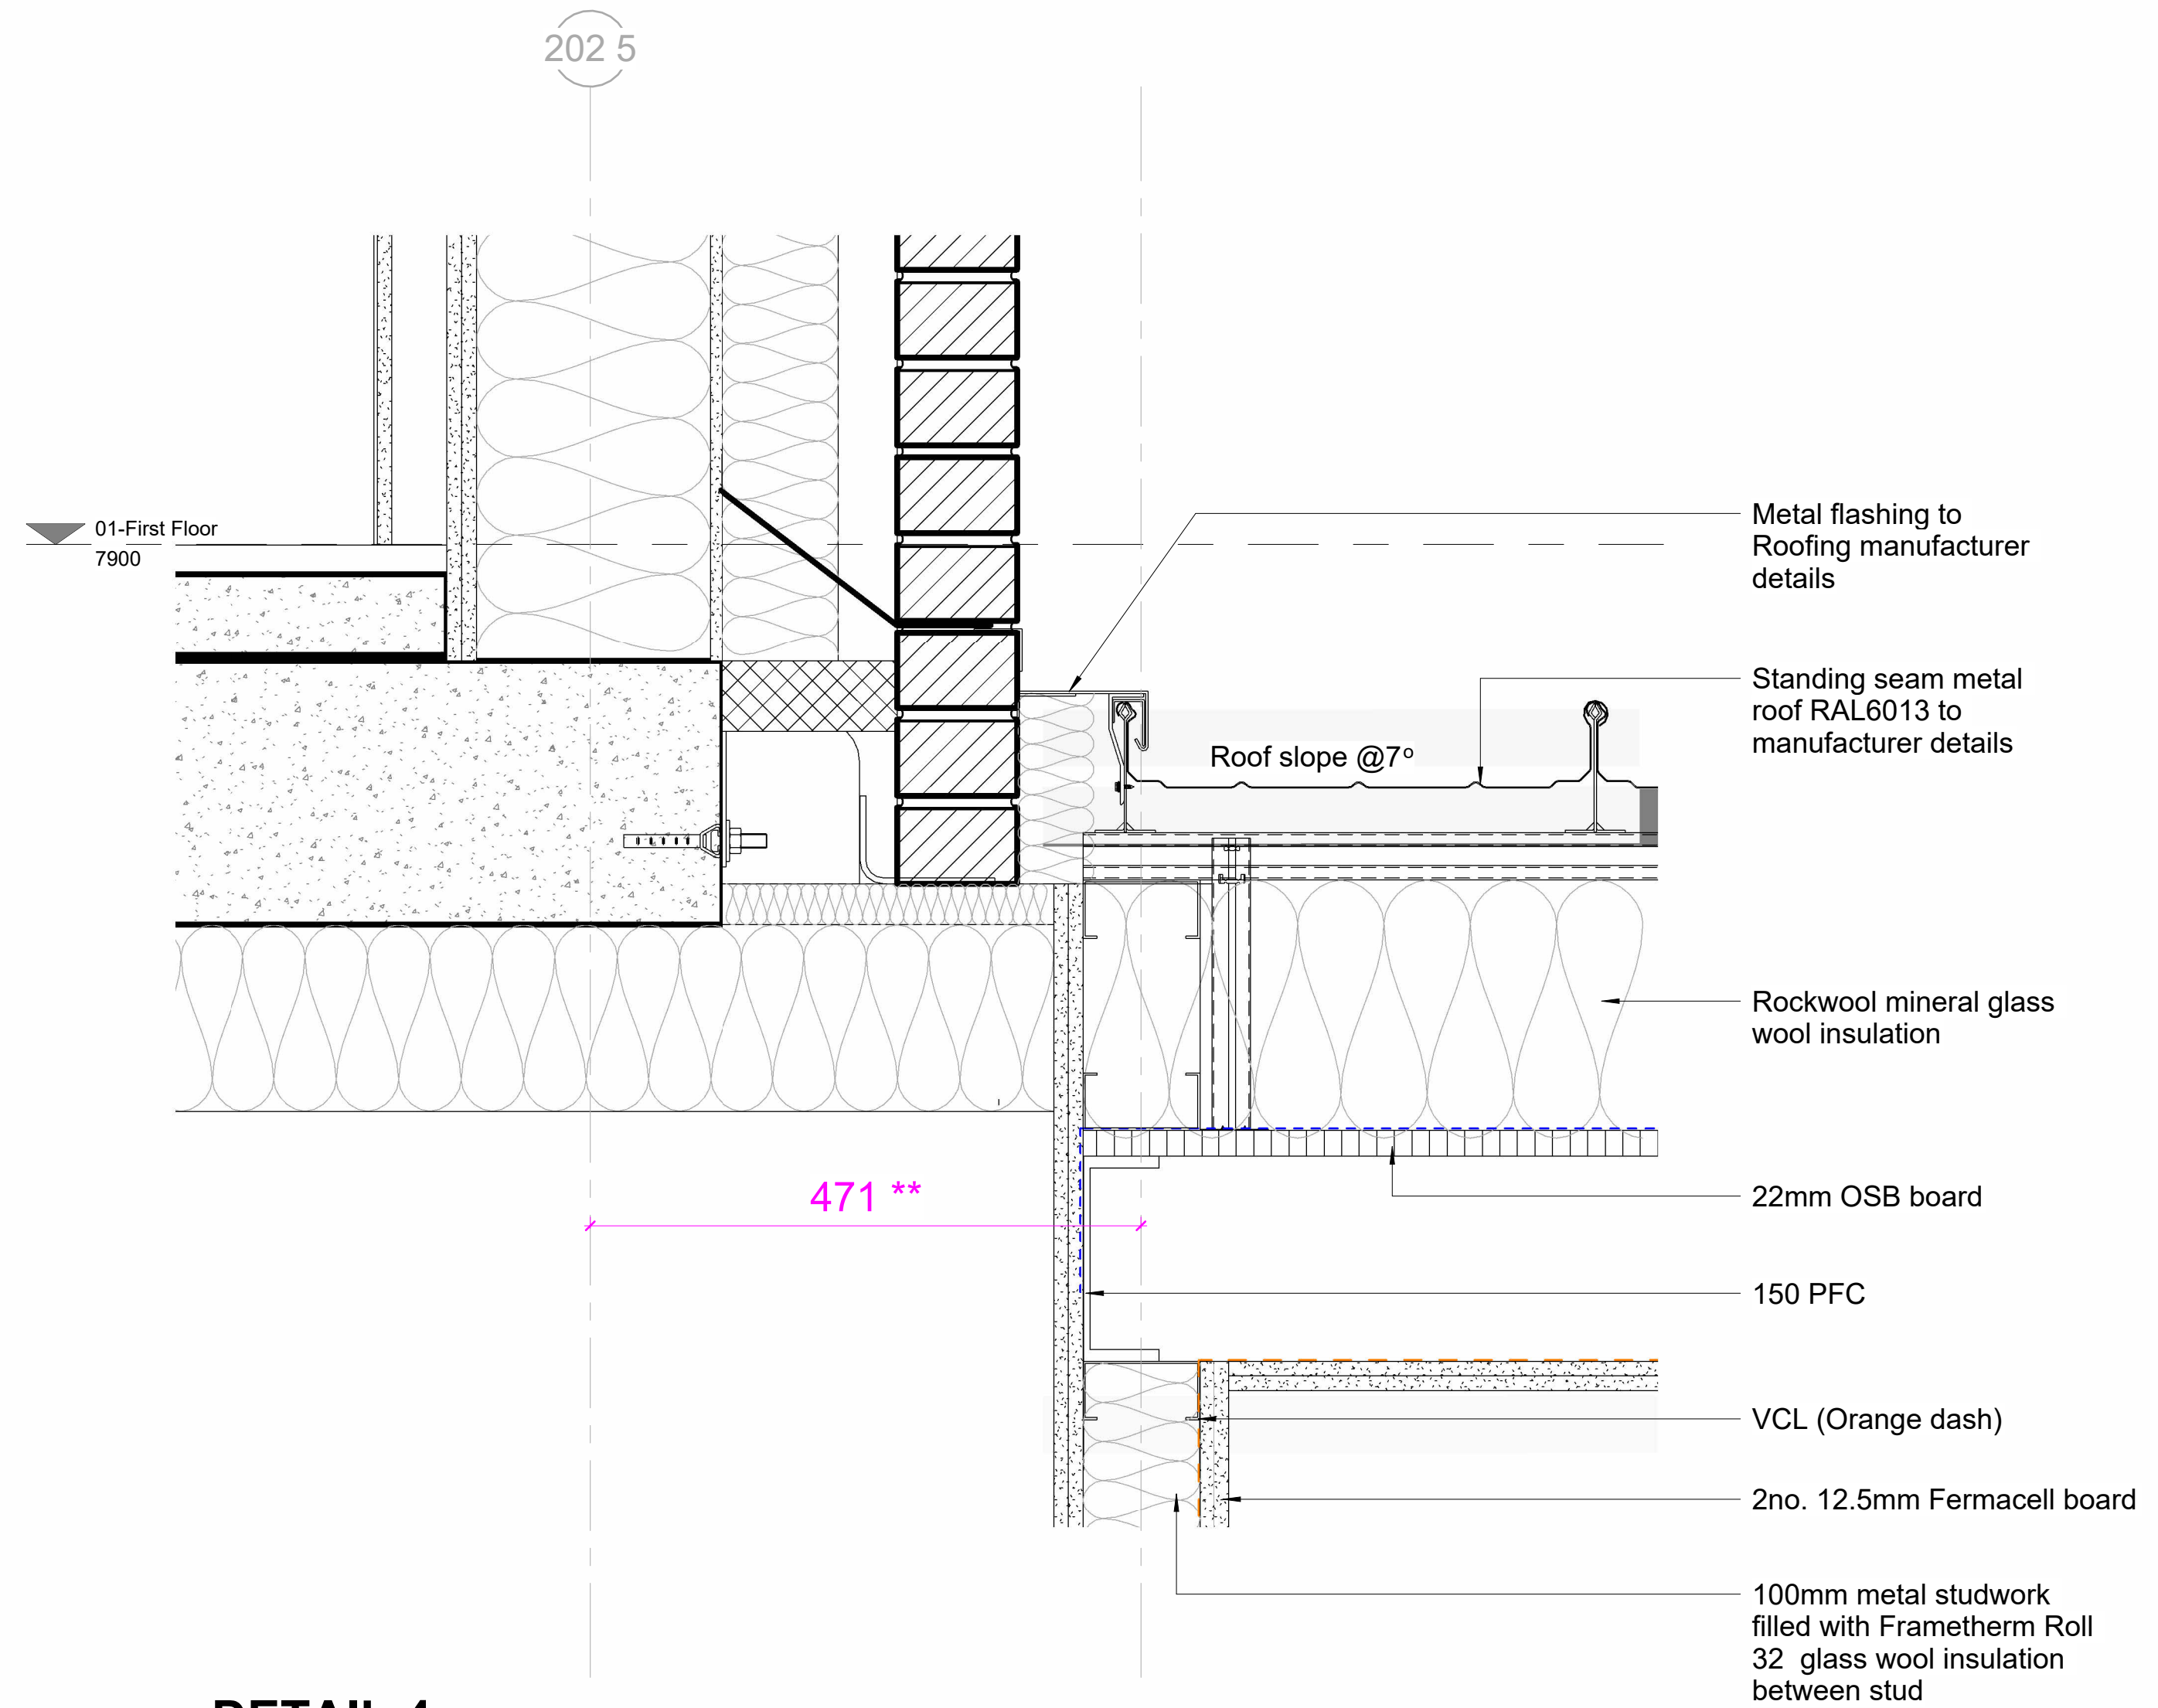

DETAIL 4
1 : 5

P01	02.06.23	PRELIMINARY	PN	SC
Rev	Date	Description	By	Chk
FOR APPROVAL				
JRL MODULAR LIMITED				
NEWARK				
CARLTON WORKS COSSINGTON ROAD, NEWARK, NG23 8HT TEL: 01636 821645 www.jrlgroup.co.uk				
CLIENT MIDGARD				
PROJECT BRENT CROSS TOWN - PAVILION PLOT 202 - PAVILION, BRENT CROSS, NW 1AJ				
TITLE PLOT 202 - PAVILION PROPOSED SECTION DETAILS SHEET 2				
CREATION	SCALE 1:1	OR	CH	STATUS
11 MAY 2023	As indicated	PN	SC	S3
DRAWING NO.				
BXS- M2012- PRJ002-Y- MOD- DR- 23-0002-ZZ				
Sht (Plot) Project Code Author Type Content Type Draw Number Level				
SHEET NO.				
P01				
REVISION				
© COPYRIGHT. ALL RIGHTS RESERVED. THIS DRAWING MUST BE READ IN CONJUNCTION WITH ALL OTHER RELEVANT DRAWINGS AND INFORMATION. ANY DISCREPANCIES MUST BE REPORTED TO JR MODULAR LTD IMMEDIATELY. THIS DRAWING OR INFORMATION MUST NOT BE USED FOR CONSTRUCTION UNLESS EXPRESSLY ISSUED FOR CONSTRUCTION. DO NOT SCALE OFF DRAWINGS. USE DISPLAYED DIMENSIONS.				